



מתחם מגורי סטודנטים אורחים:

המבנה תוכנן בצורה ייחודית של שתי קומות, כאשר הקומה הראשונה יושבת על הקרקע והקומה השנייה מרחפת ברובה באוויר בצורת ר'!



השימוש בעמודים תומכים בעיצוב המבנה מדגישים תחכום הנדסי ומתכננים מרחב פתוח שמזמין אינטראקציות חברתיות ומאפשר תנועה חופשית בין הפנים לחוץ.

הבחירה בעיצוב זה נובעת מהרצון ליצור חיבור טבעי עם הנוף הקיים, כך שכל החללים פונים לכיוון הנוף ומנצלים אותה בצורה מיטבית.

העמדת הקומות בצורה זו מאפשרת למבנה להשתלב בסביבה בצורה הרמונית, תוך יצירת תחושת מרחב אווירית.

המגרש משופע לכיוון דרום בהפרש גבהים של כ 2 מטרים, בהתחשב במבטים לנוף בחרתי למקם את המעונות בחלקו הגבוהה של המגרש, כך שיתאפשר לכל חדרי האירוח להנות מהנוף.

השראה:

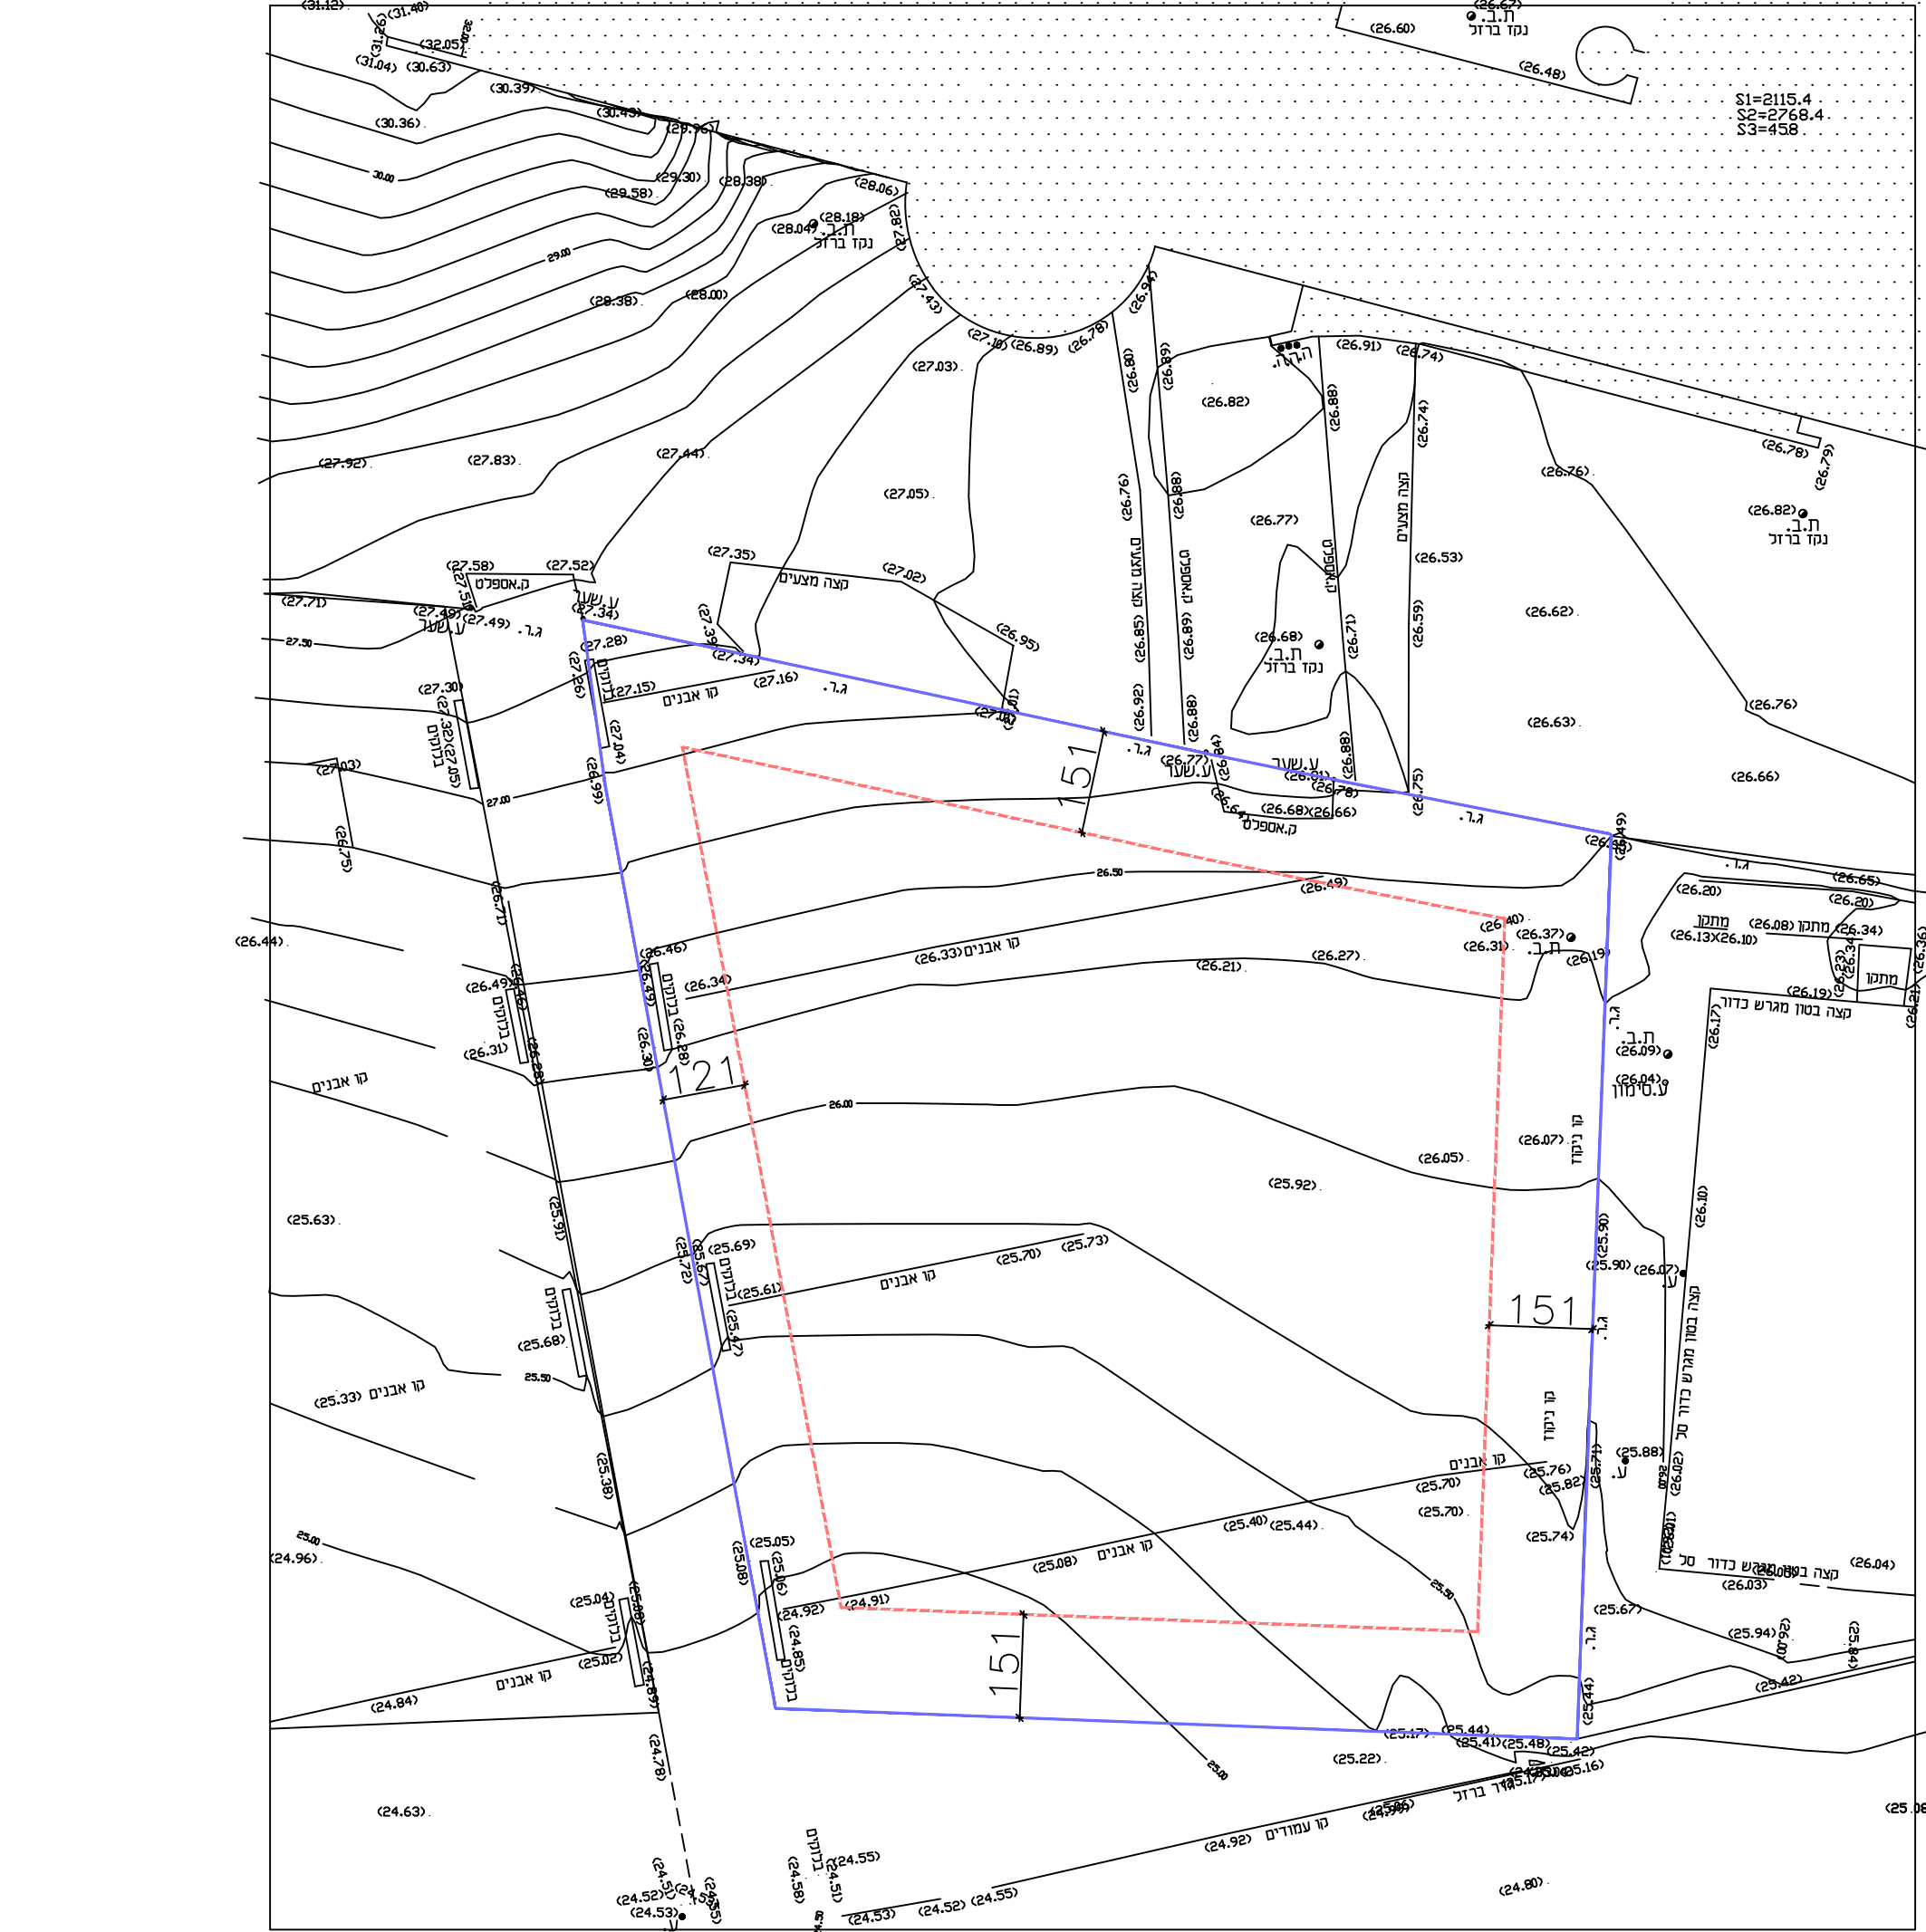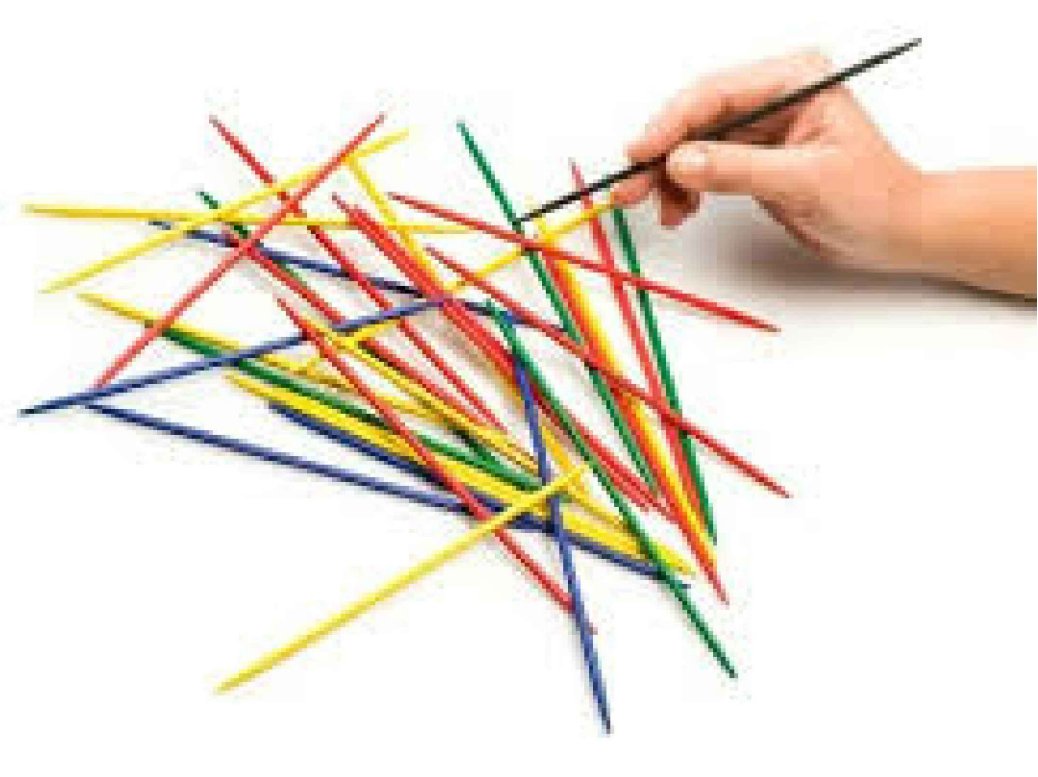

נתוני המגרש:

המגרש ממוקם בין המכללה הטכנולוגית למרכז האקדמי רופין. ממערב לקמפוס המכללה הטכנולוגית ומדרום למרכז האקדמי בקרבה לספריה שנמצאת מצפון.

מגבלת בנייה של 500 מ"ר. קו בניין מערבי 4 מ) גישה לכביש) קו בניין 5 מ בשאר הצלעות.



מגמת אדריכלות
מחזור ס'
ב'

שם הקורס:
תכנון אדריכלי

פרוייקט מעונות
סטודנטים

מס גיליון:
2/8

קנ"מ:
1-100





נושא גיליון:

שם המנחה:
נעמה שבתאי ציזר

תאריך:
18.9.24

מגישה:
כרמל סעדון

תנועה ושימושים לפי קומות:


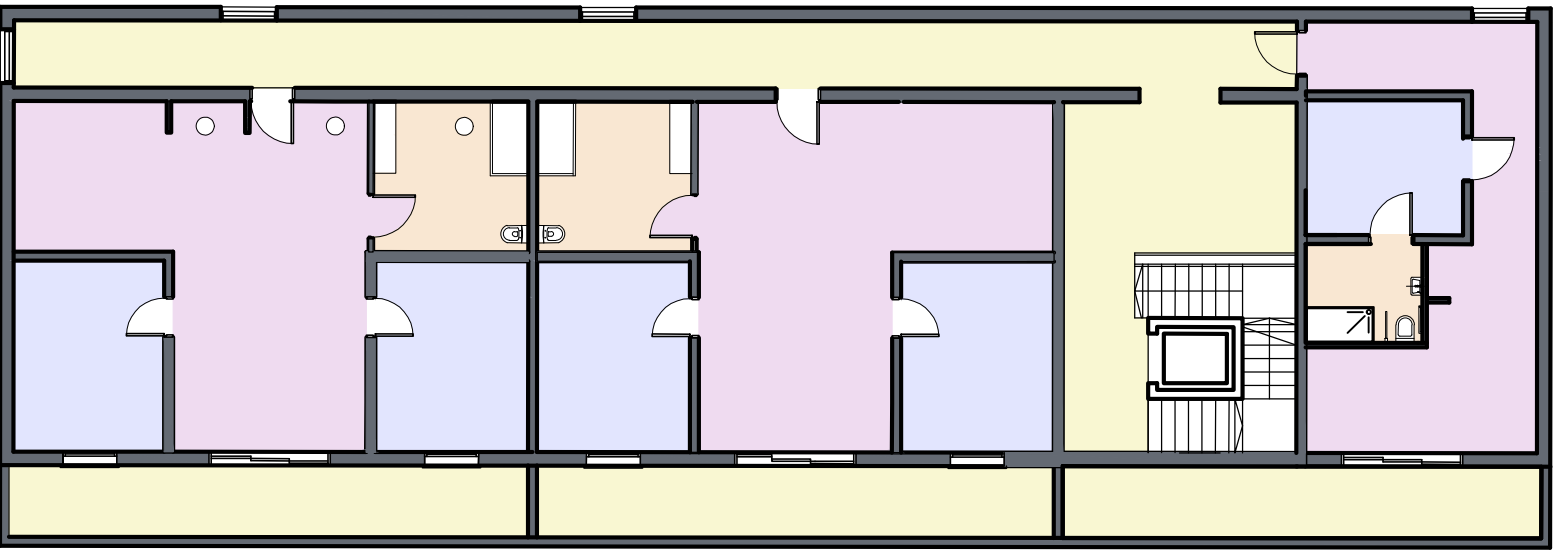
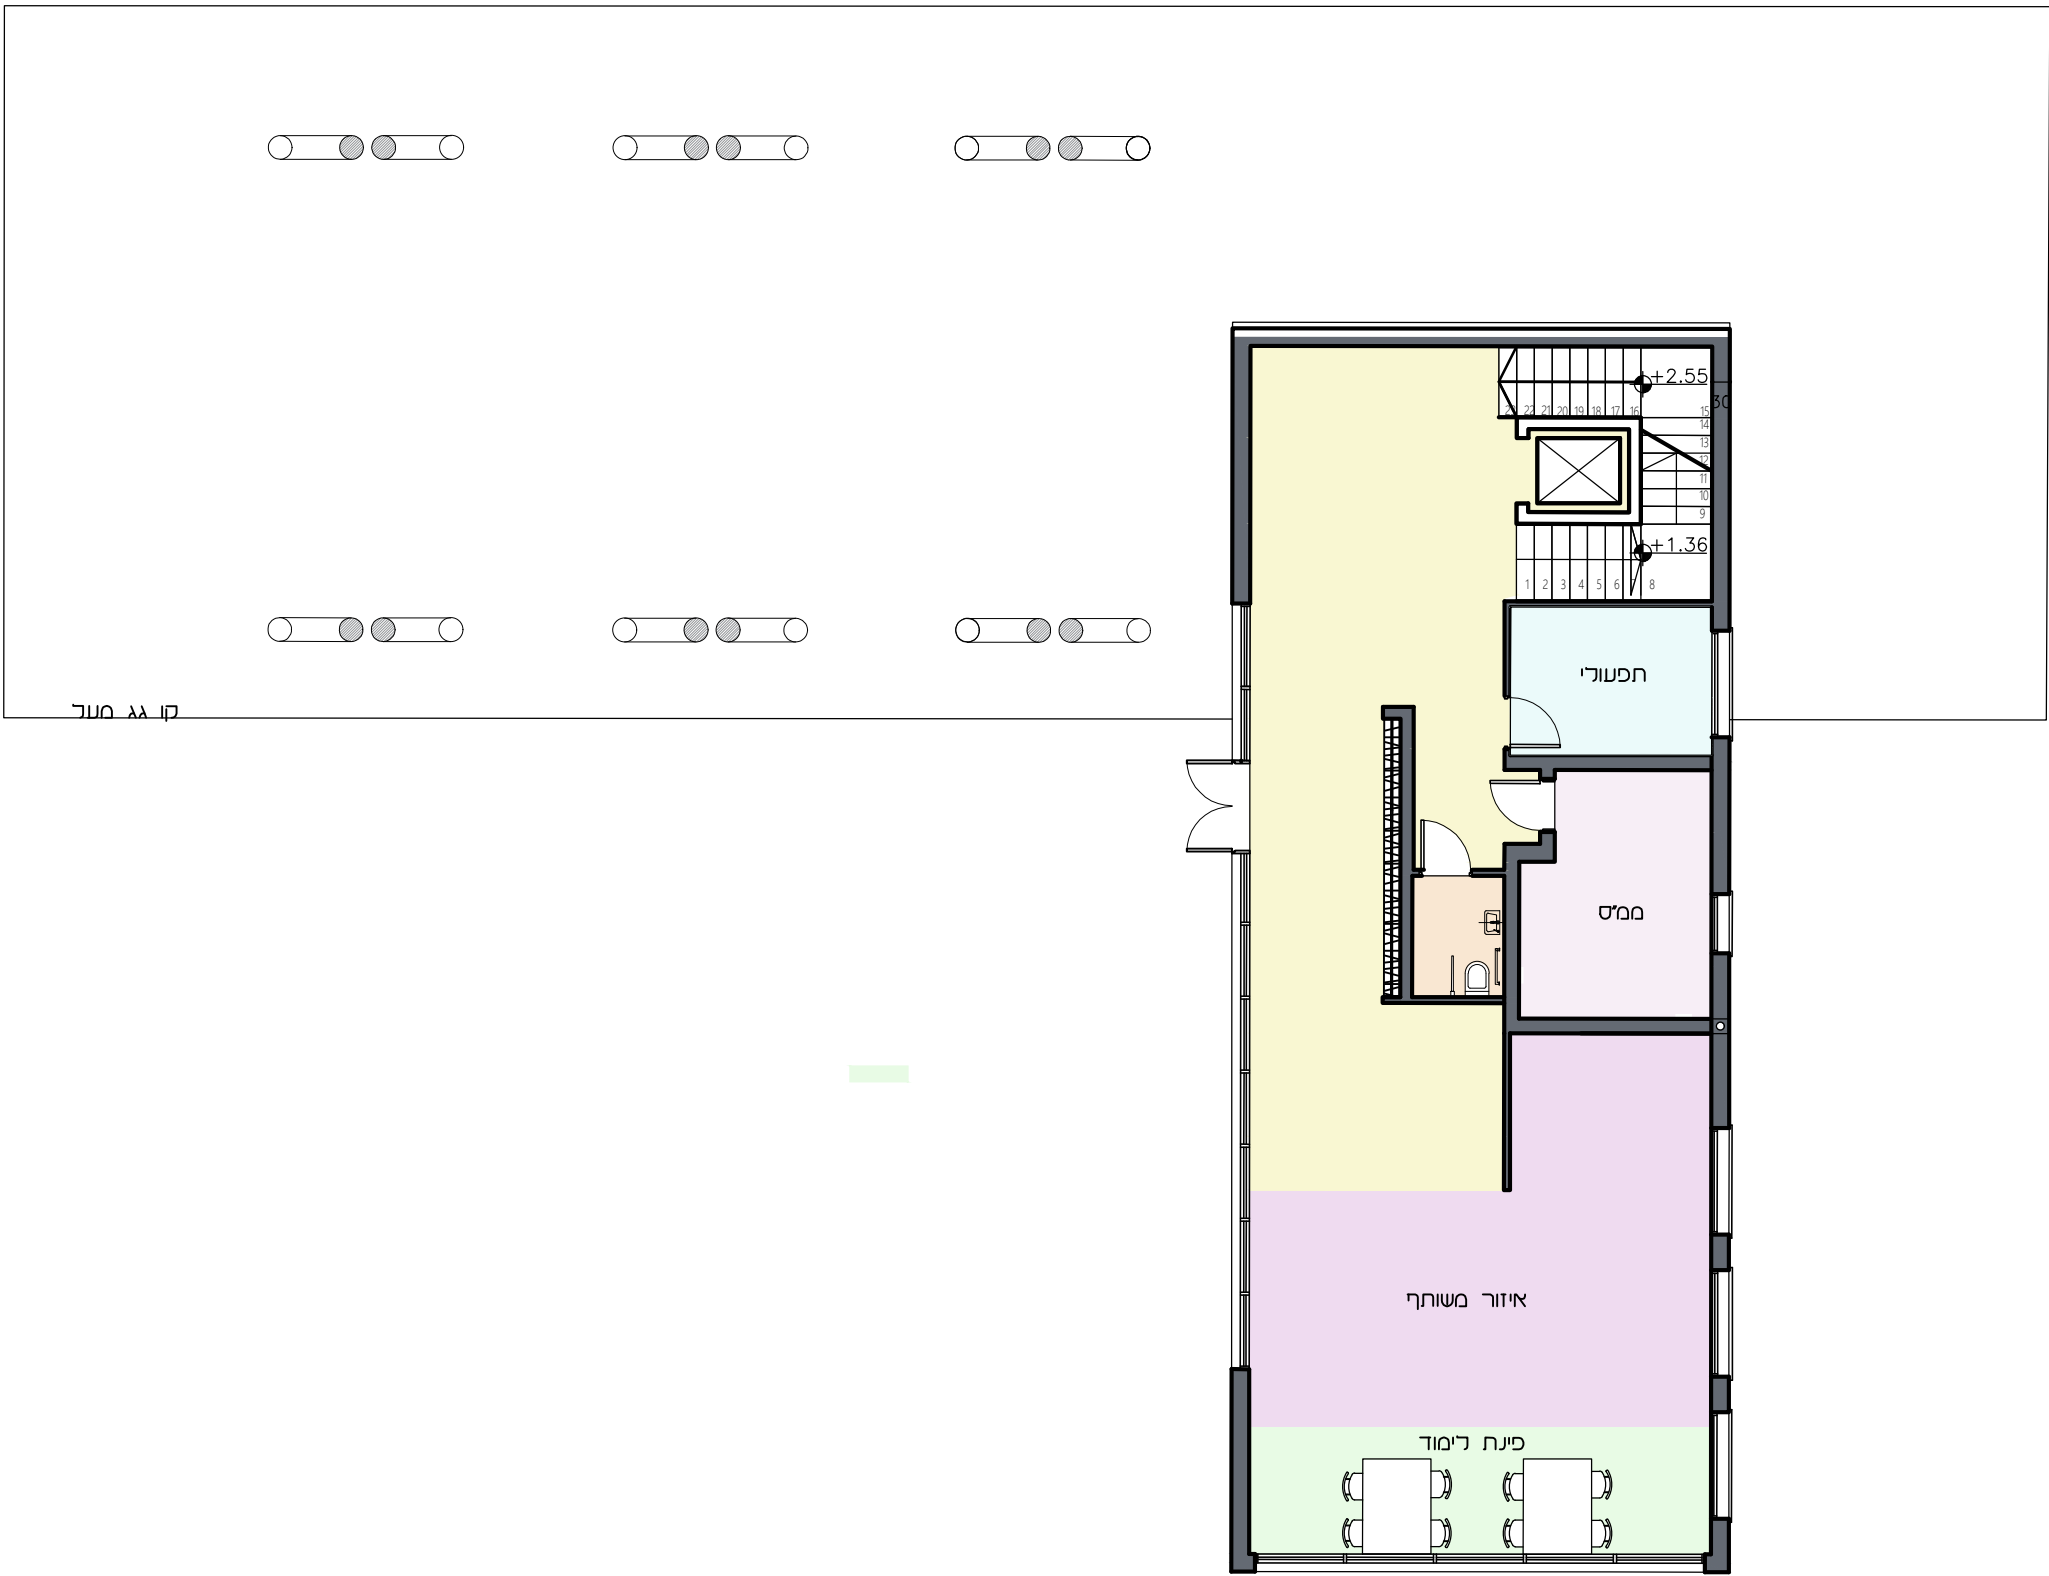



קומה א

מקרא שטחים:

- מעברים
- ממ"ס
- שירותים
- תפעולי
- איוזר משותף
- איוזר לימוד
- חדרי שינה

סקיצות ראשוניות:

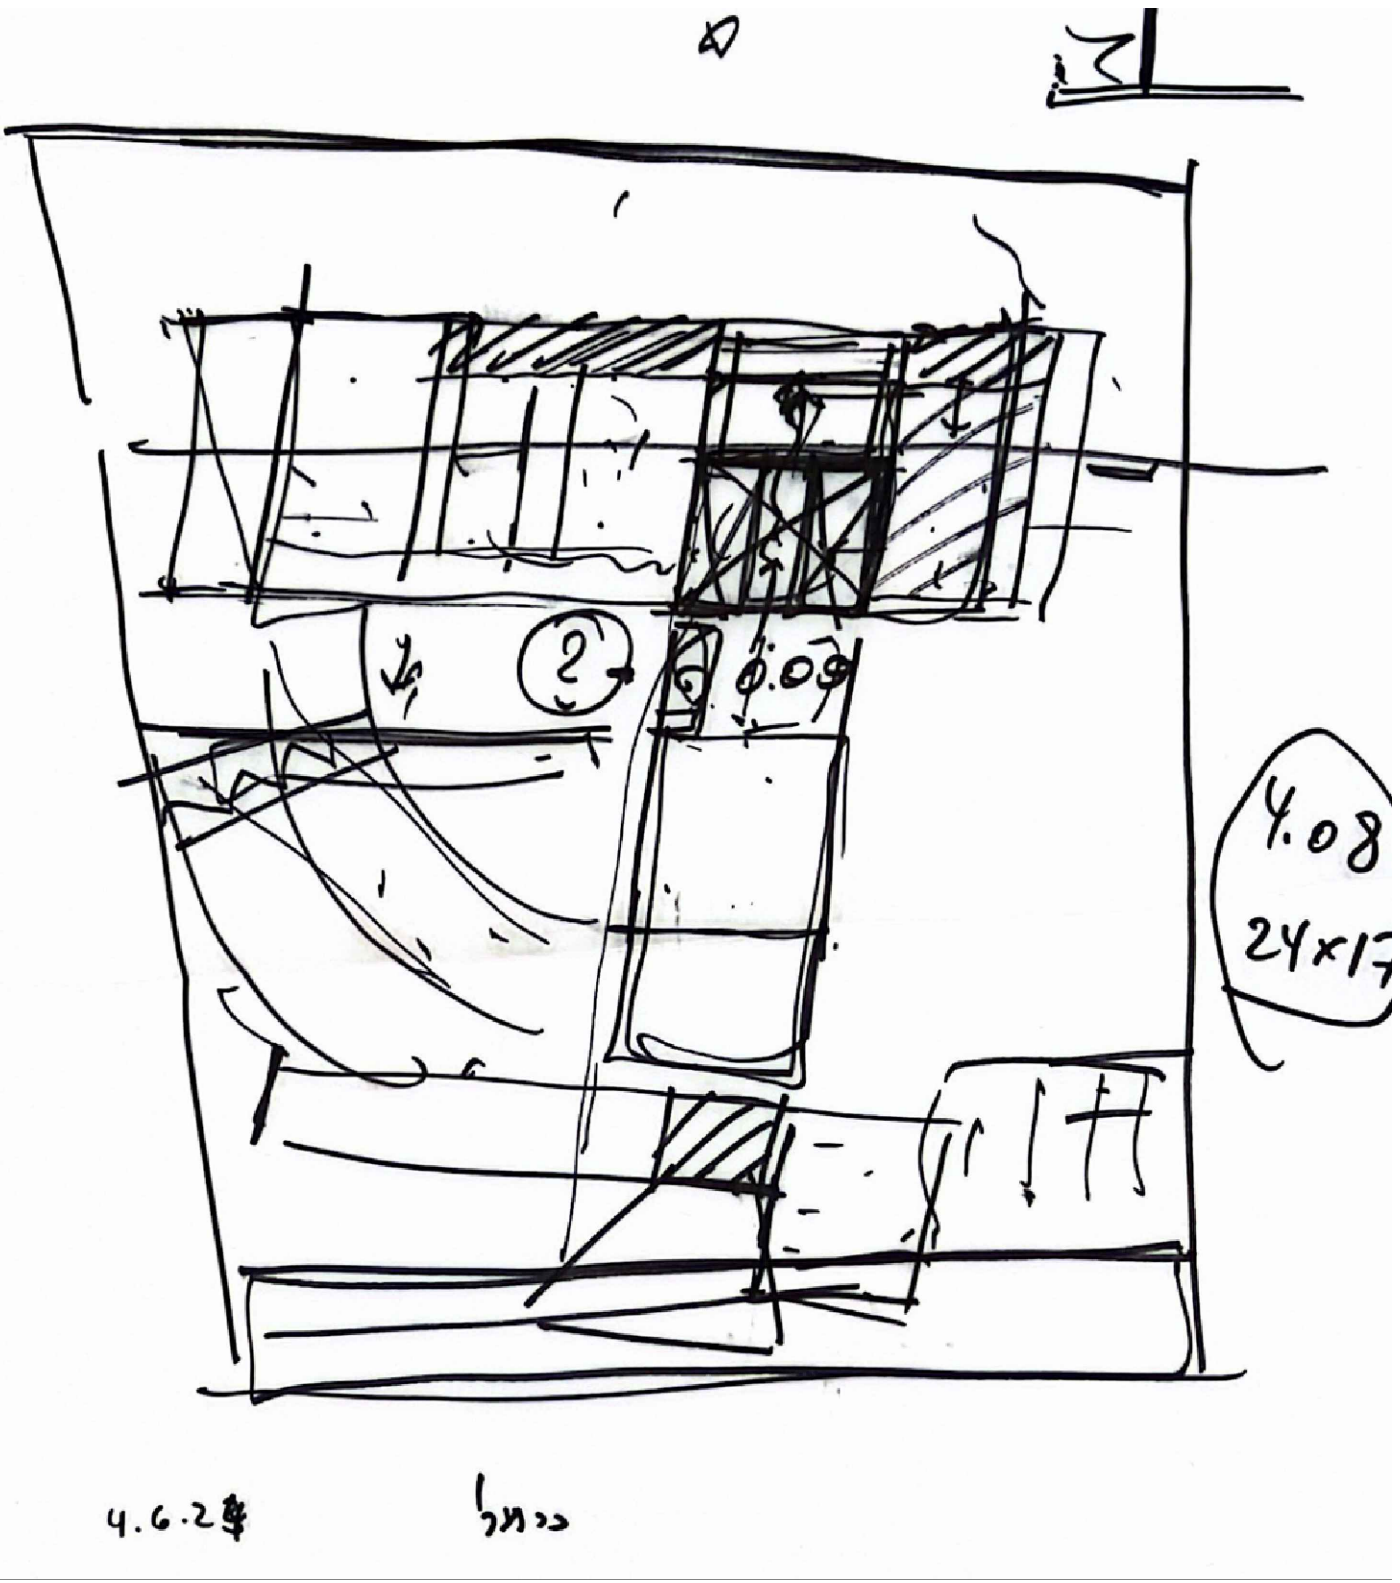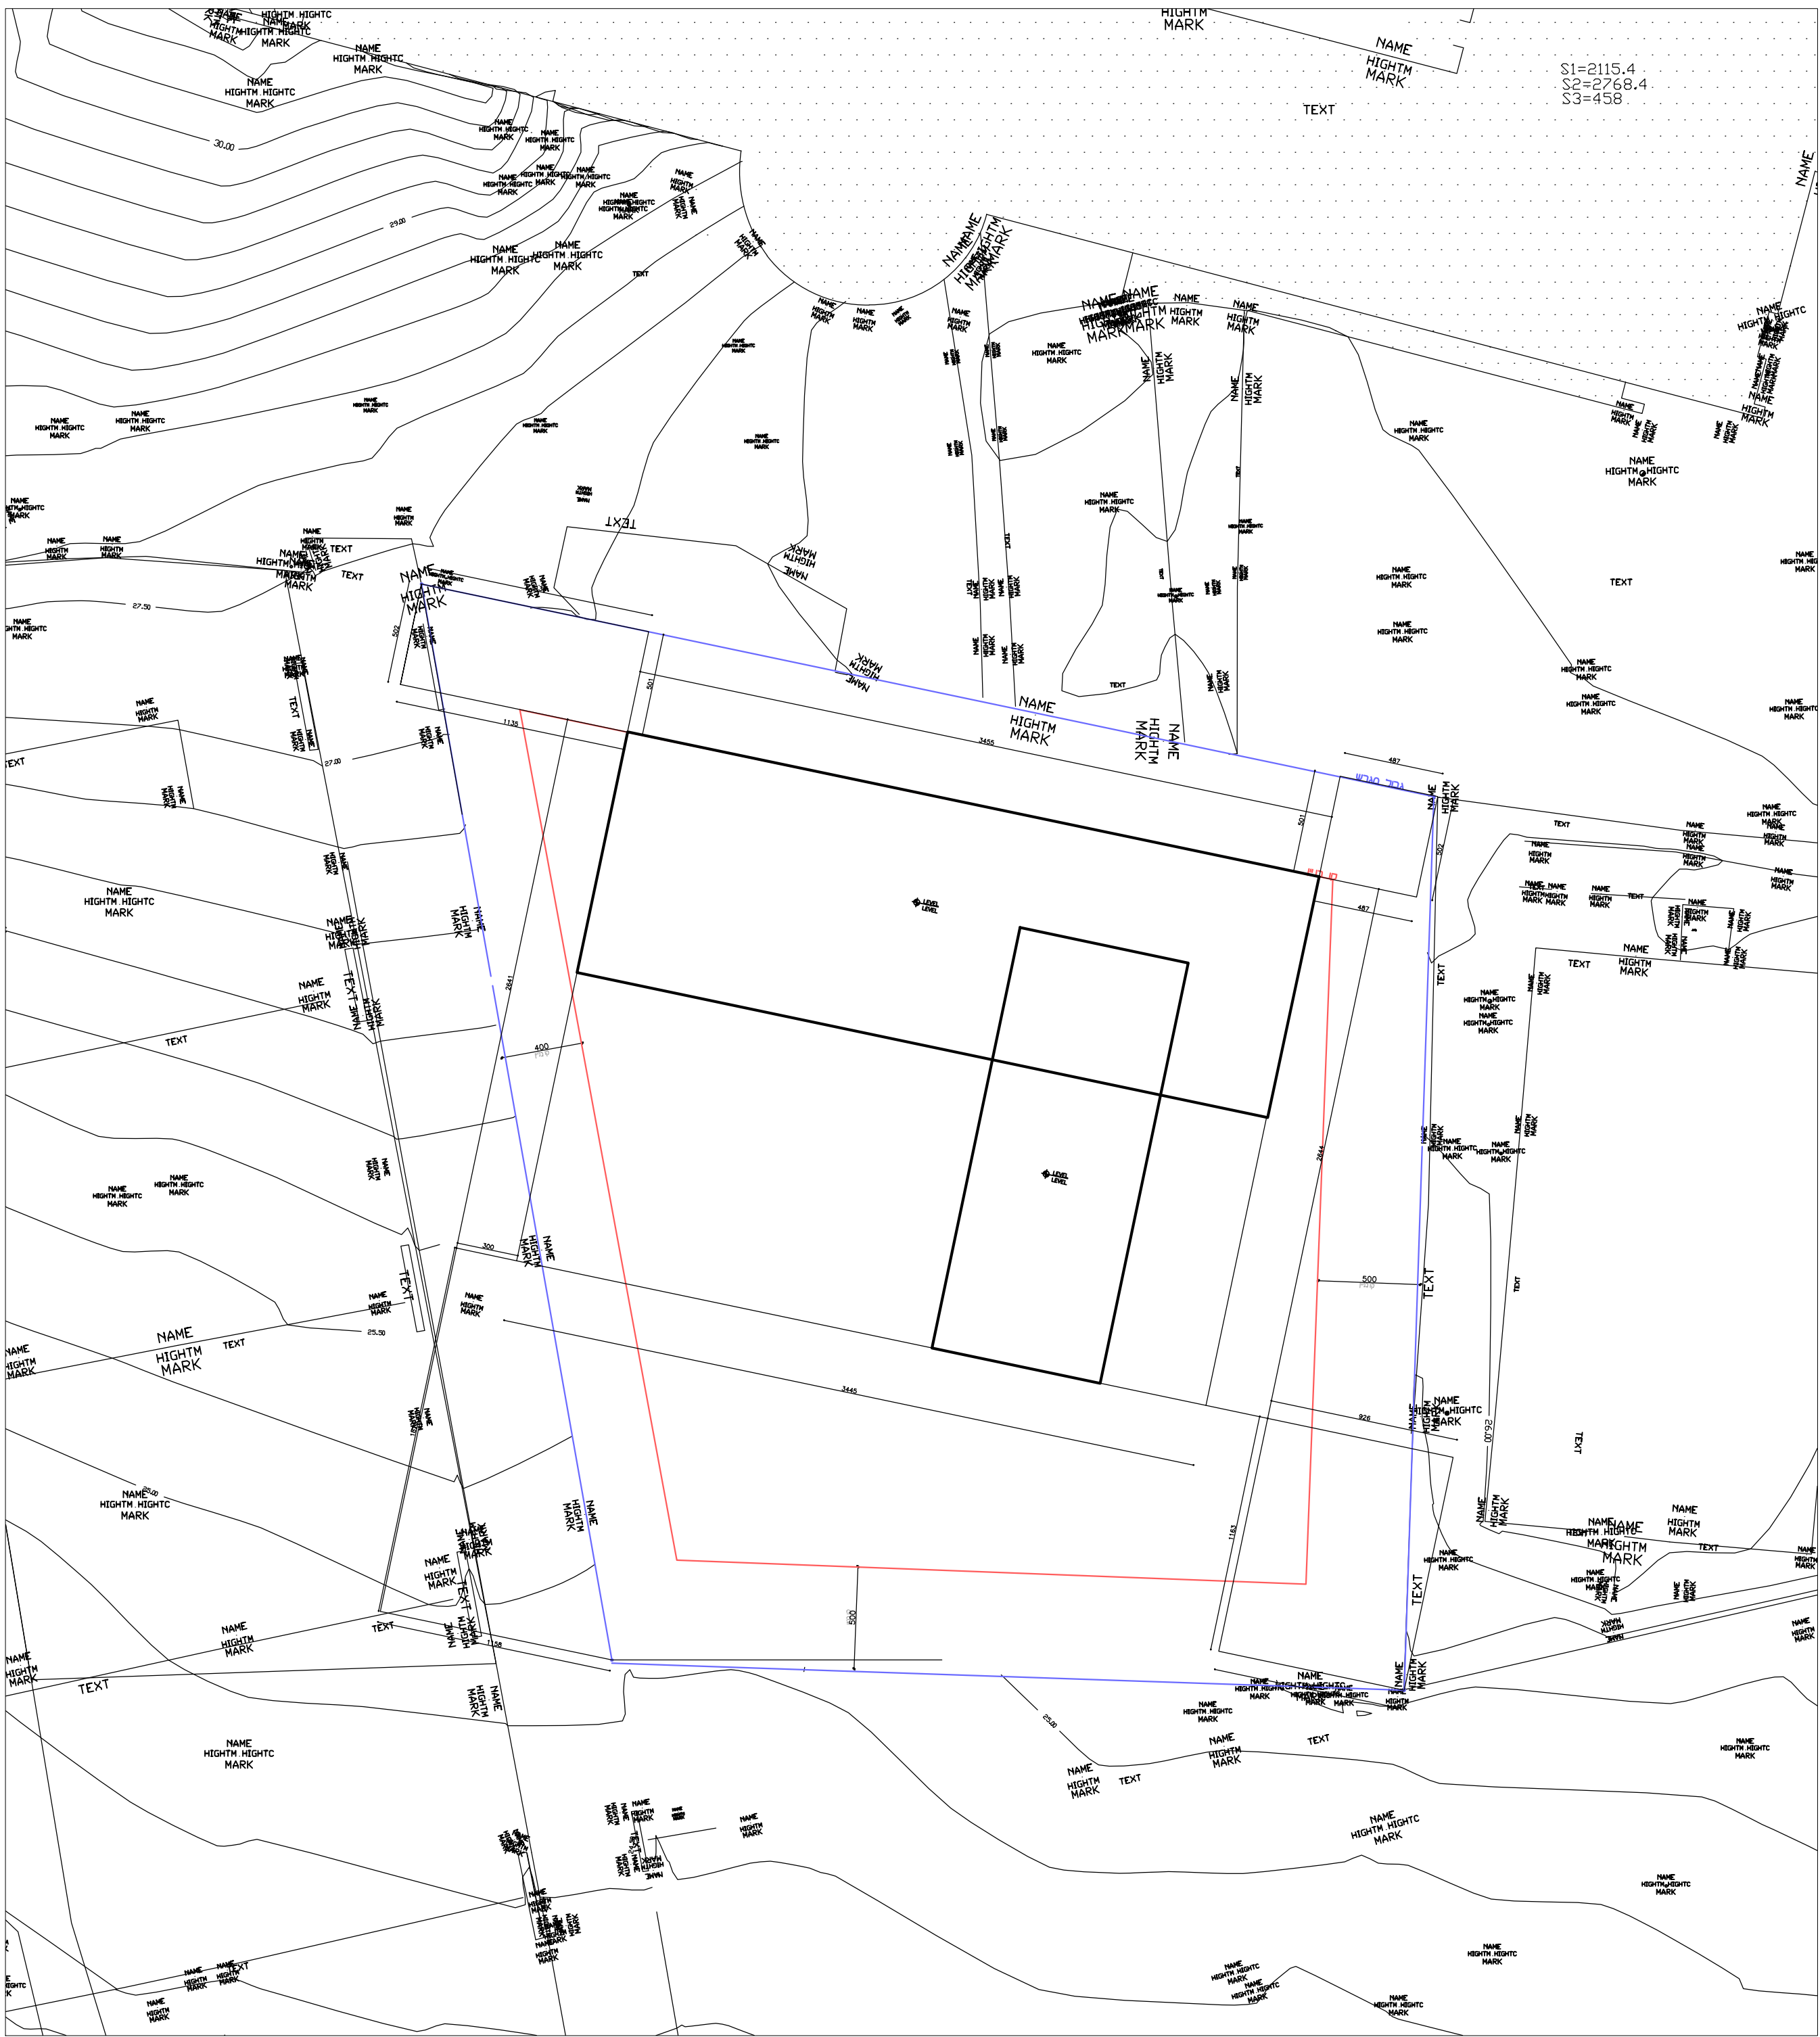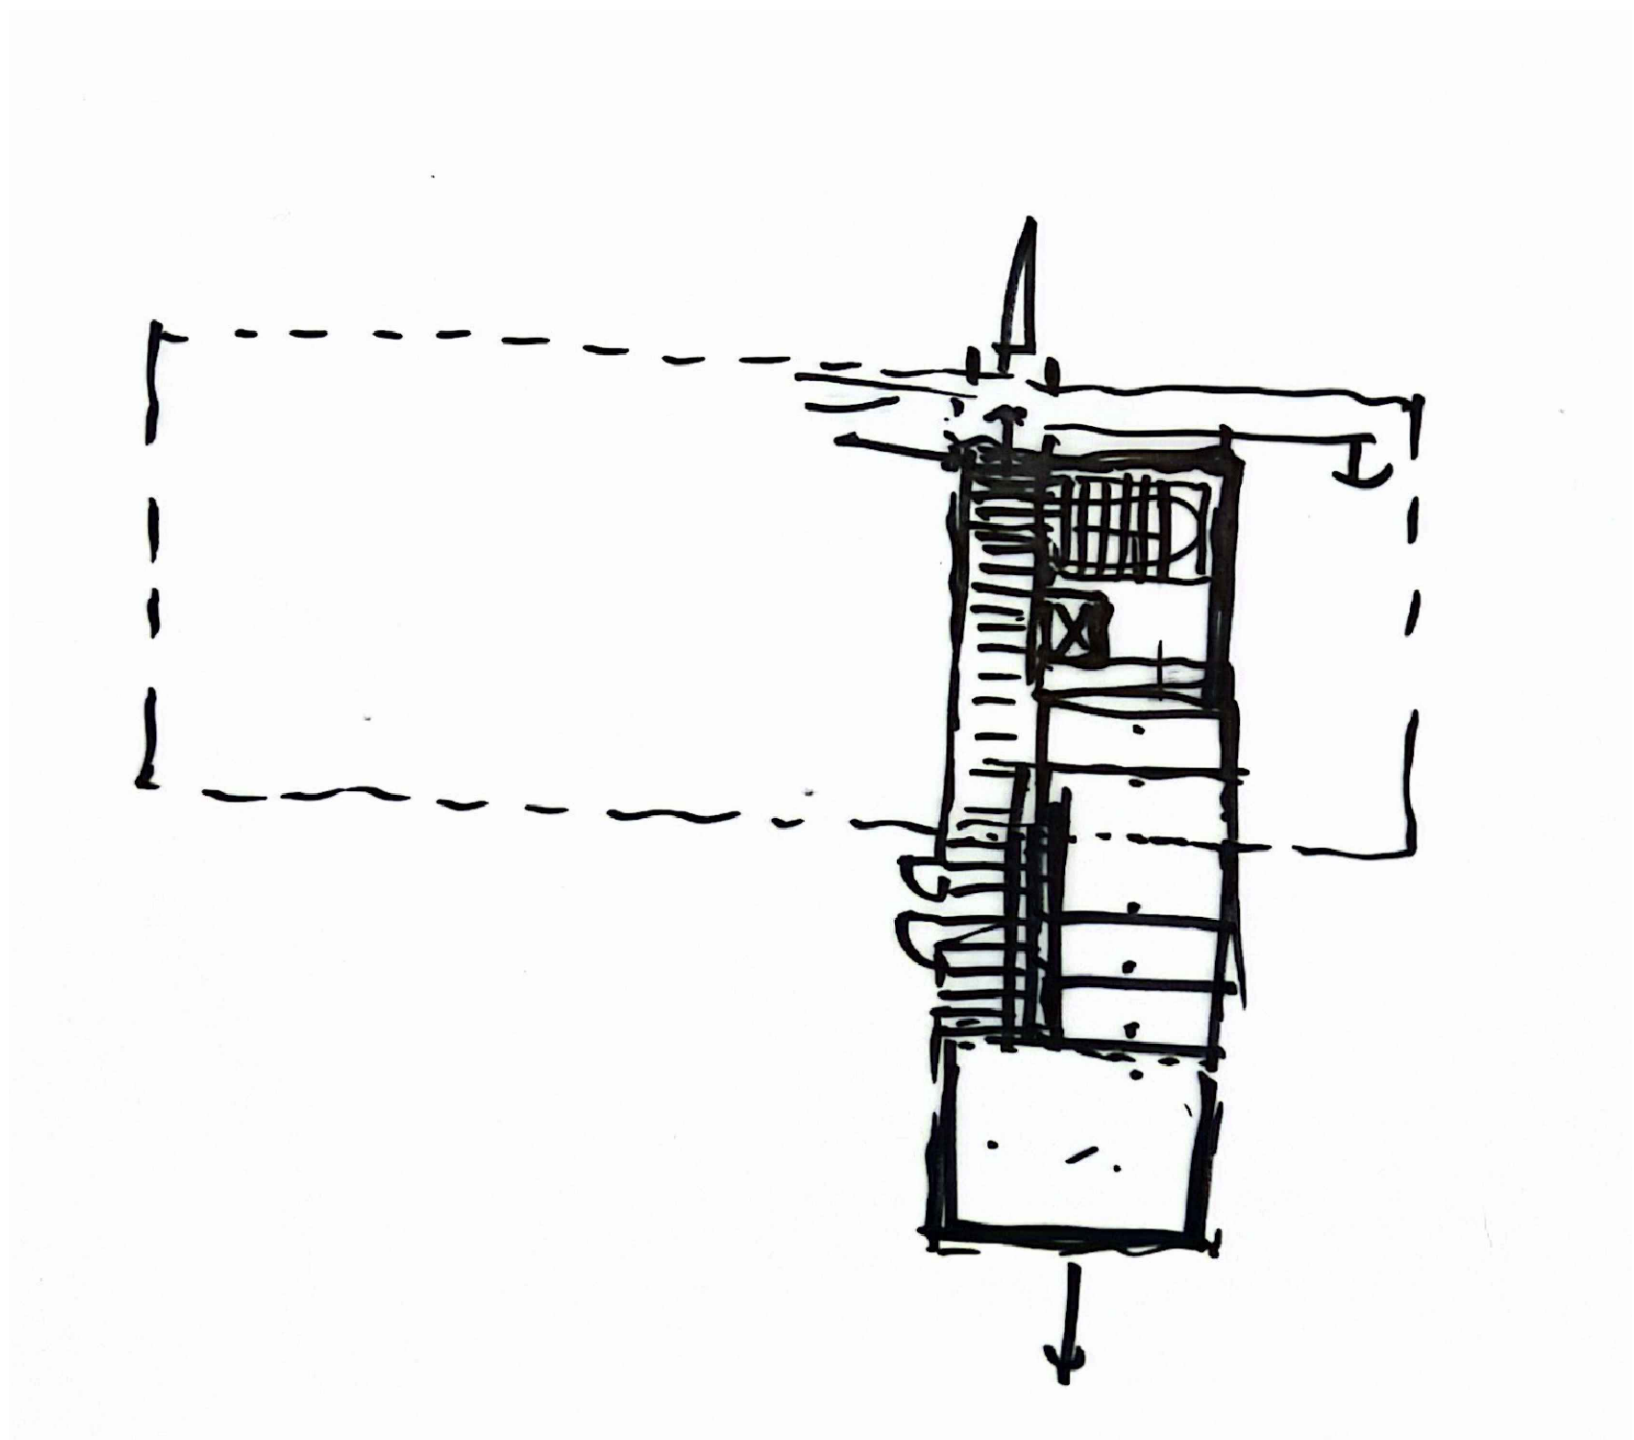

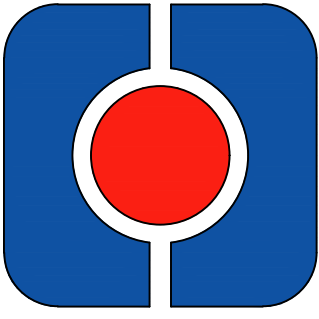

המכללה
הטכנווגית
רופין

מגמת אדריכלות
מחזור ס'
ב'

שם הקורס:
תכנון אדריכלי

פרוייקט מעונות
סטודנטים

מס גיריון:
3/8

קנ"מ:
1-100




נושא גיריון:
תכנית קרקע

שם המנחה:
נעמה שבתאי ציזר

תאריך:
18.9.24

מגישה:
כרמל סעדון

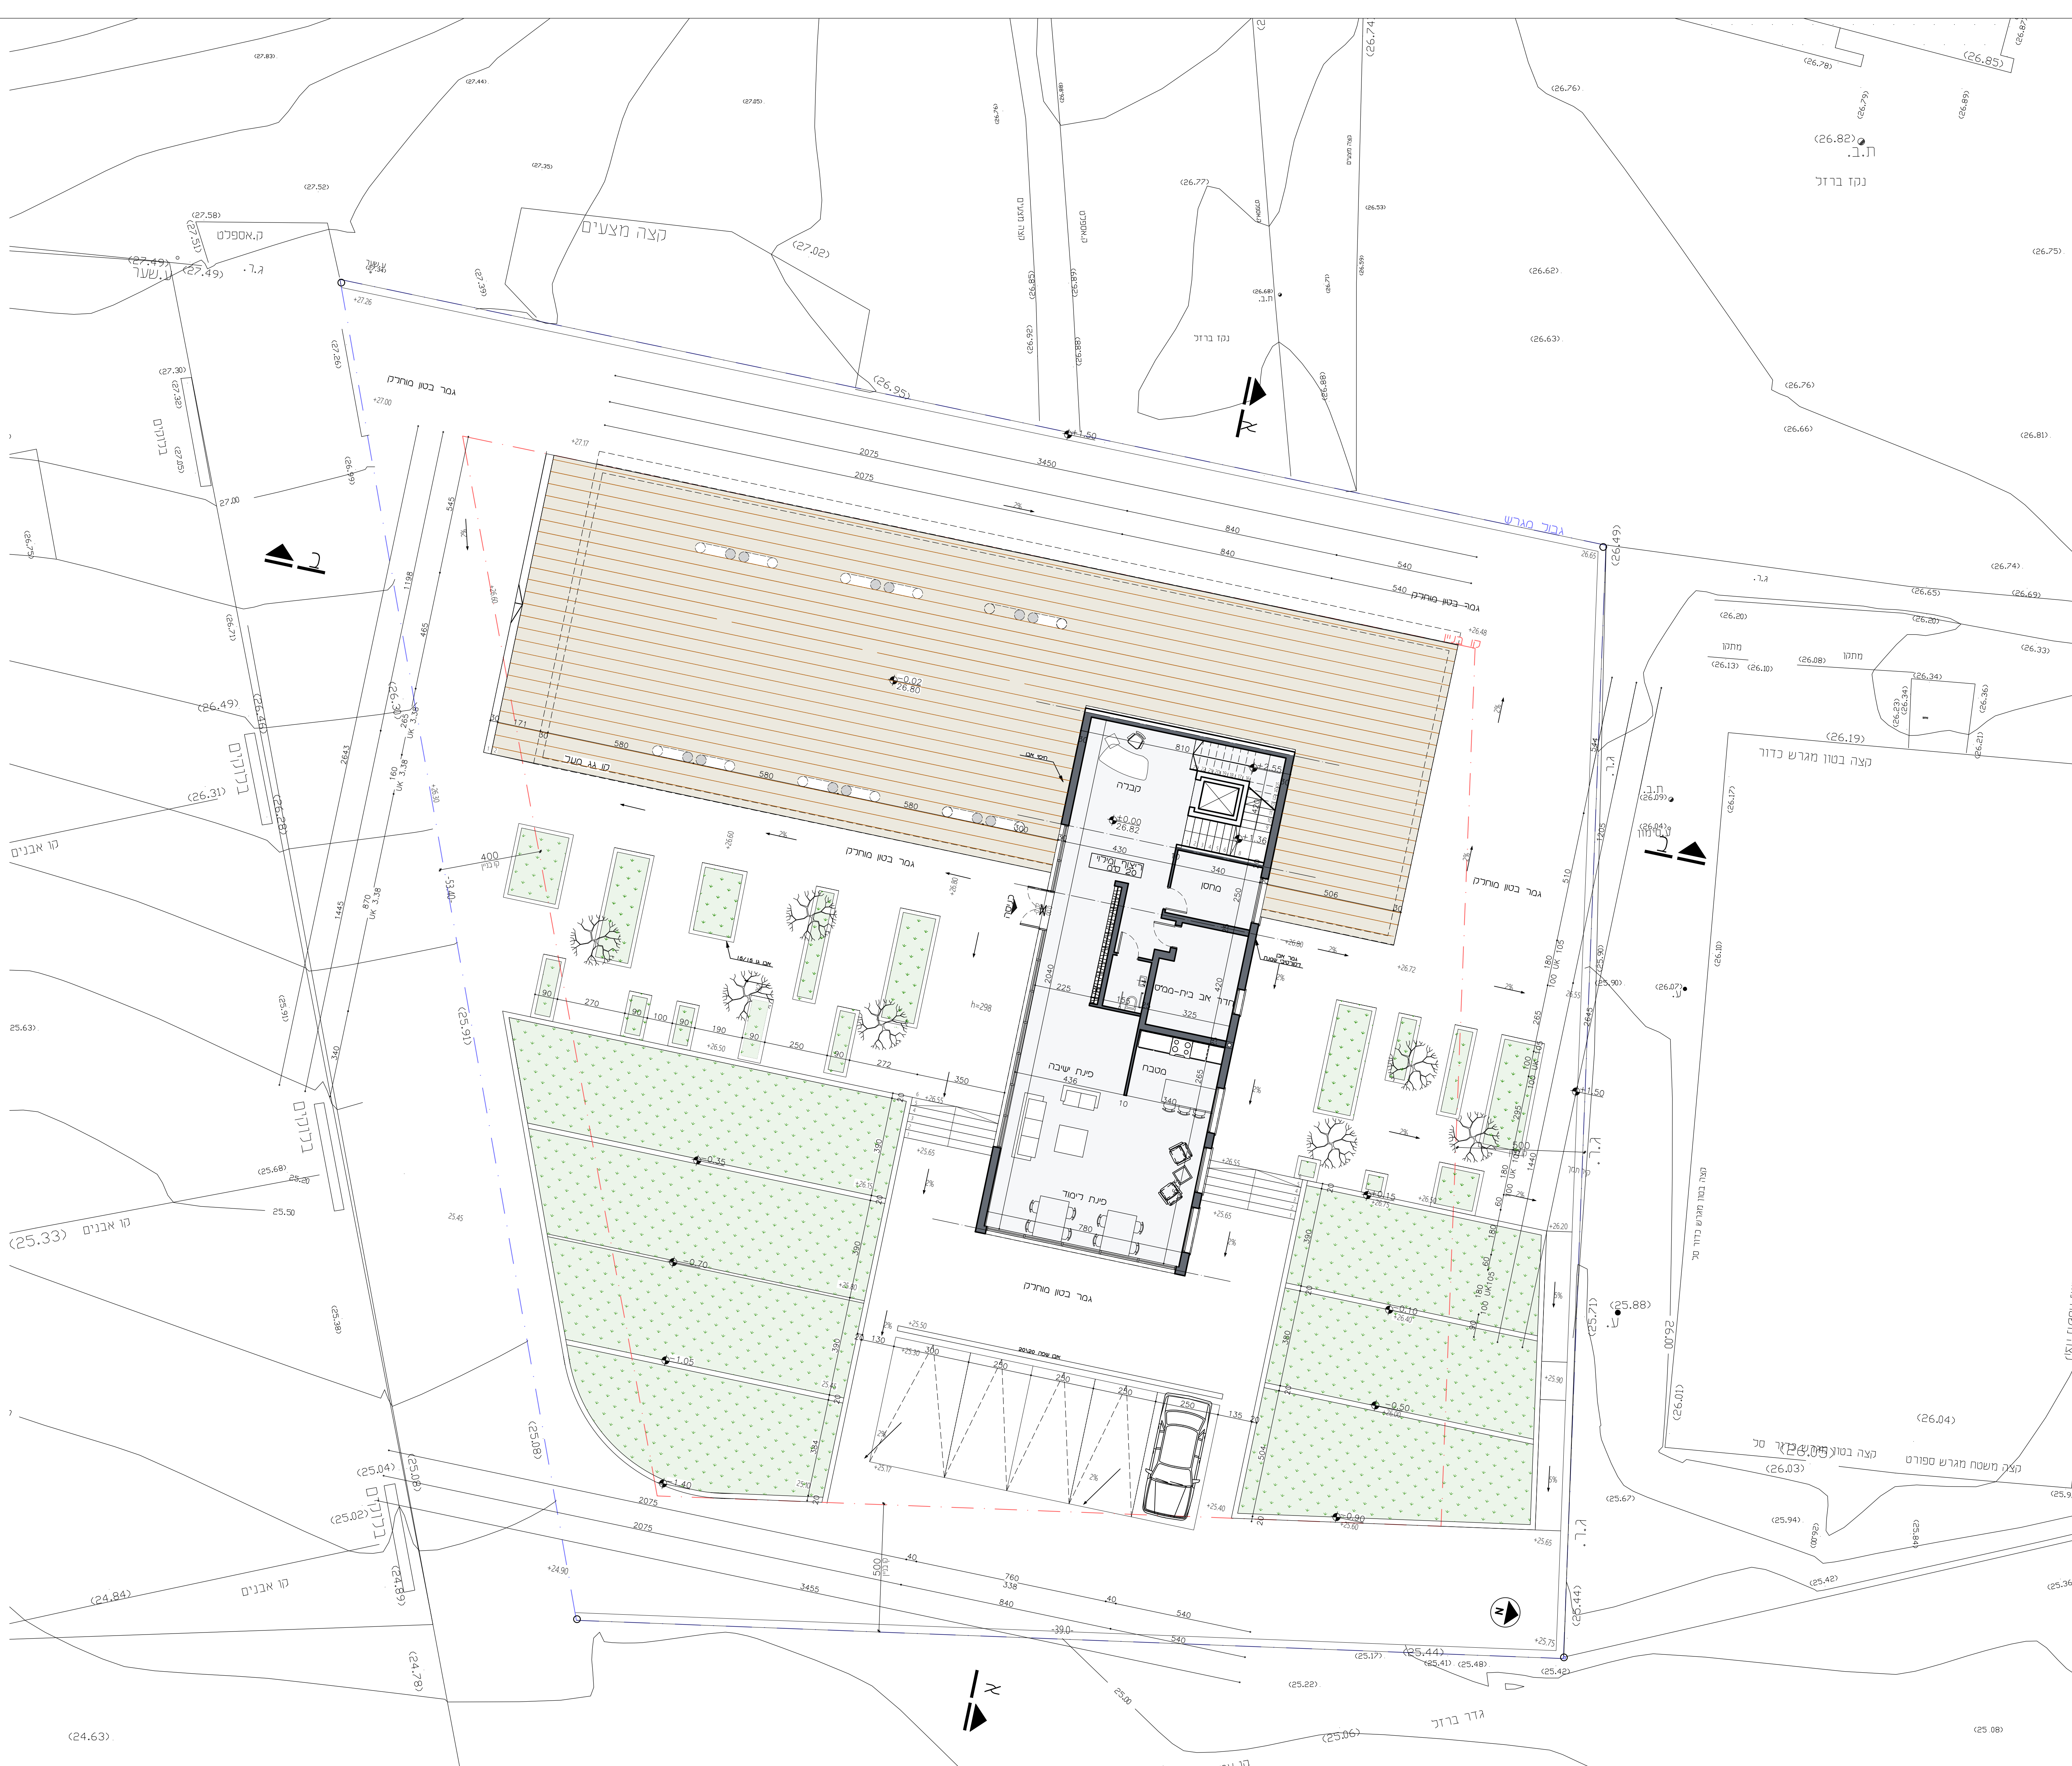

מגמת אדריכלות
מחזור ס'
ב'

שם הקורס:
תכנון אדריכלי

פרוייקט מעונות
סטודנטים

מס גיליון:
4/8

קנ"מ:
1-100




נושא גיליון:
תכנית קומה א


שם המנחה:
נעמה שבתאי ציזר

תאריך:
18.9.24

מגישה:
כרמל סעדון

תכנית קומה א

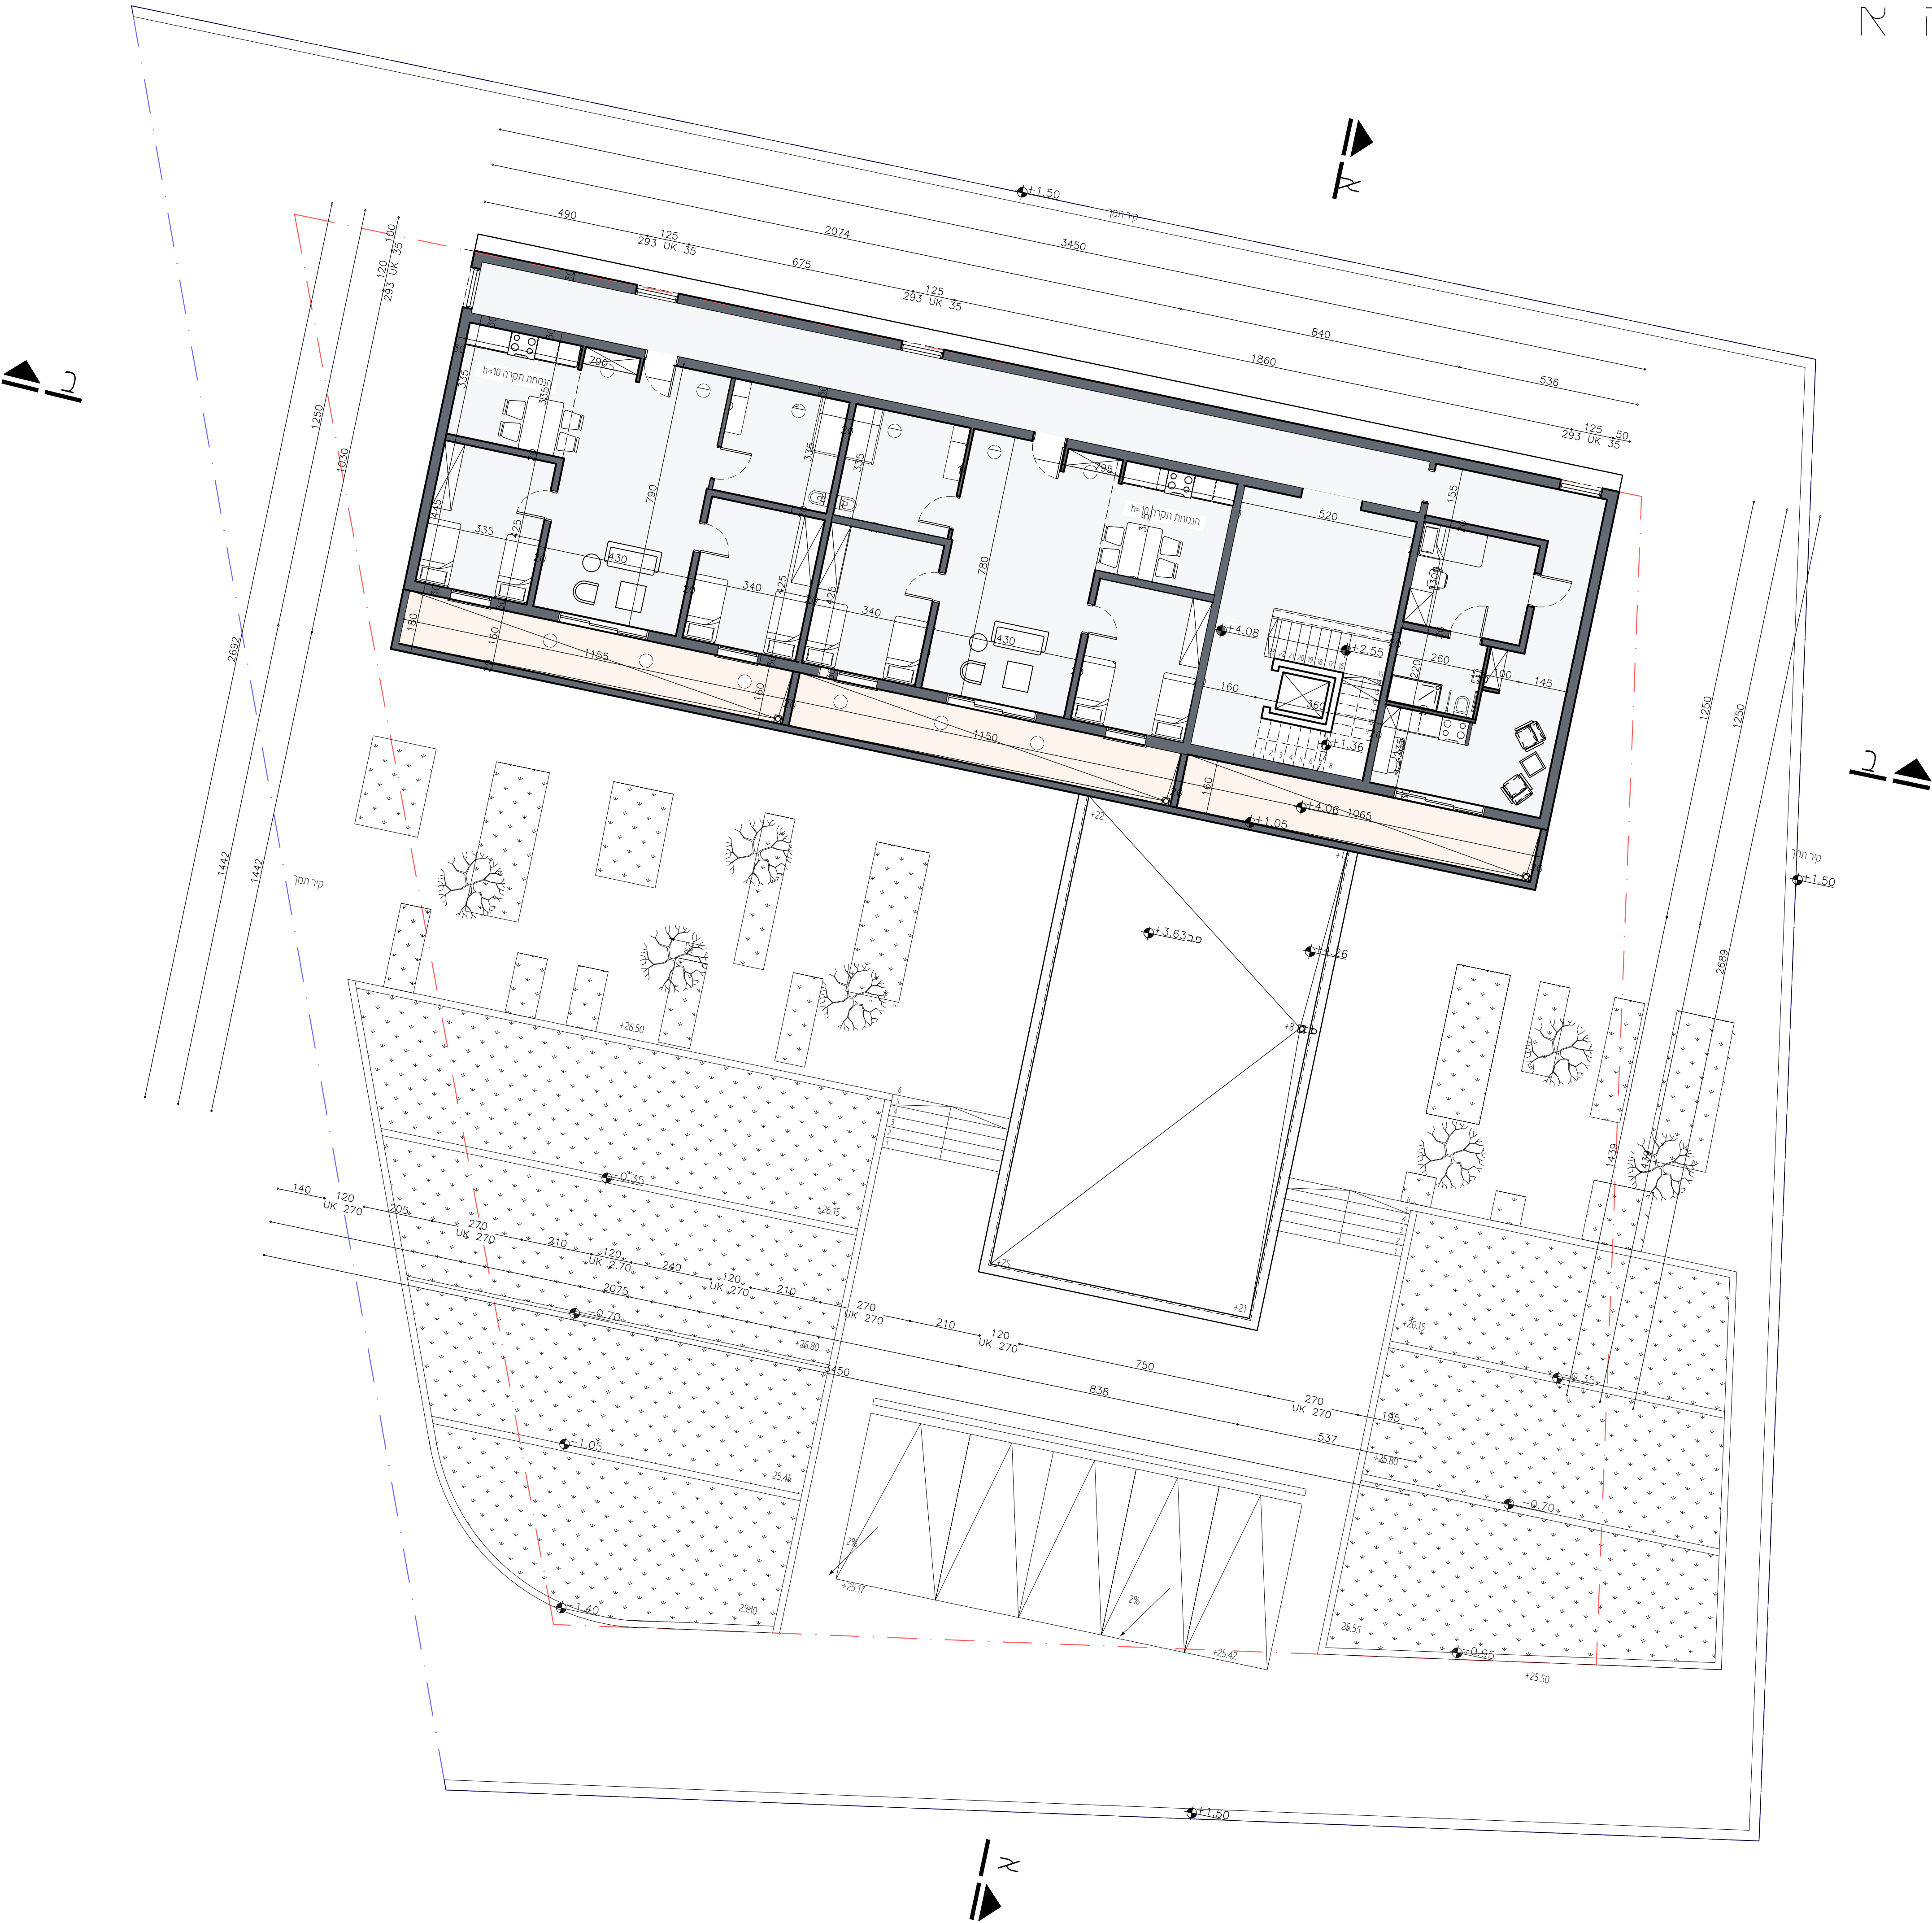

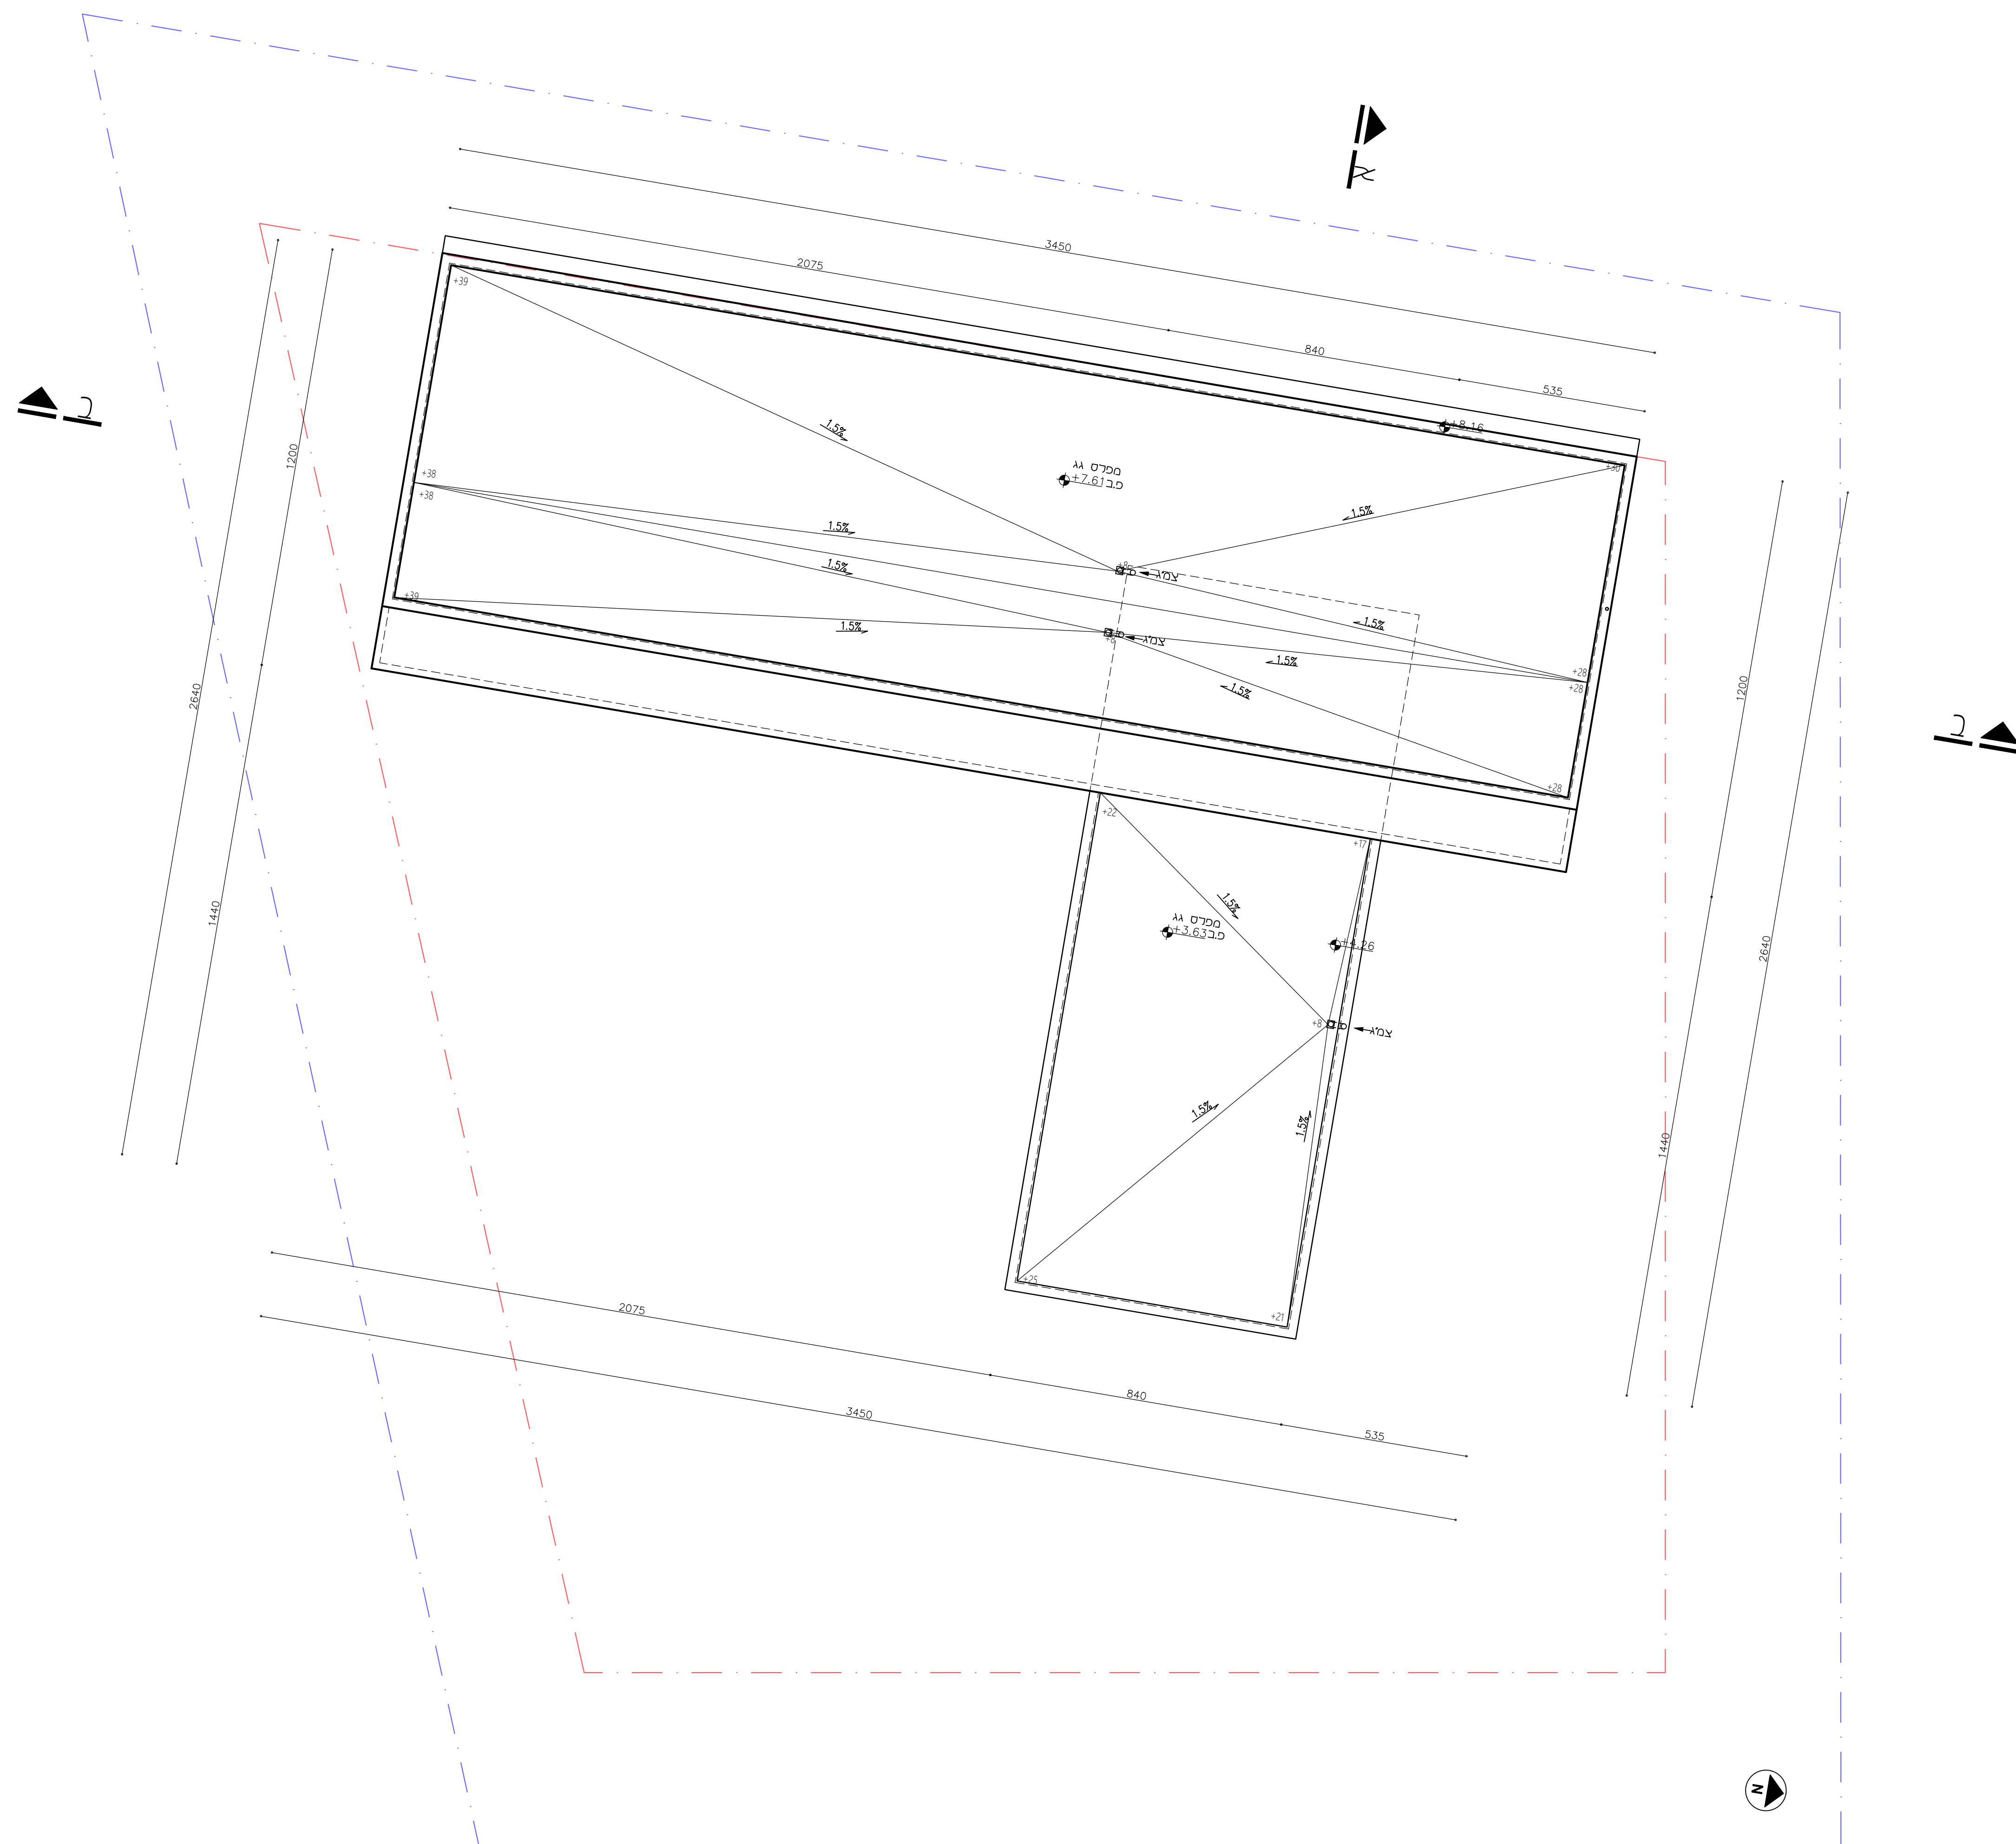

מגמת אדריכלות
מחזור ס'
ב'

שם הקורס:
תכנון אדריכלי

פרוייקט מעונות
סטודנטים

מס גיליון:
6/8

קנ"מ:
1 – 100








נושא גיליון:
חתכים

שם המנחה:
נעמה שבתאי ציזר

תאריך:
18.9.24

מגישה:
כרמל סעדון

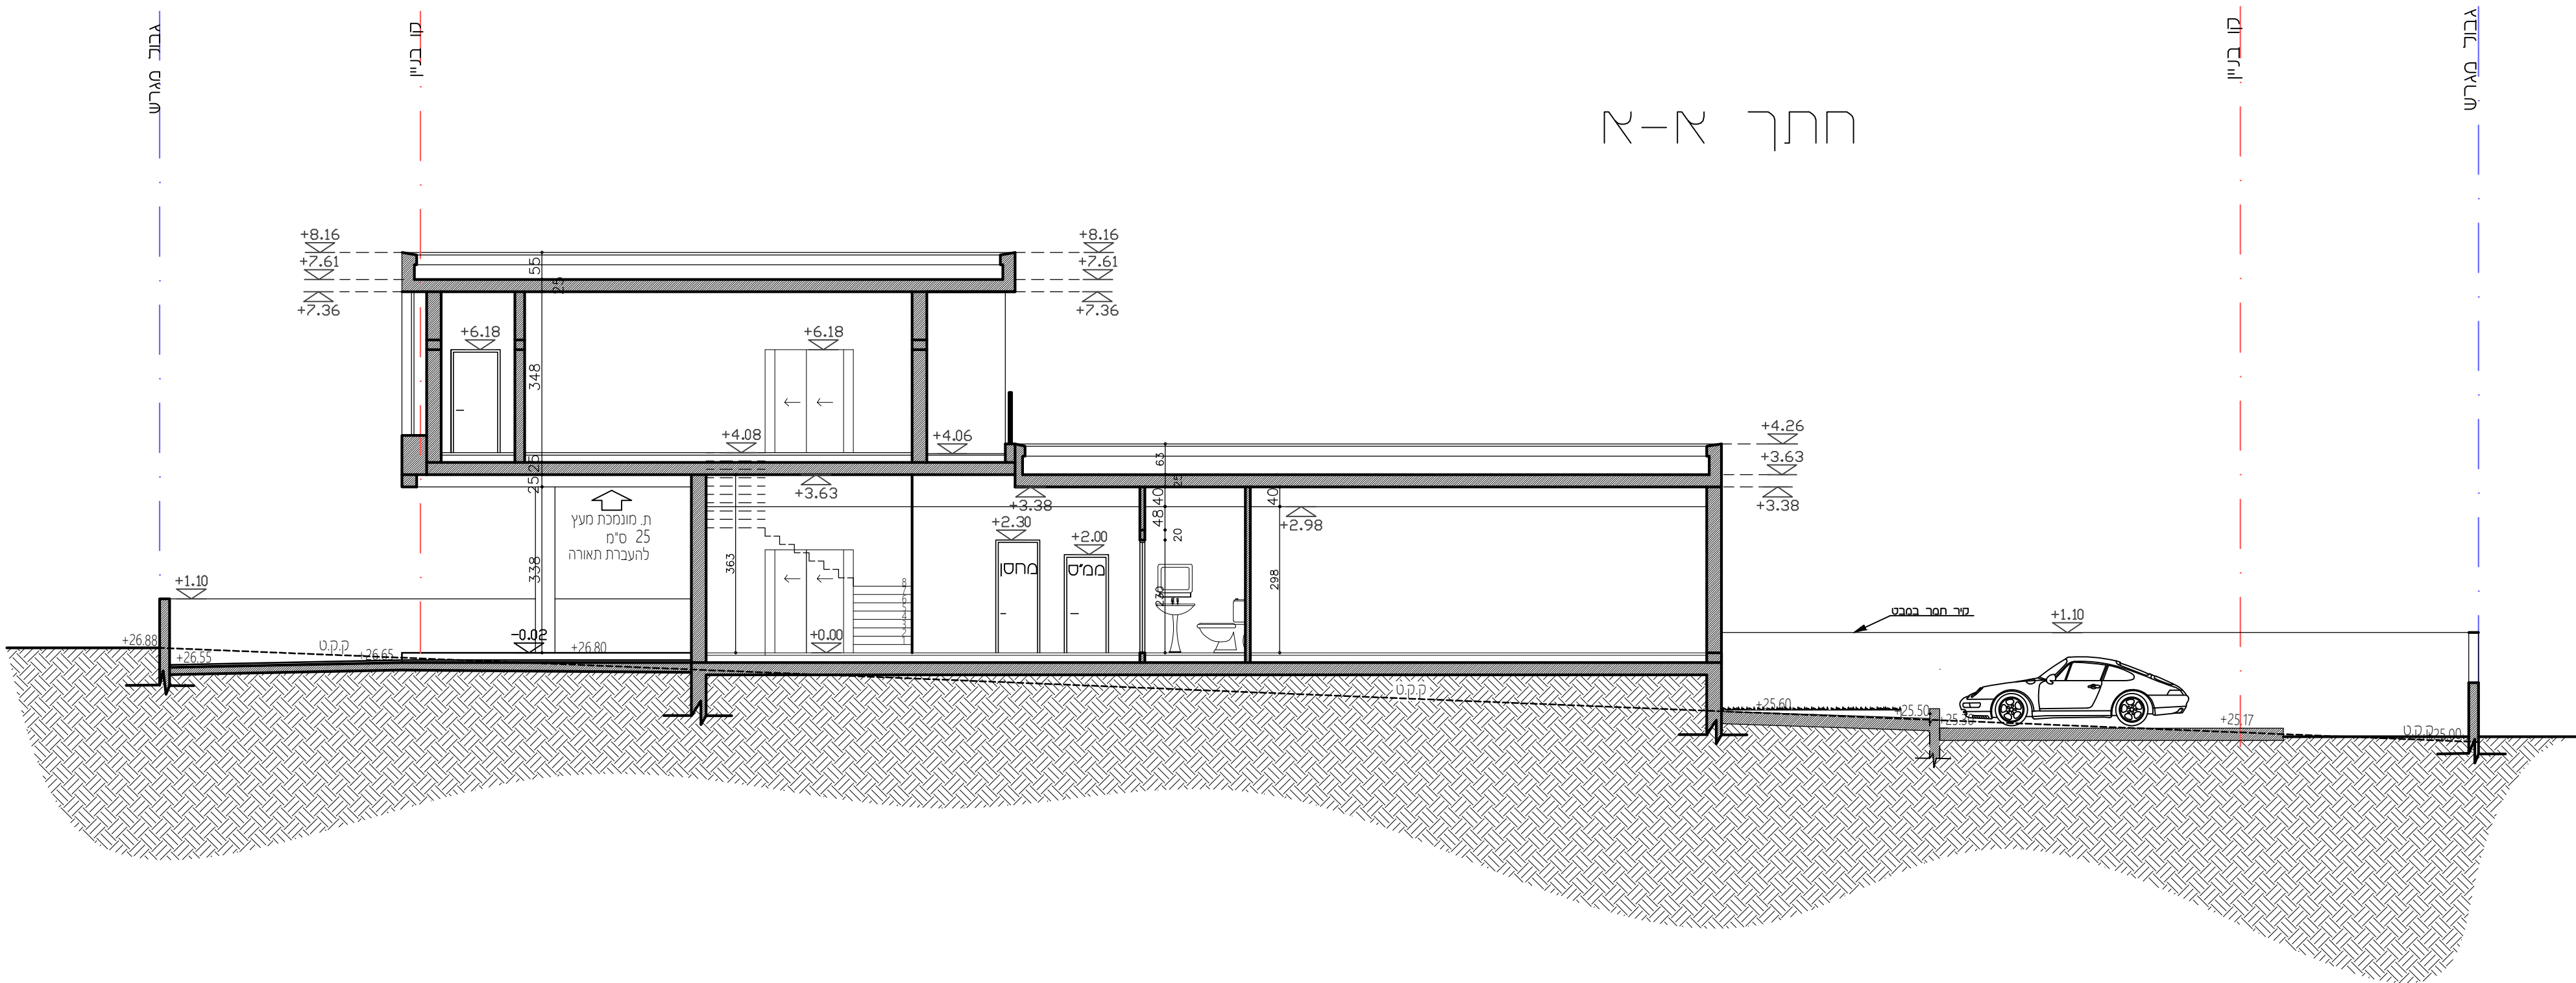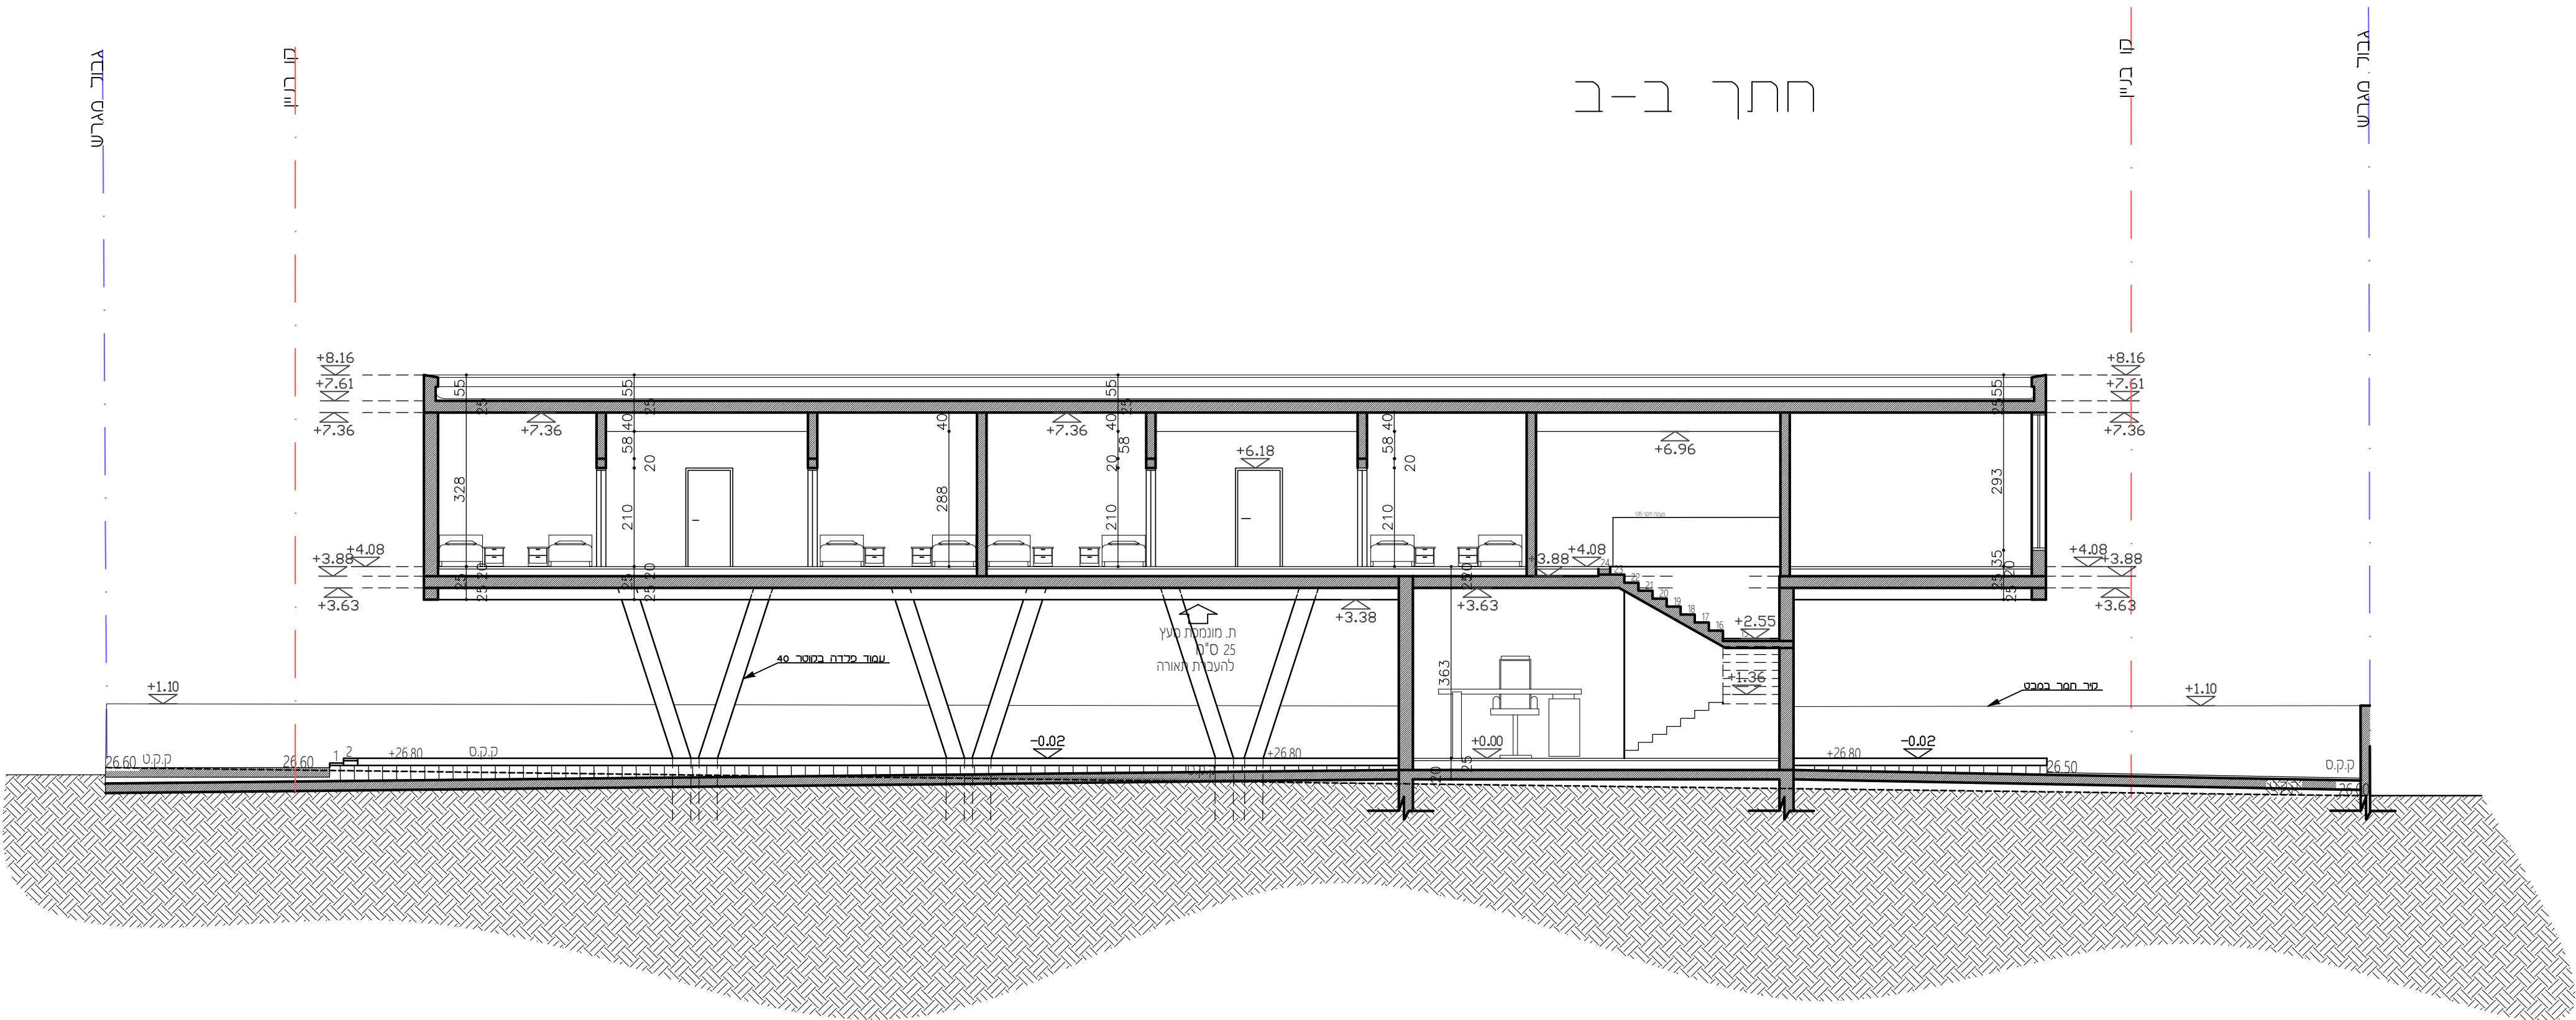

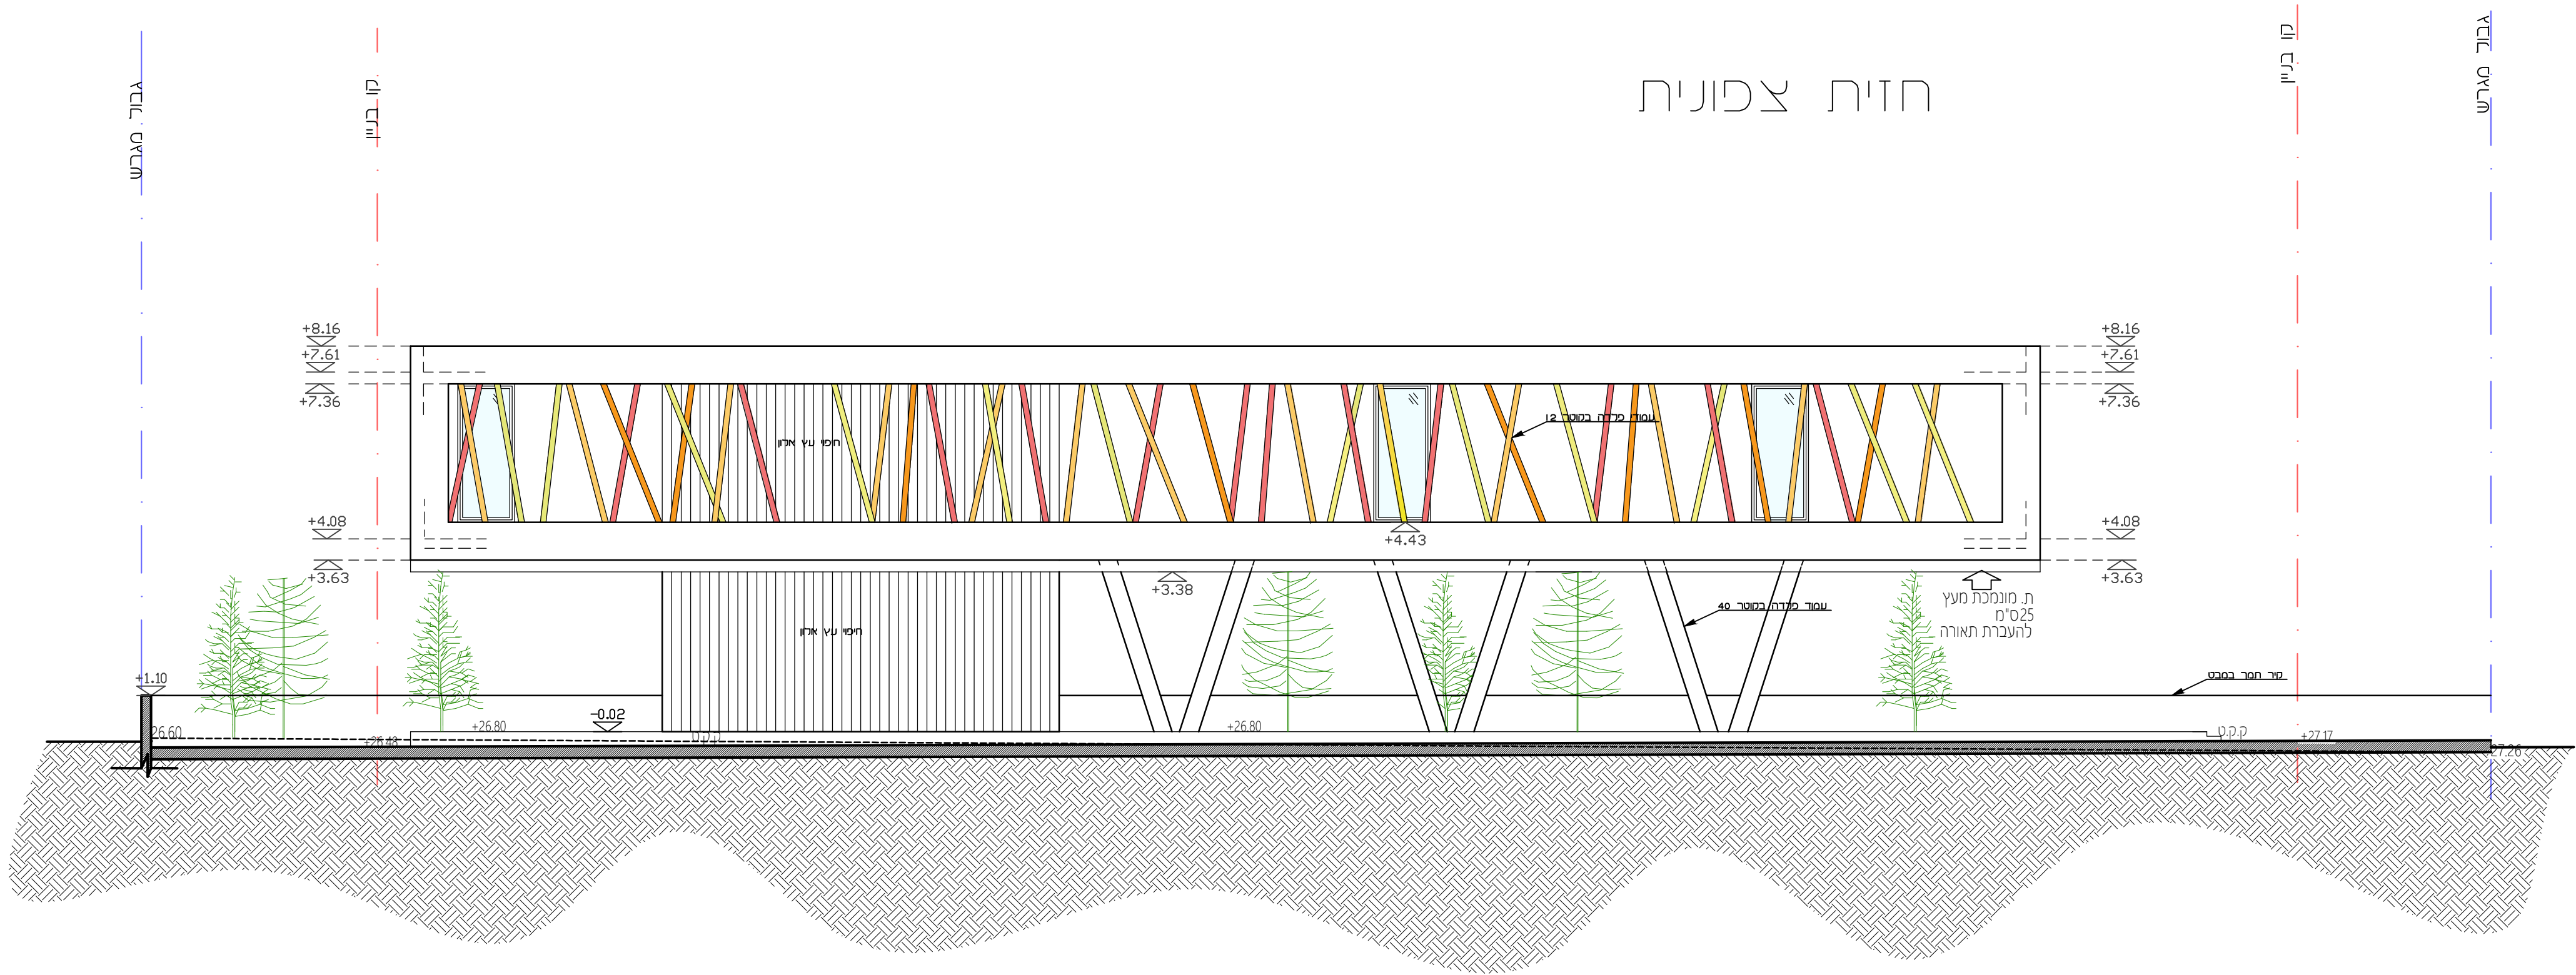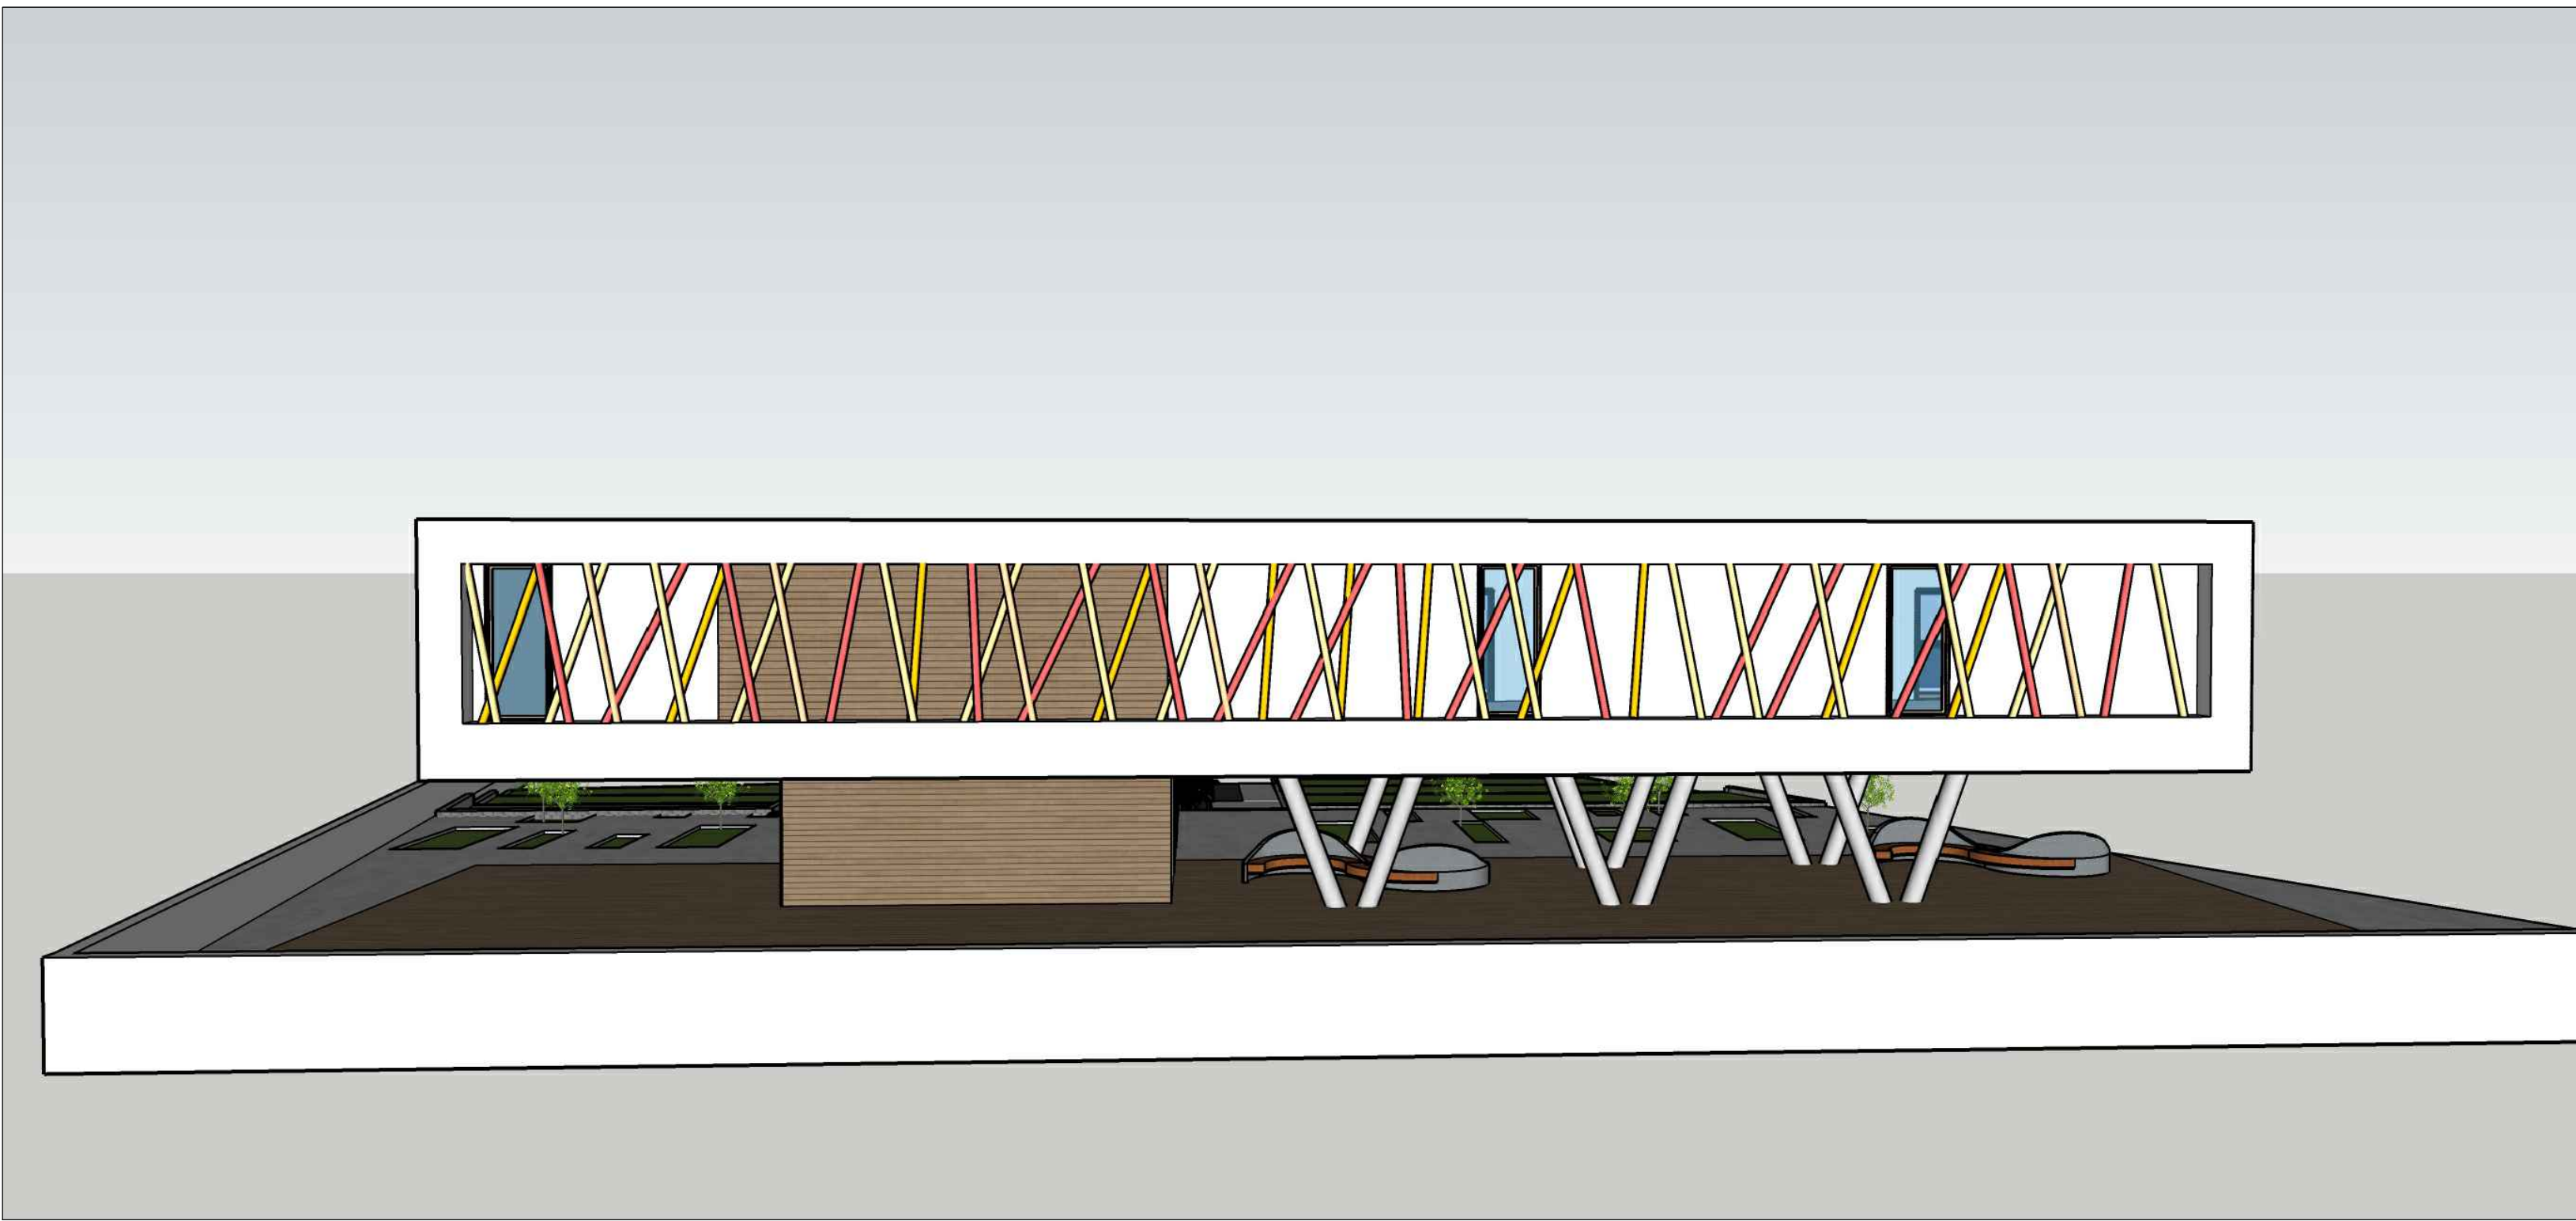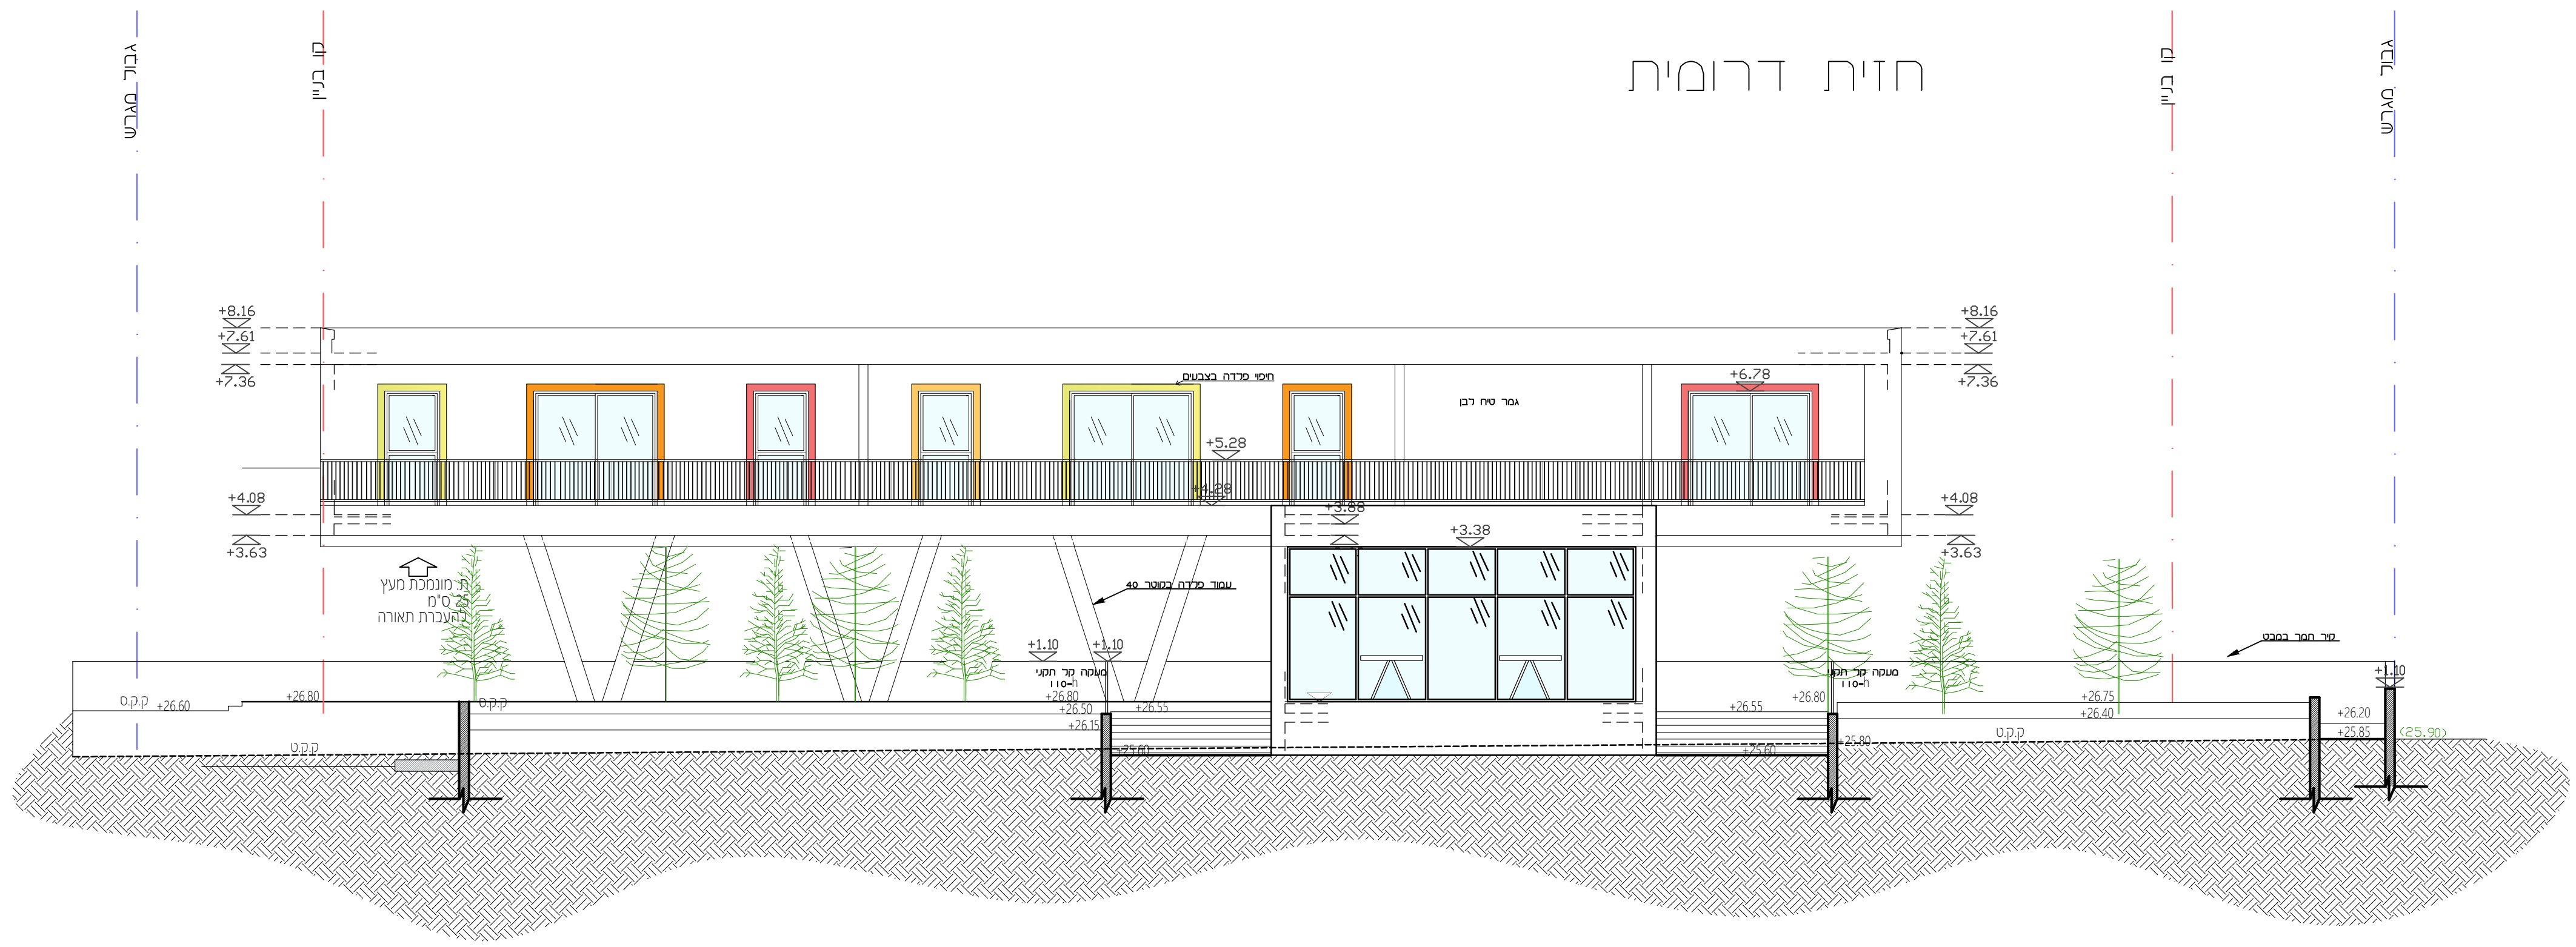

מגמת אדריכלות
מחזור ס'
ב'

שם הקורס:
תכנון אדריכלי

פרויקט מעונות
סטודנטים

מס גיליון:
8/8

קנ"מ:
1-100




נושא גיליון:
חזיתות

שם המנחה:
נעמה שבתאי ציזר

תאריך:
18.9.24

מגישה:
כרמל סעדון

חזית מזרחית

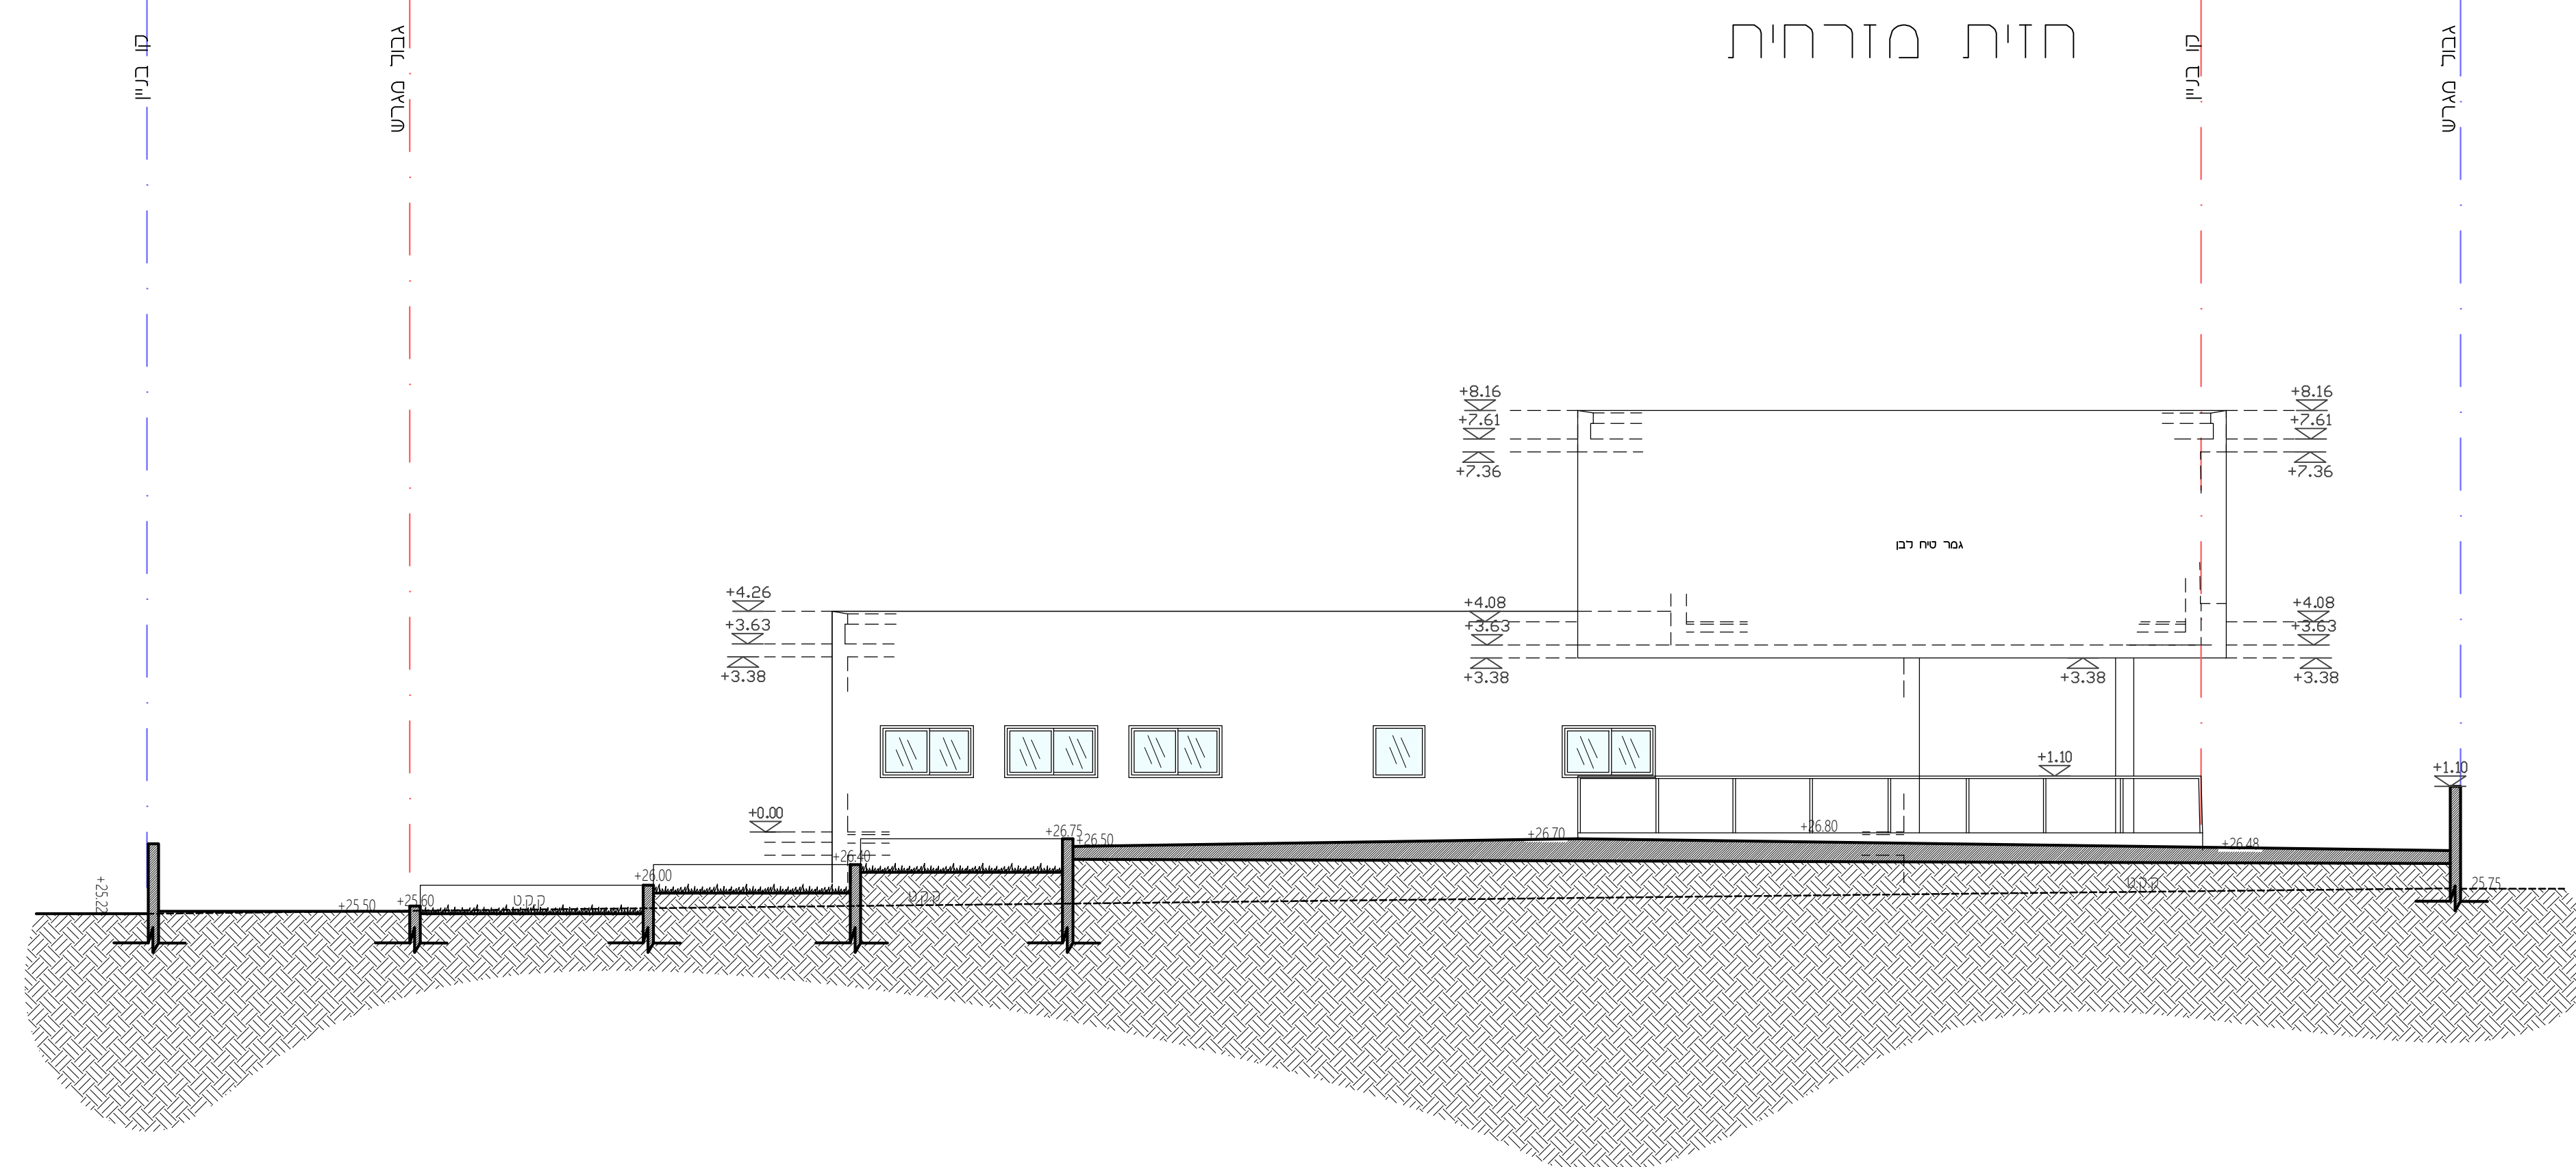

חזית מערבית

