


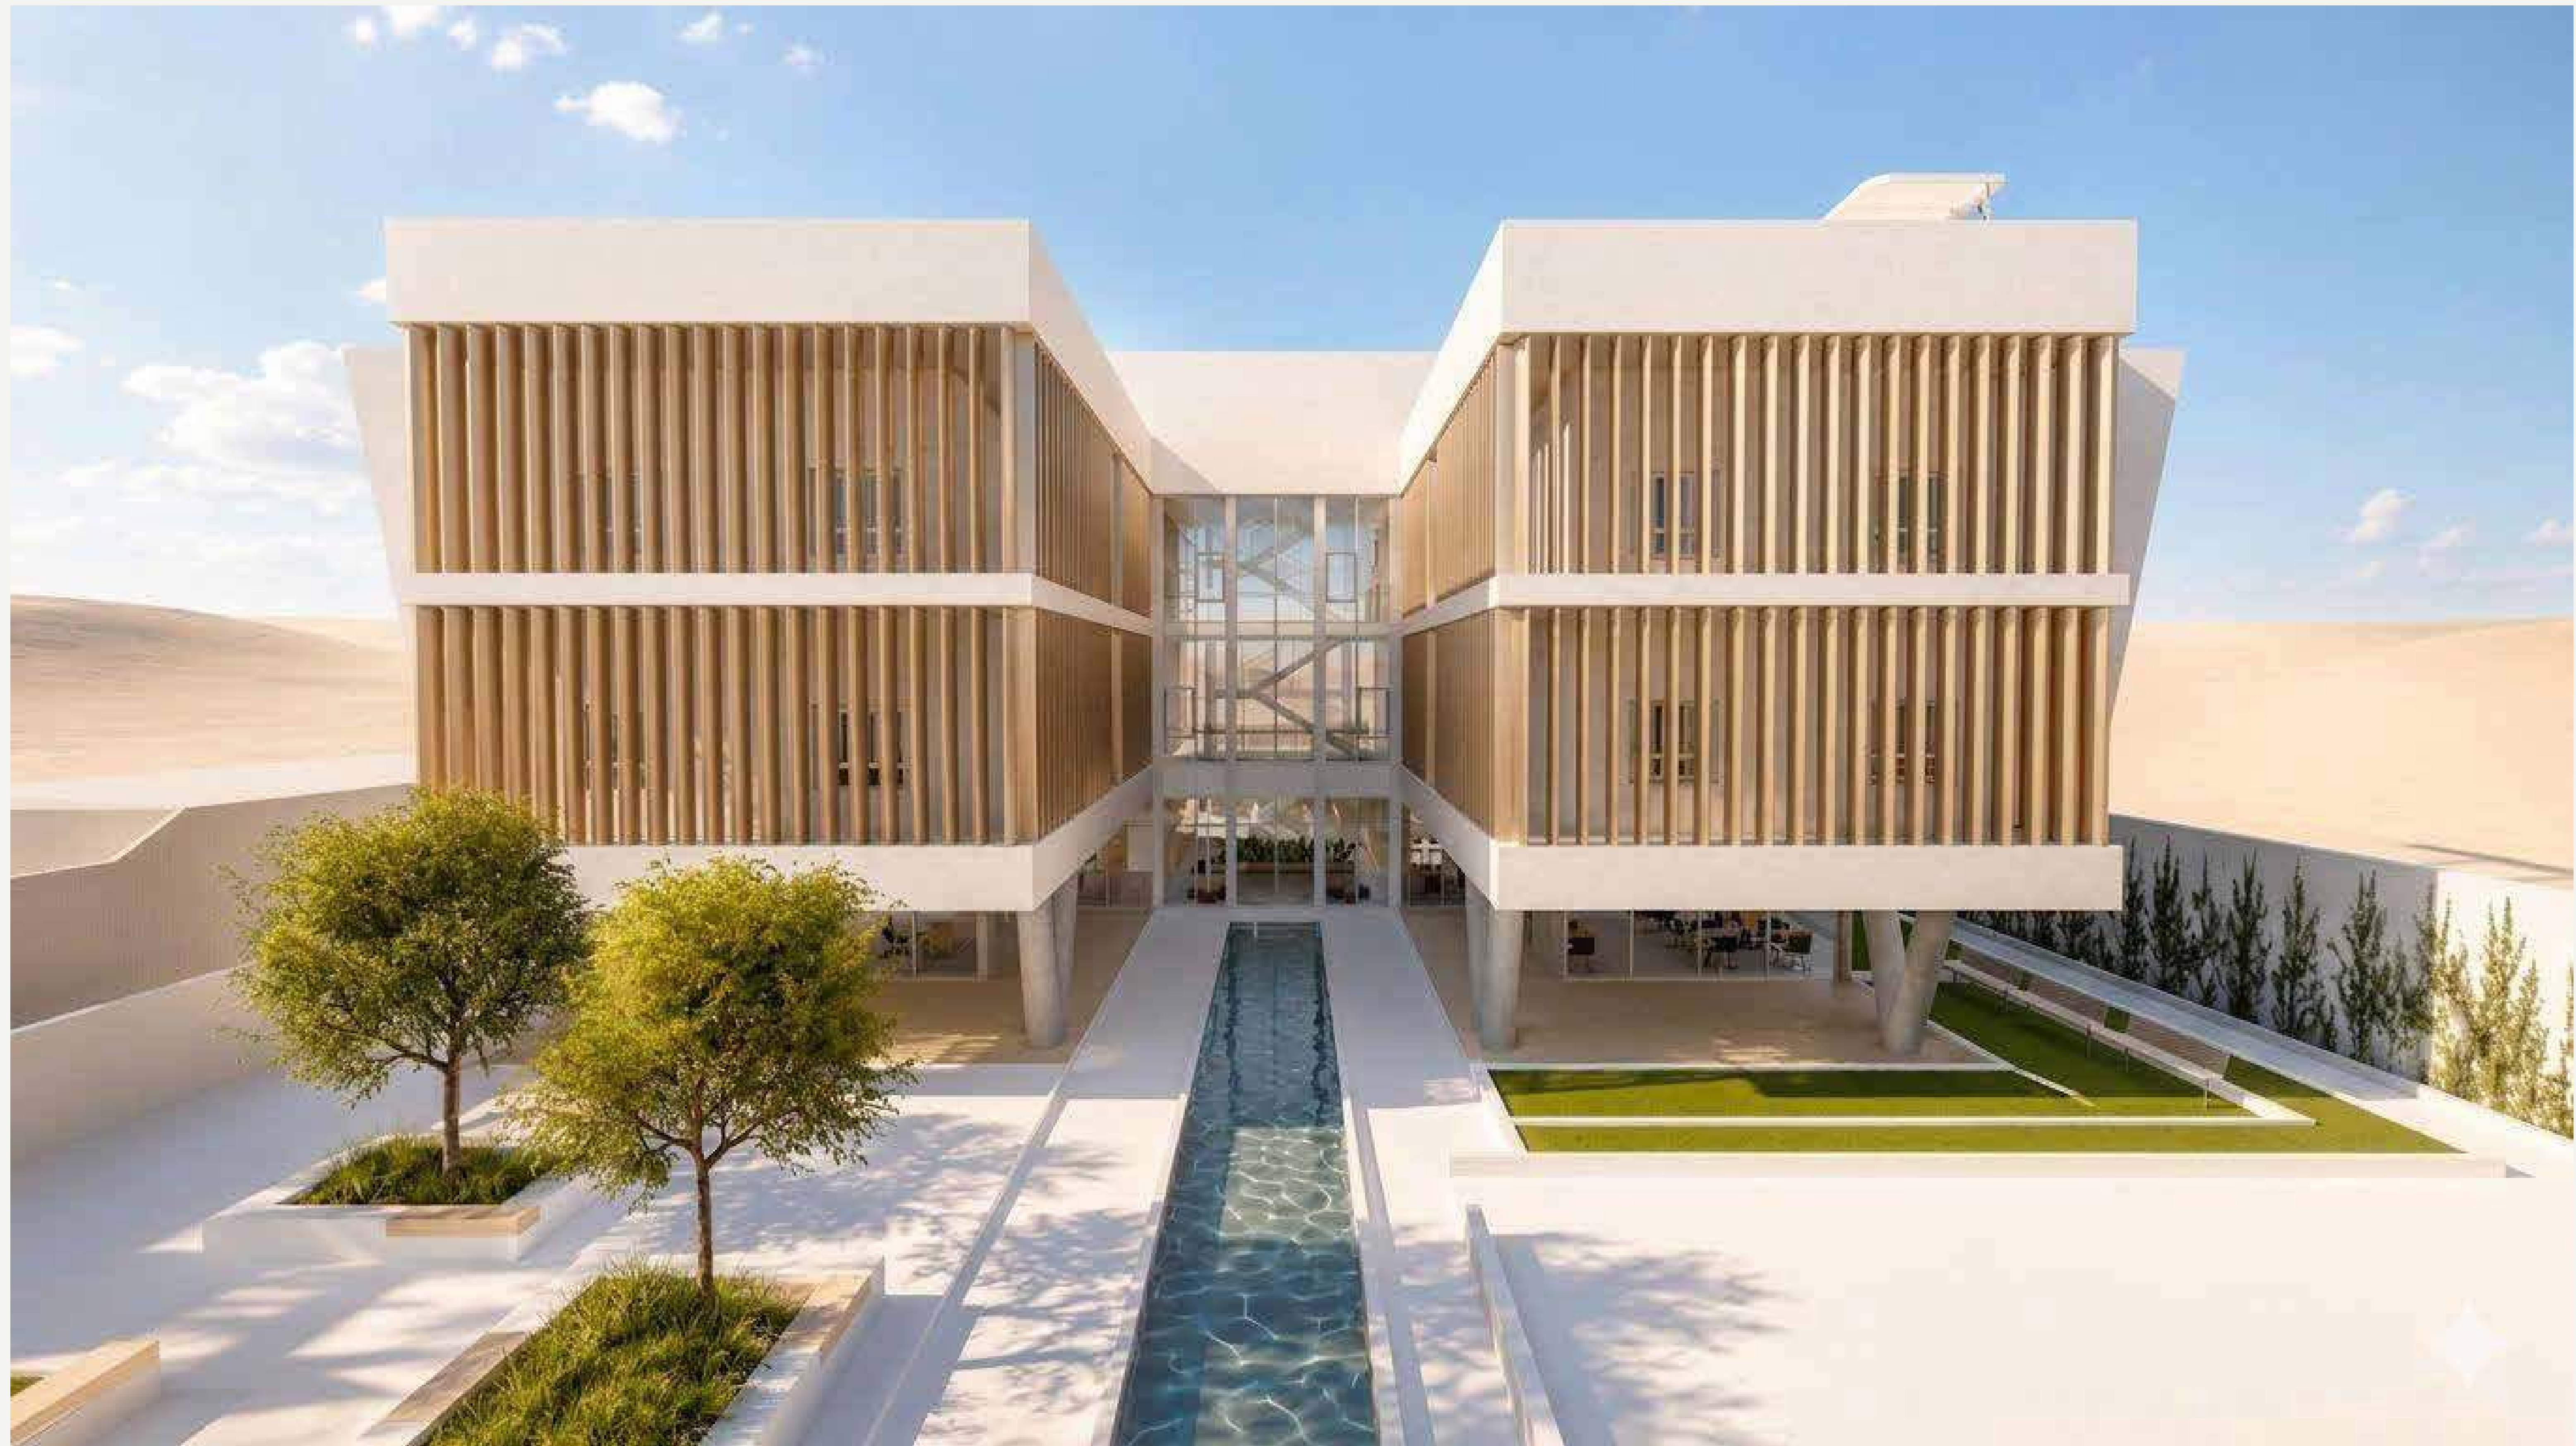



מס'	תיאור גיליון:	קו"מ:
-00	שער	
-01	ניתוח סביבה	
-02	סקיצות פרוגרמה	
-03	הדמיות	

פיתוח שטח		
1:100	תכנית קומת קרקע	-04
1:100	תכנית קומה א	-05

תכנית שחור לכן		
1:100	תכנית קומת קרקע	-06
1:100	תכנית קומה א	-07
1:100	תכנית קומה ב	-08
1:100	תכנית גגות	-09
1:100	חתיכים	-10
1:100	חזיתות	-11
1:100	חזיתות	-12

תכנית עבודה		
1:50	תכנית עבודה קומה א	-13
1:50	חתך א'-א', ב'-ב'	-14
1:50	חזית צפונית, מערבית	-15

1:5	1:20	1:20	מדגמות תכניות פרטים	-16
	1:20		מדגמות חתיכים	-17
	1:20		קיר ייחודי-חתיכים	-18
	1:5		קיר ייחודי-פרטים	-19

עיצוב פנים				
1:50			תכנית ריהוט, רציף	-20
1:50			תכנית חקיקה משותפת	-21
1:50			הדמיות ופריסת קיר	-22
1:10	1:20		תכנון דלפק	-23
1:50			עיצוב חדר לדגמא	-24

קונסטרוקציה		
1:100	תכניות קונסטרוקציה	-25

כפר יונה:

היא עיר בשרון,סמוך לנתניה, השייכת למחוז מרכז.
היא הוקמה בשנת1932כמושבה חקלאית ,
במשך השנים הפכה מכפר קטן לעיר מתפתחת, תוך שמירה על אופייה הכפרי והירוק.
בשנת2014הוכרזה כעיר באופן רשמי .

העיר מתאפיינת בשטחים פתוחים, בתי גידול טבעיים ושטחי חקלאות,
שמהווים כ70%משטחה הכולל .
השילוב בין הפיתוח עירוני לבין הצביון הטבעי
מרחב ייחודי המאפשר לתושבים להנות מסביבה ירוקה ושלווה לצד נגישות עירונית מלאה.



המגרש:

המגרש ממוקם בכניסה של כפר יונה באזור מרכזי ונגיש.
מצדו הדרומי עובר כביש57-רחוב העצמאות הכולל גישה רגלית אל האתר.
בצדו הצפוני עובר רחוב הגולן, המאפשר דרכו כניסה לרכבים, מעברו השני שוכנים בתים פרטיים.
בצד המזרחי של המגרש מתוכננת הקמה של מרכז מסחרי ומתחם מגורים,
שעתידים ליצור חזית עירונית פעילה.
בחזית המערבית נשקף נוף פתוח,עשיר בצמחיהומרחבים ירוקים-שמעניקים תחושת מרחב וחיבור לסביבה הטבעית.



מבט מהמגרש לרחוב הגולן




מבט מרחוב העצמאות למגרש

נתוני המגרש:

גוש:8147
מס חלקה:102
שטח המגרש:2000מ"ר
קווי בניין:
4מ' קו בניין אחורי
3מ' קו בניין צידי וקדמי

שיפוע המגרש3מ' מצפון לדרום

כמו כן המגרש מאופיין בהפרש גבהים של 33מטרים היוצר אתגר תכנוני .
בשל כך החלטתי ליצור מבנה עם2כניסות במפלסים שונים
שישתלבו עם הפרשי הגבהים של המגרש.

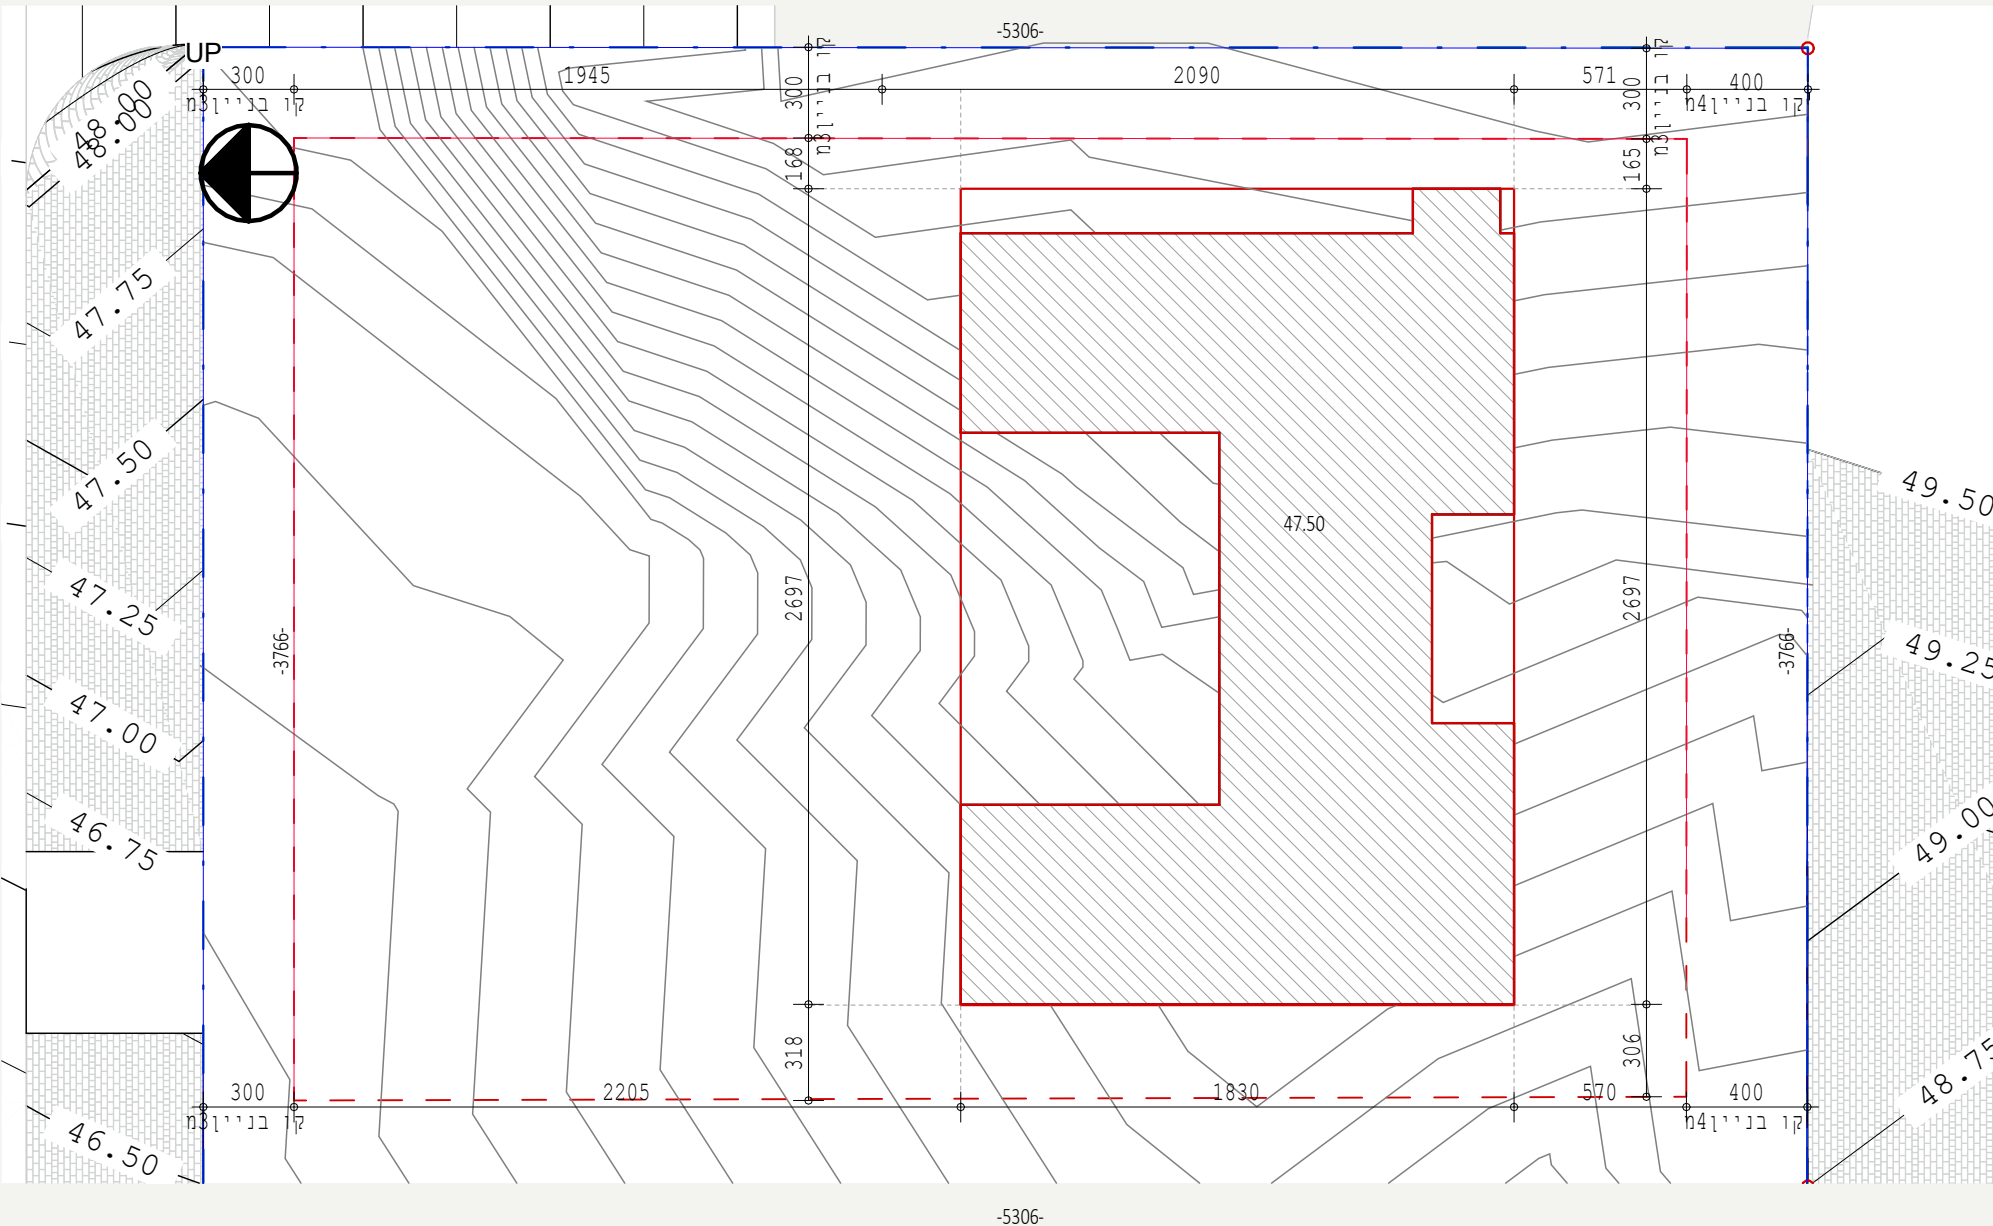

מפה מצבית והעמדה
1 : 250



מס'	תיאור גיליון:	קו"מ:
-00	שער	
-01	ניתוח סביבה	
-02	סקיצות פרוגרמה	
-03	הדמיות	

פיתוח שטח		
-04	תכנית קומת קרקע	1:100
-05	תכנית קומה א	1:100
תכנית שחור לכן		
-06	תכנית קומת קרקע	1:100
-07	תכנית קומה א	1:100
-08	תכנית קומה ב	1:100
-09	תכנית גגות	1:100
-10	חתכים	1:100
-11	חזיתות	1:100
-12	חזיתות	1:100

תכנית עבודה		
-13	תכנית עבודה קומה א	1:50
-14	חתך א, א'-ב'	1:50
-15	חזית צפונית, מערבית פרטי	1:50
-16	מדרגות-תכנית, פרטים	1:20 1:5
-17	מדרגות-חתכים	1:20
-18	קיר ייחודי-חתכים	1:20
-19	קיר ייחודי-פרטים	1:5

עיצוב פנים		
-20	תכנית ריהוט, ריפוף	1:50
-21	תכנית חקיה שטח אחיד	1:50
-22	הדמיות ופריסת קיר	1:50
-23	תכנון דלפק	1:20 1:10
-24	עיצוב חדר לדגמא	1:50

קונסטרוקציה		
-25	תכנית קונסטרוקציה	1:100

תיאור הפרויקט:

המבנה משמש כפרויקט משולב של מעונות סטודנטים עם קומת מסחר בקומת הקרקע, המיועדים לבית ספר לקולניריה המשלב ליקוט צמחים ותבלינים משטחים המיועדים לכך במגרש.

המבנה תוכנן בהתאם לסביבתו ולאקלים המקומי. חזית מרפסות המערבית פונה לנף הירוק וחשופה לאור הרך של אחה"צ, צפון לאיזור השכונה השקטה, דרום עם פתחים מצומצמים לכביש המהיר ומרפסות מזרח למשרדים עתידיים

העמדת המבנה תוכננה מתוך שילוב בין תנאי האקלים להקשר העירוני, המבנה משמש כחוצץ אקוסטי מפני הכביש הראשי בדרום, תוך יצירת כניסה שקטה ומזמינה כלפי השכונה בצפון. מרפסות המגורים הופנו למזרח ולמערב כדי למקסם אוורור ורוח טבעית, לשלוט נכון בחשיפה לשמש לאורך היום, ולהציע לסטודנטים במעונות איזון מושלם בין שקט ונוף פתוח לבין חיבור לאזור המסחרי

השראות:






Hotel Sand-Kastelbell, Italy



VIPE 201-Manaus Brasil

תהליך עבודה:

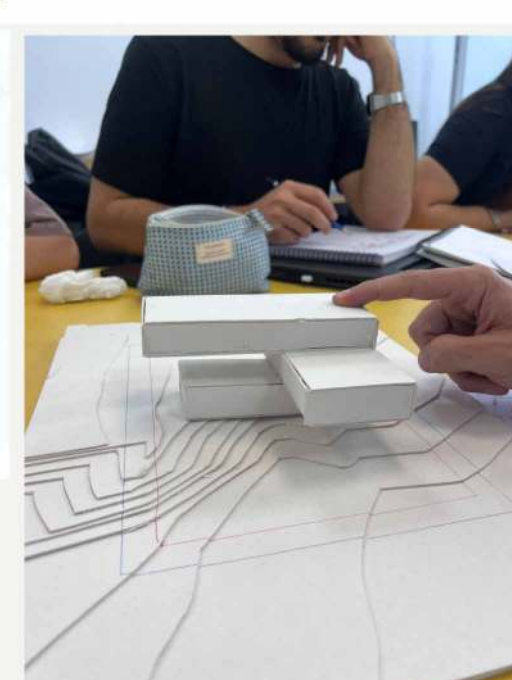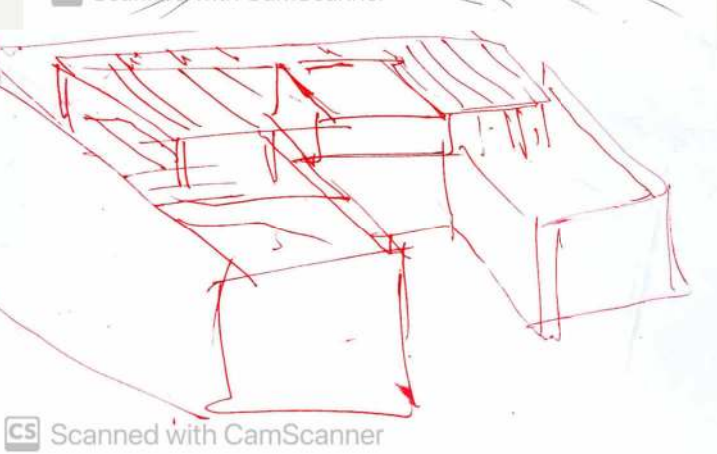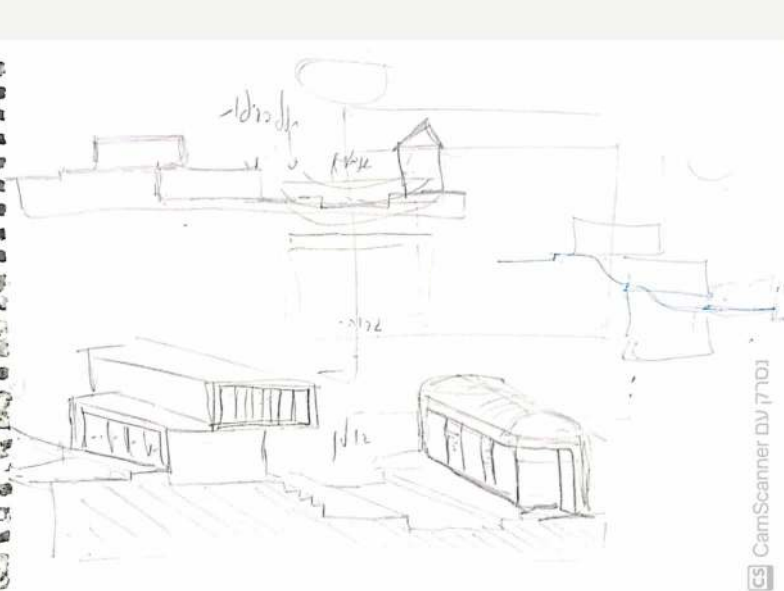


סכמות תנועה:


פירוט הפרוגרמה:

קומת קרקע

- 72 בית קפה
- 140 מעברים
- 12 ממ"ס
- 11 שירותים
- 7 מחסן
- 4.8 חדר מערכות
- 5.1 חדר כביסה
- 12 חדר מנהל
- 12 חדר הנהלת חשבונות
- 11 חדר אשפה

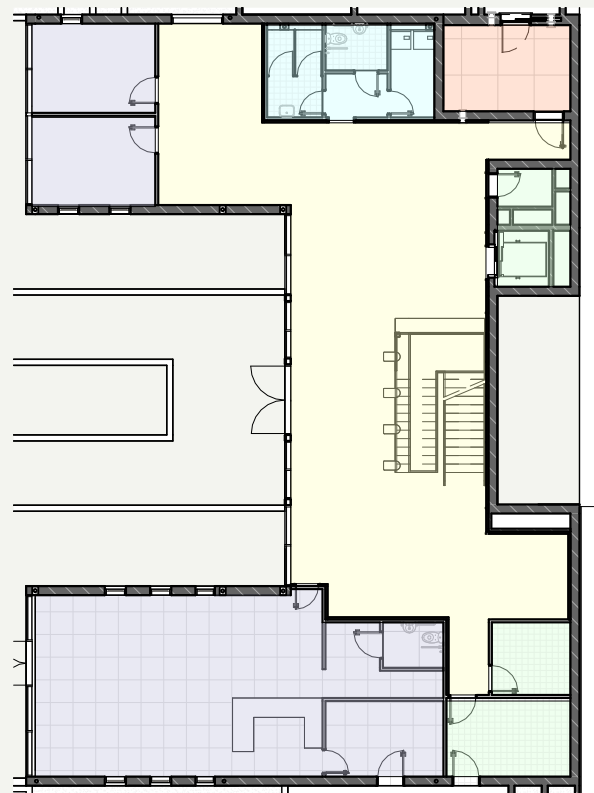


קומת קרקע-סכמות
1 : 250

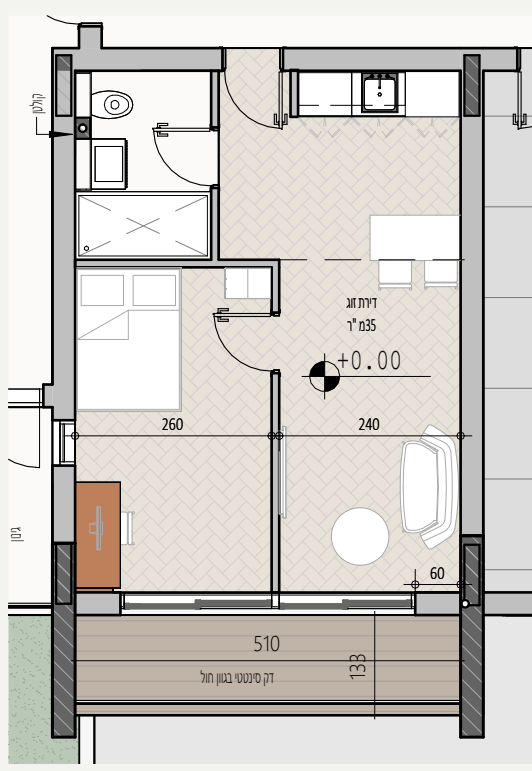


תכנית דירה לזוג
1 : 100




דירה לזוג

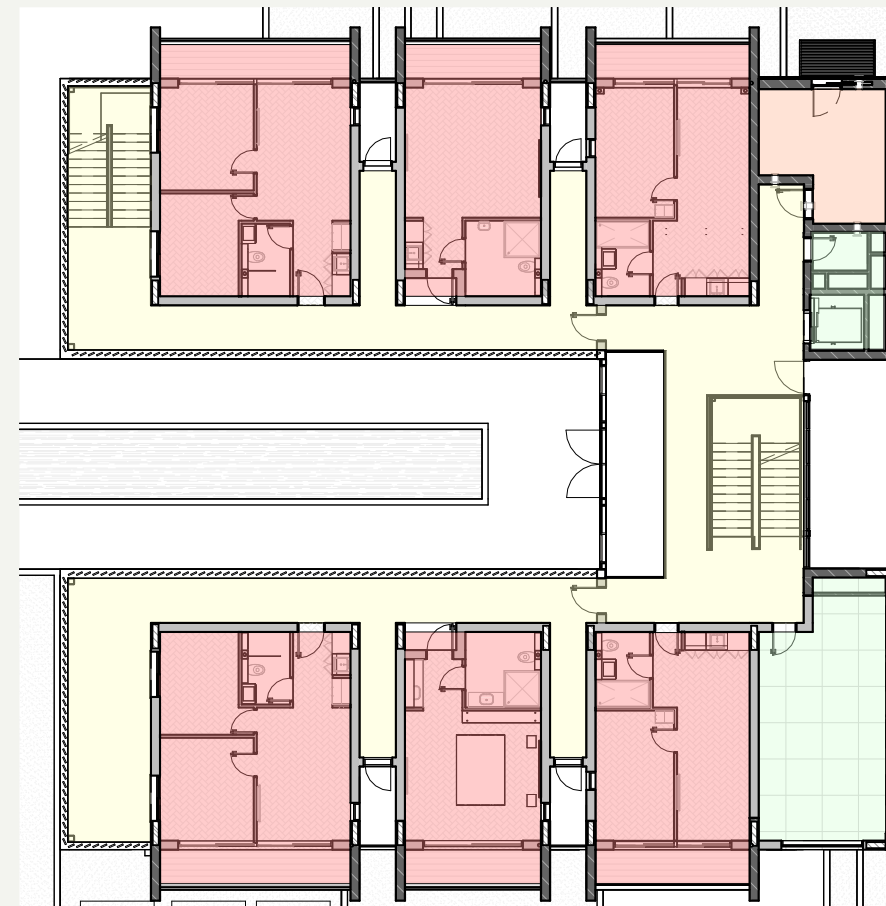


סכמות קומה א'
1 : 250

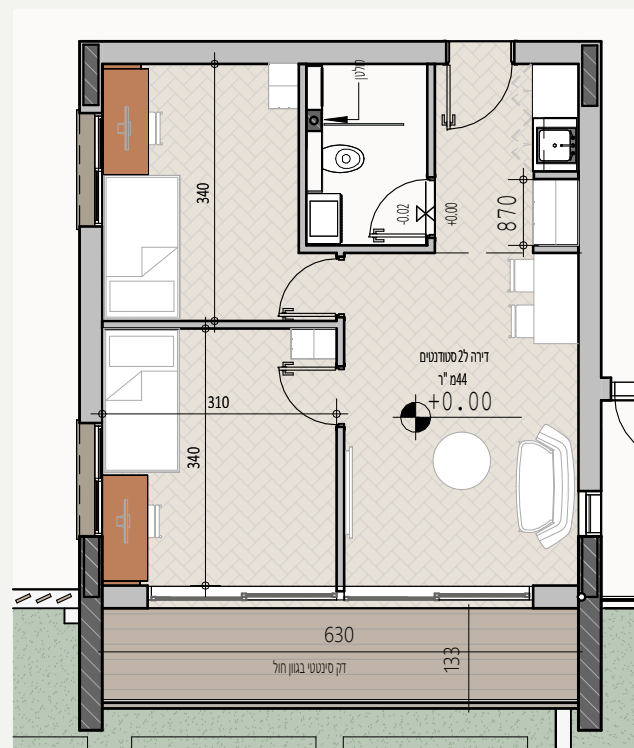


תכנית דירת 3חדרים
1 : 100

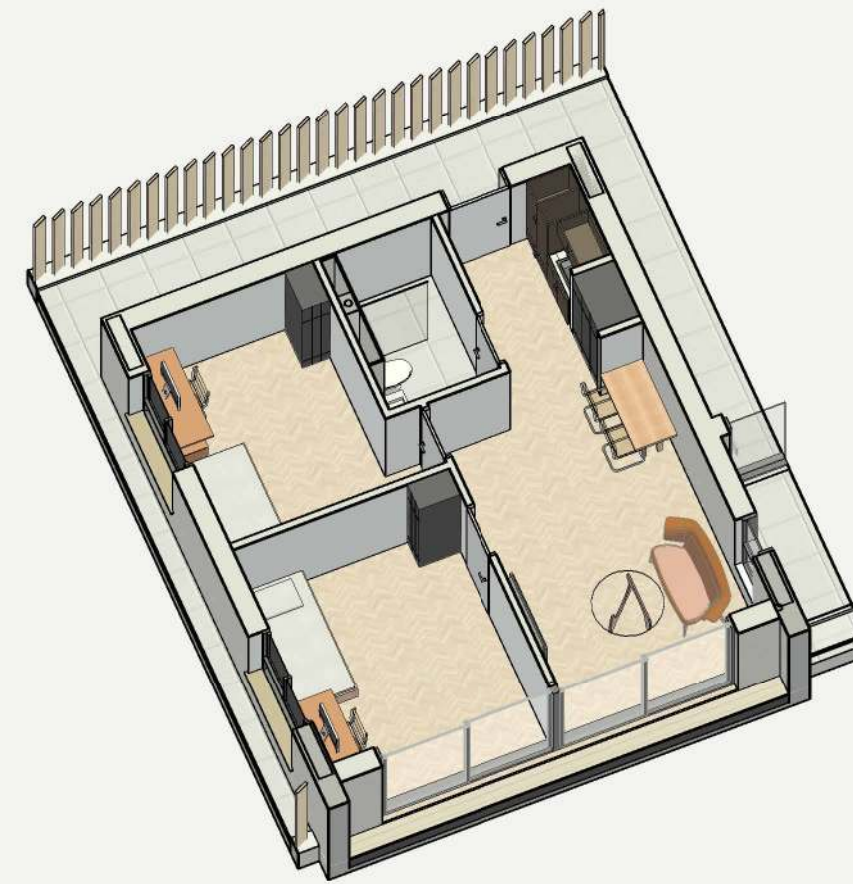


דירת 3חדרים

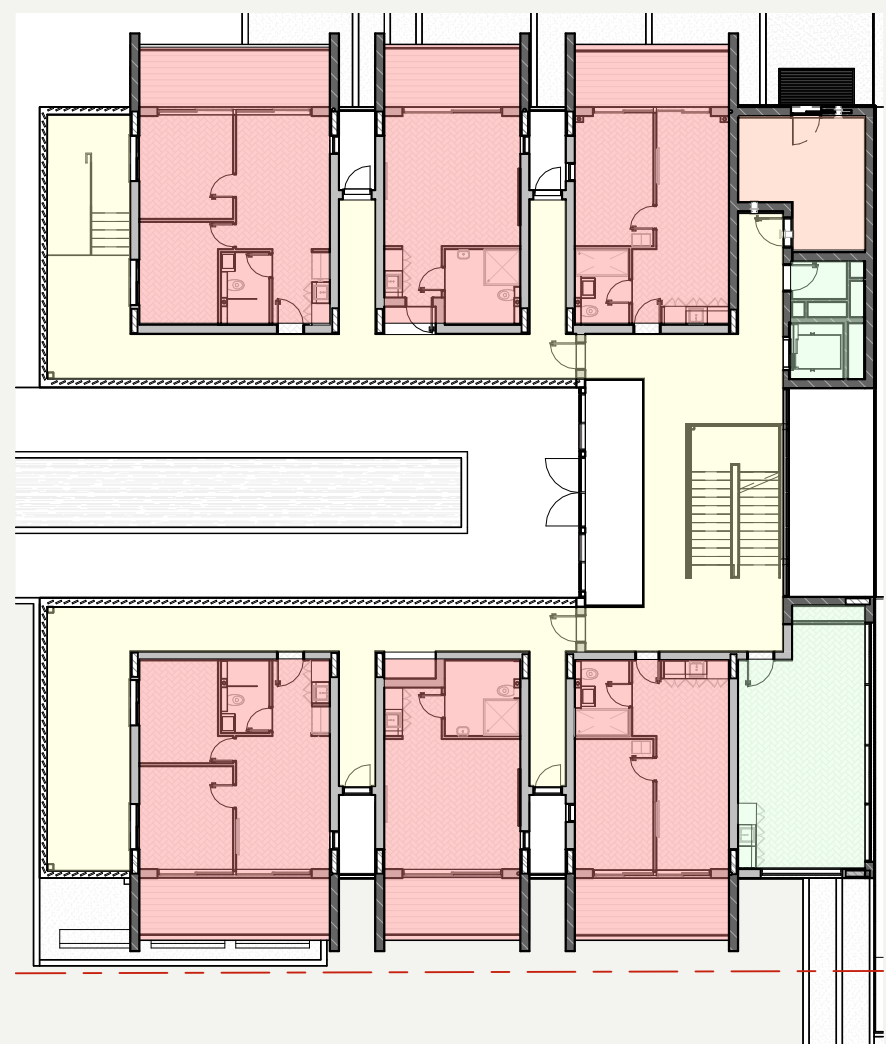

סכמות קומה ב'
1 : 250

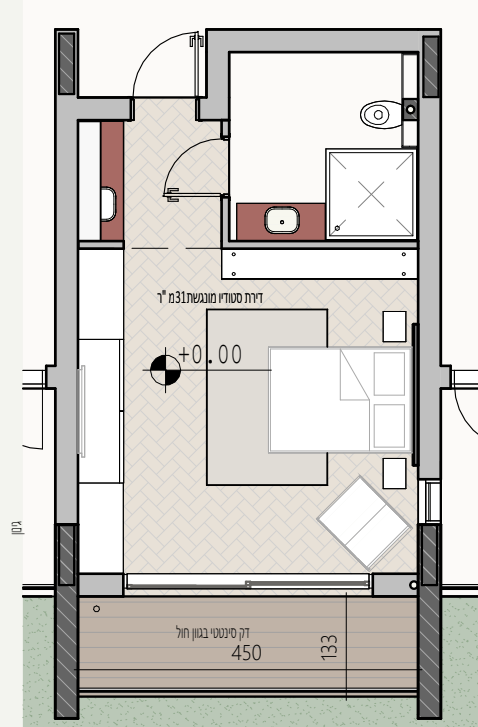

תכנית דירת סטודיו מונגשת
1 : 100

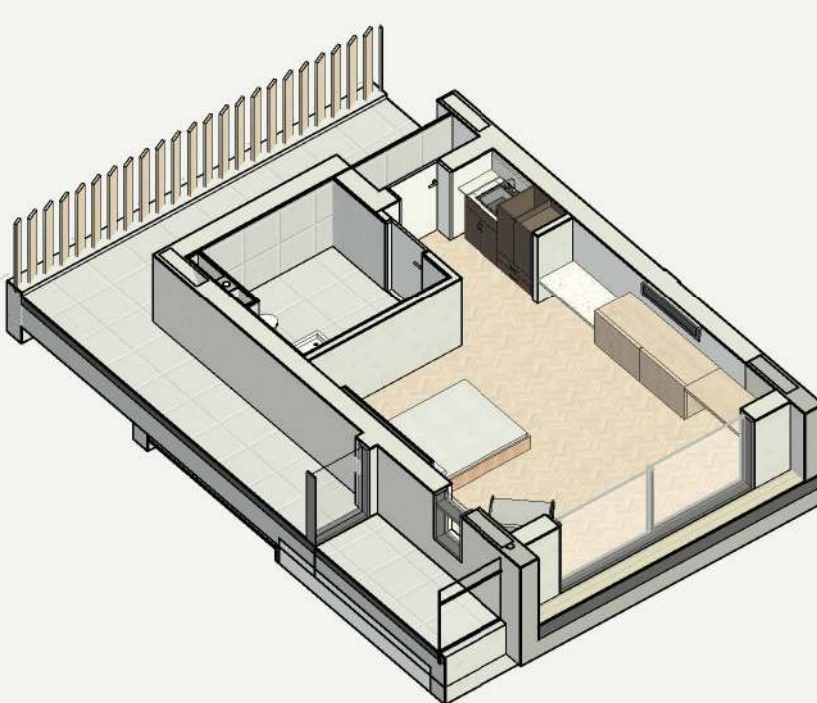

דירת סטודיו מונגשת

- תפעולי
- חדרים פרטיים
- שירותים
- מסחר
- מעברים
- ממ"ס

קומה ב

- 33 חדר סדנאות
- 4.8 חדר מערכות
- סה"כ 2חדרי שינה
- 70 טיפוס
- סה"כ 2חדרי שינה
- 62 טיפוס
- סה"כ 2חדרי שינה
- 88 טיפוס
- 65 מרפסות
- 16 ממ"ס

שם הפרויקט:
מעונות סטודנטים



מס'	תיאור גיליון:	ק"מ:
-00	שער	1:100
-01	ניחוח סביבה	
-02	סקיצות-פרוגרמה	
-03	הדמיות	
פיתוח שטח		
-04	תכנית קומות קרקע	1:100
-05	תכנית קומה א	1:100
תכנית שחור לבן		
-06	תכנית קומות קרקע	1:100
-07	תכנית קומה א	1:100
-08	תכנית קומה ב	1:100
-09	תכנית גגות	1:100
-10	חתכים	1:100
-11	חזיתות	1:100
-12	חזיתות	1:100
תכנית עבודה		
-13	תכנית עבודה קומה א	1:50
-14	חתך א-א', ב-ב'	1:50
-15	חזית צפונית, מערבית	1:50
פרטי ביין		
-16	מדגות-תכנית, פרטים	1:20 1:5
-17	מדגות-חתכים	1:20
-18	קיר ייחודי-חתכים	1:20
-19	קיר ייחודי-פרטים	1:5
עיצוב פנים		
-20	תכנית ריהוט, רישוף	1:50
-21	תכנית חקירה מרחב ואור	1:50
-22	הדמיות ופריסת קיר	1:50
-23	תכנון דלפק	1:20 1:10
-24	עיצוב חדר לדגמא	1:50
קונסטרוקציה		
-25	תכנית קונסטרוקציה	1:100

מגיש/ה:
כרמל סעדון
שם ראש המגמה:
שרון גפני
שם המנחה:
לית'ל

תאריך:

23\06\2026



חזית מזרחית



חזית מערבית



חזית צפונית



חזית דרומית

שם הפרויקט:
מעונות סטודנטיים




מס'	תיאור גיליון:	קנ"מ:
-00	שער	
-01	ניחוח סביבה	
-02	סקיצות פרוגרמה	
-03	הדמיות	
פיתוח שטח		
-04	תכנית קומת קרקע	1:100
-05	תכנית קומה א	1:100
תכנית שחור לבן		
-06	תכנית קומת קרקע	1:100
-07	תכנית קומה א	1:100
-08	תכנית קומה ב	1:100
-09	תכנית גגות	1:100
-10	חתיכים	1:100
-11	חיתות	1:100
-12	חיתות	1:100
תכנית עבודה		
-13	תכנית עבודה קומה א	1:50
-14	חתך א'-ב'	1:50
-15	חית צפנית, מערבית פרטי בין	1:50
-16	מדרגות תכנית, פרטים	1:20
-17	מדרגות-חתיכים	1:20
-18	קיר ייחודי-חתיכים	1:20
-19	קיר ייחודי-פרטים	1:5
עיצוב פנים		
-20	תכנית ריהוט, רישוף	1:50
-21	תכנית חזקה משה אורי	1:50
-22	הדמיות פריסת קיר	1:50
-23	תכנון דלפק	1:20
-24	עיצוב חדר לדגמא	1:50
קונסטרוקציה		
-25	תכנית קונסטרוקציה	1:100

מגישה:
כרמל סעדון
שם ראש המגמה:
שרון גפני
שם המנחה:
ליית'

תאריך:

23/06/2026

תכנית קרקע פיתוח שטח
1 : 100

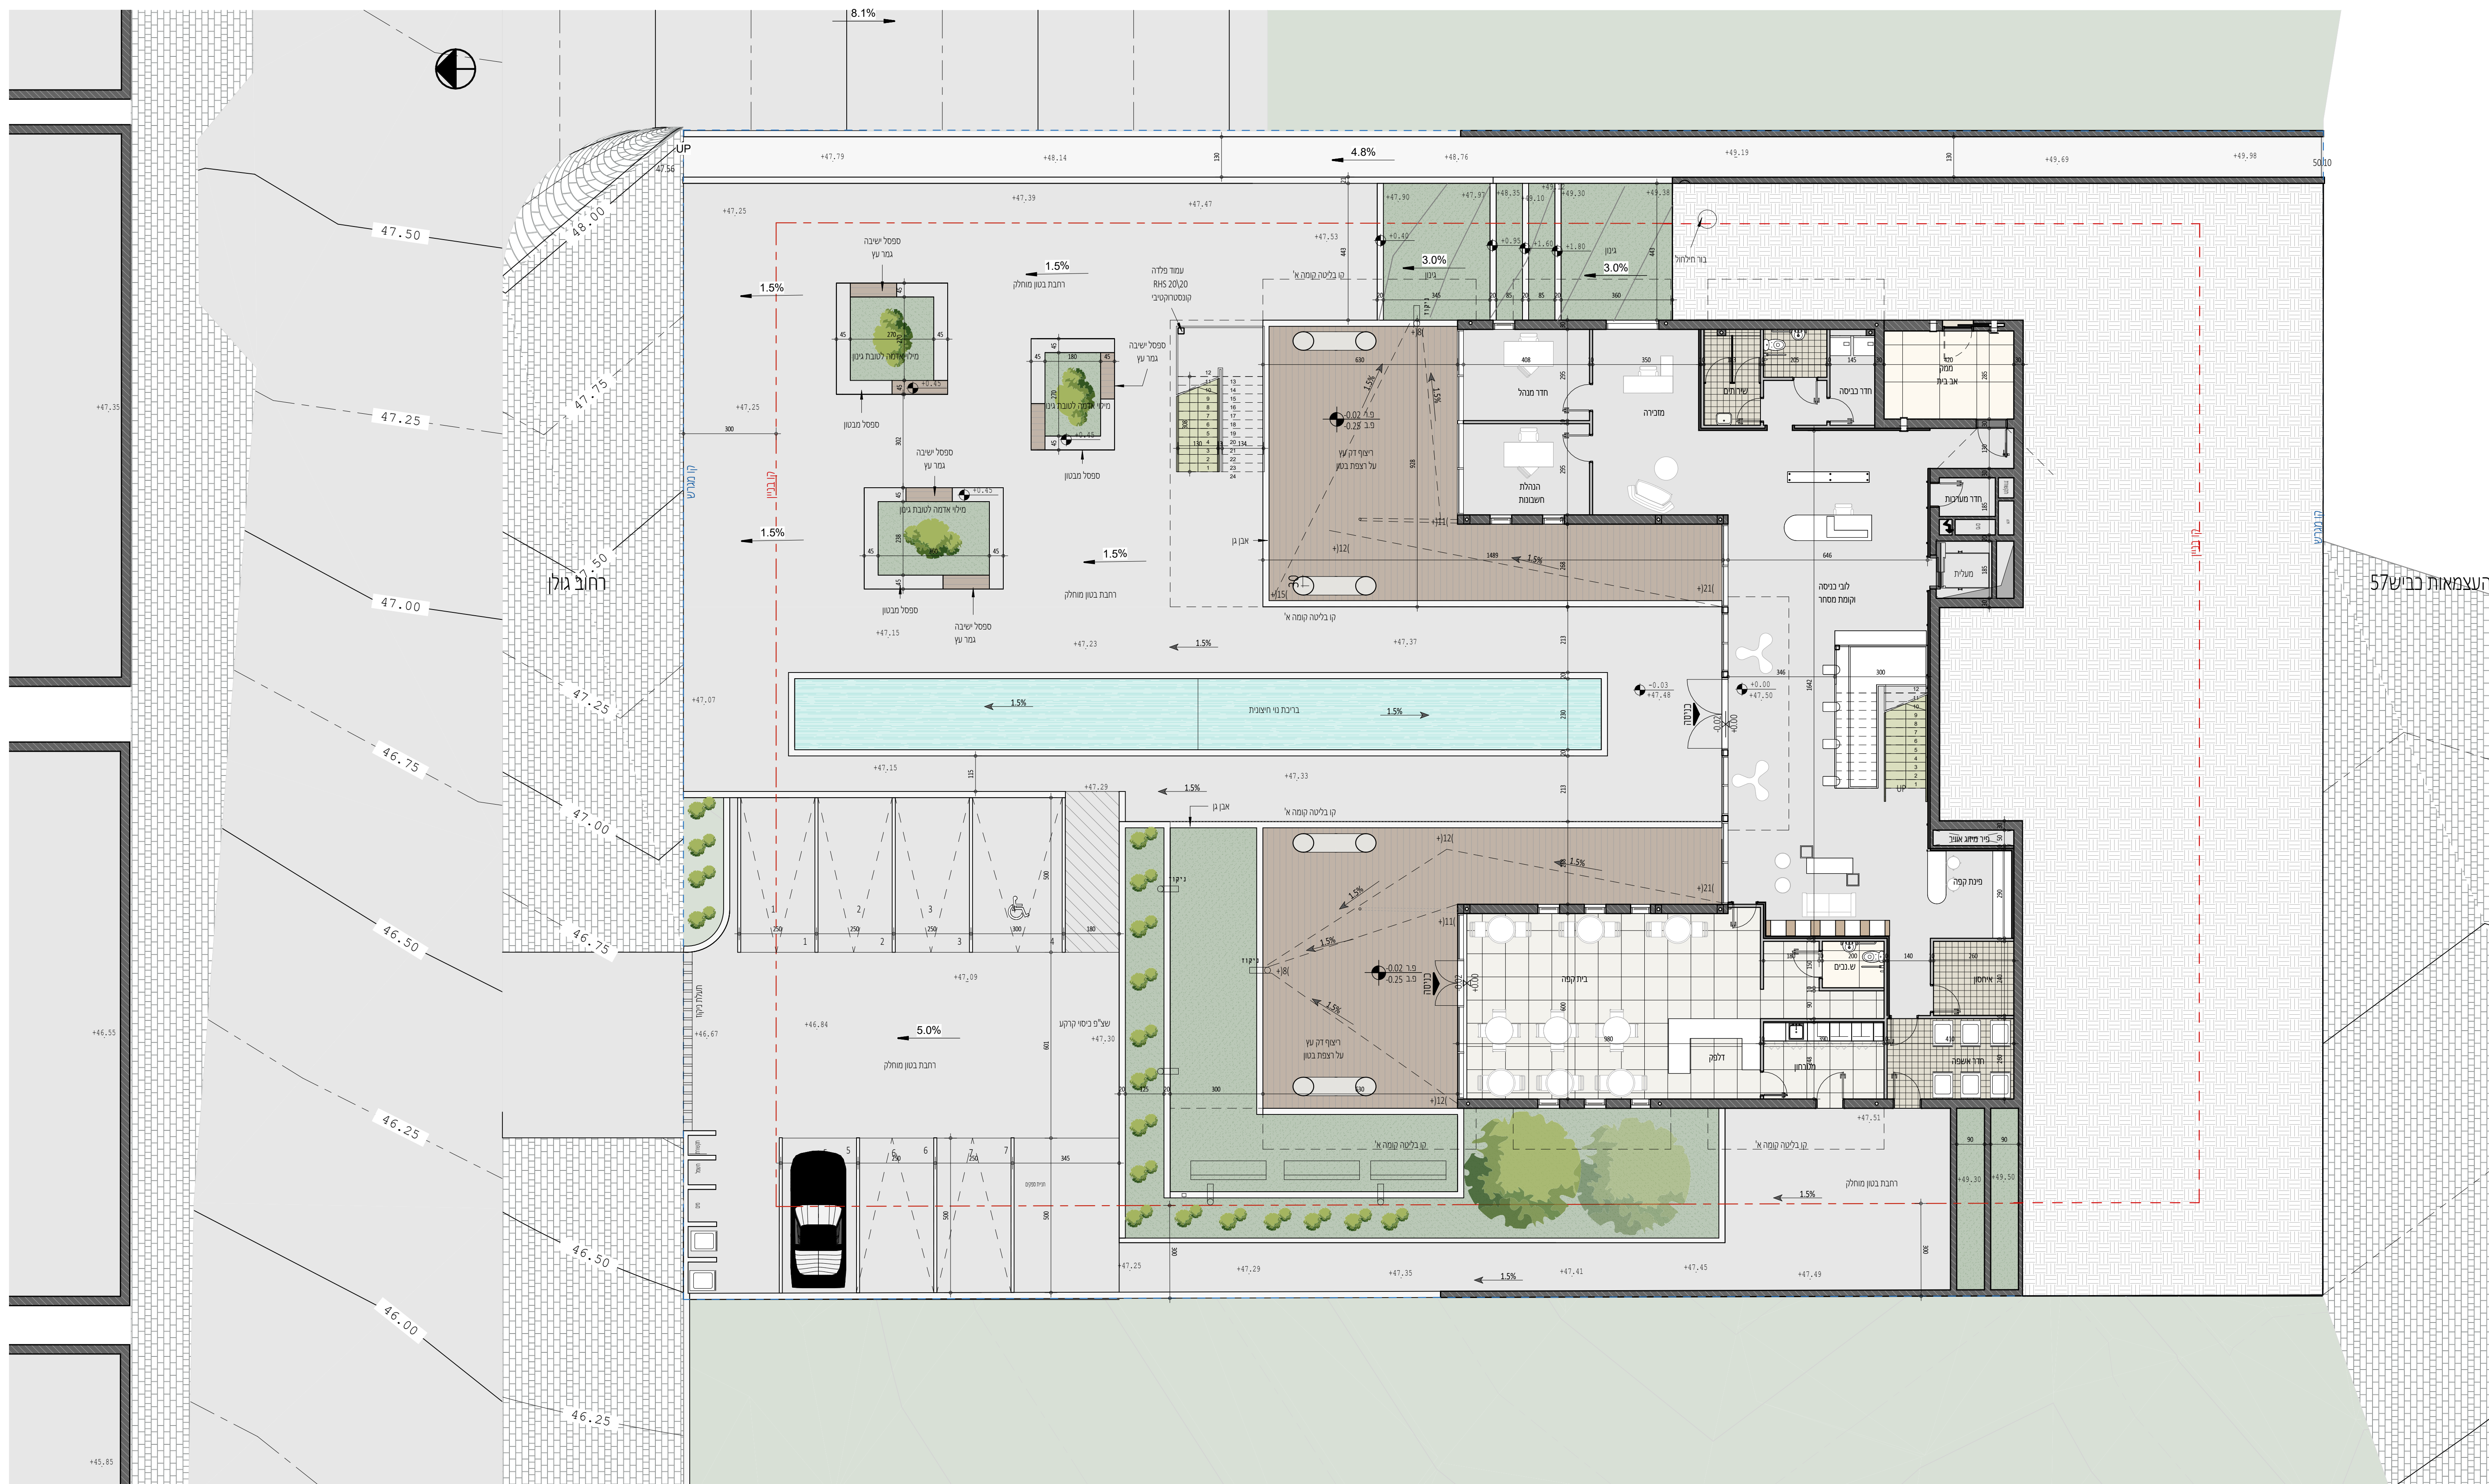

שם הפרויקט:
מעונות סטודנטים




מס'	תיאור גיליון:	ק"מ:
-00	שער	
-01	ניחוח סביבה	
-02	סקיצות פרוגרמה	
-03	הדמיות	
פיתוח שטח		
-04	תכנית קומת קרקע	1:100
-05	תכנית קומה א	1:100
תכניות שחור לבן		
-06	תכנית קומת קרקע	1:100
-07	תכנית קומה א	1:100
-08	תכנית קומה ב	1:100
-09	תכנית גגות	1:100
-10	חתיכים	1:100
-11	חיתות	1:100
-12	חיתות	1:100
תכנית עבודה		
-13	תכנית עבודה קומה א	1:50
-14	חתך א-א', ב-ב'	1:50
-15	חזית צפונית, מערבית	1:50
פרטי ביין		
-16	מדרגות-תכנית, פרטים	1:5 1:20
-17	מדרגות-חתיכים	1:20
-18	קיר ייחודי-חתיכים	1:20
-19	קיר ייחודי-פרטים	1:5
עיצוב פנים		
-20	תכנית ריהוט, רישוף	1:50
-21	תכנית חקירה מיוחדת	1:50
-22	הדמיות ופריסת קיר	1:50
-23	תכנון דלפק	1:10 1:20
-24	עיצוב חדר לדגמא	1:50
קונסטרוקציה		
-25	תכנית קונסטרוקציה	1:100

מגישה:
כרמל סעדון
שם ראש המגמה:
שרון גפני
שם המנחה:
לית'

תאריך:

02/23/26

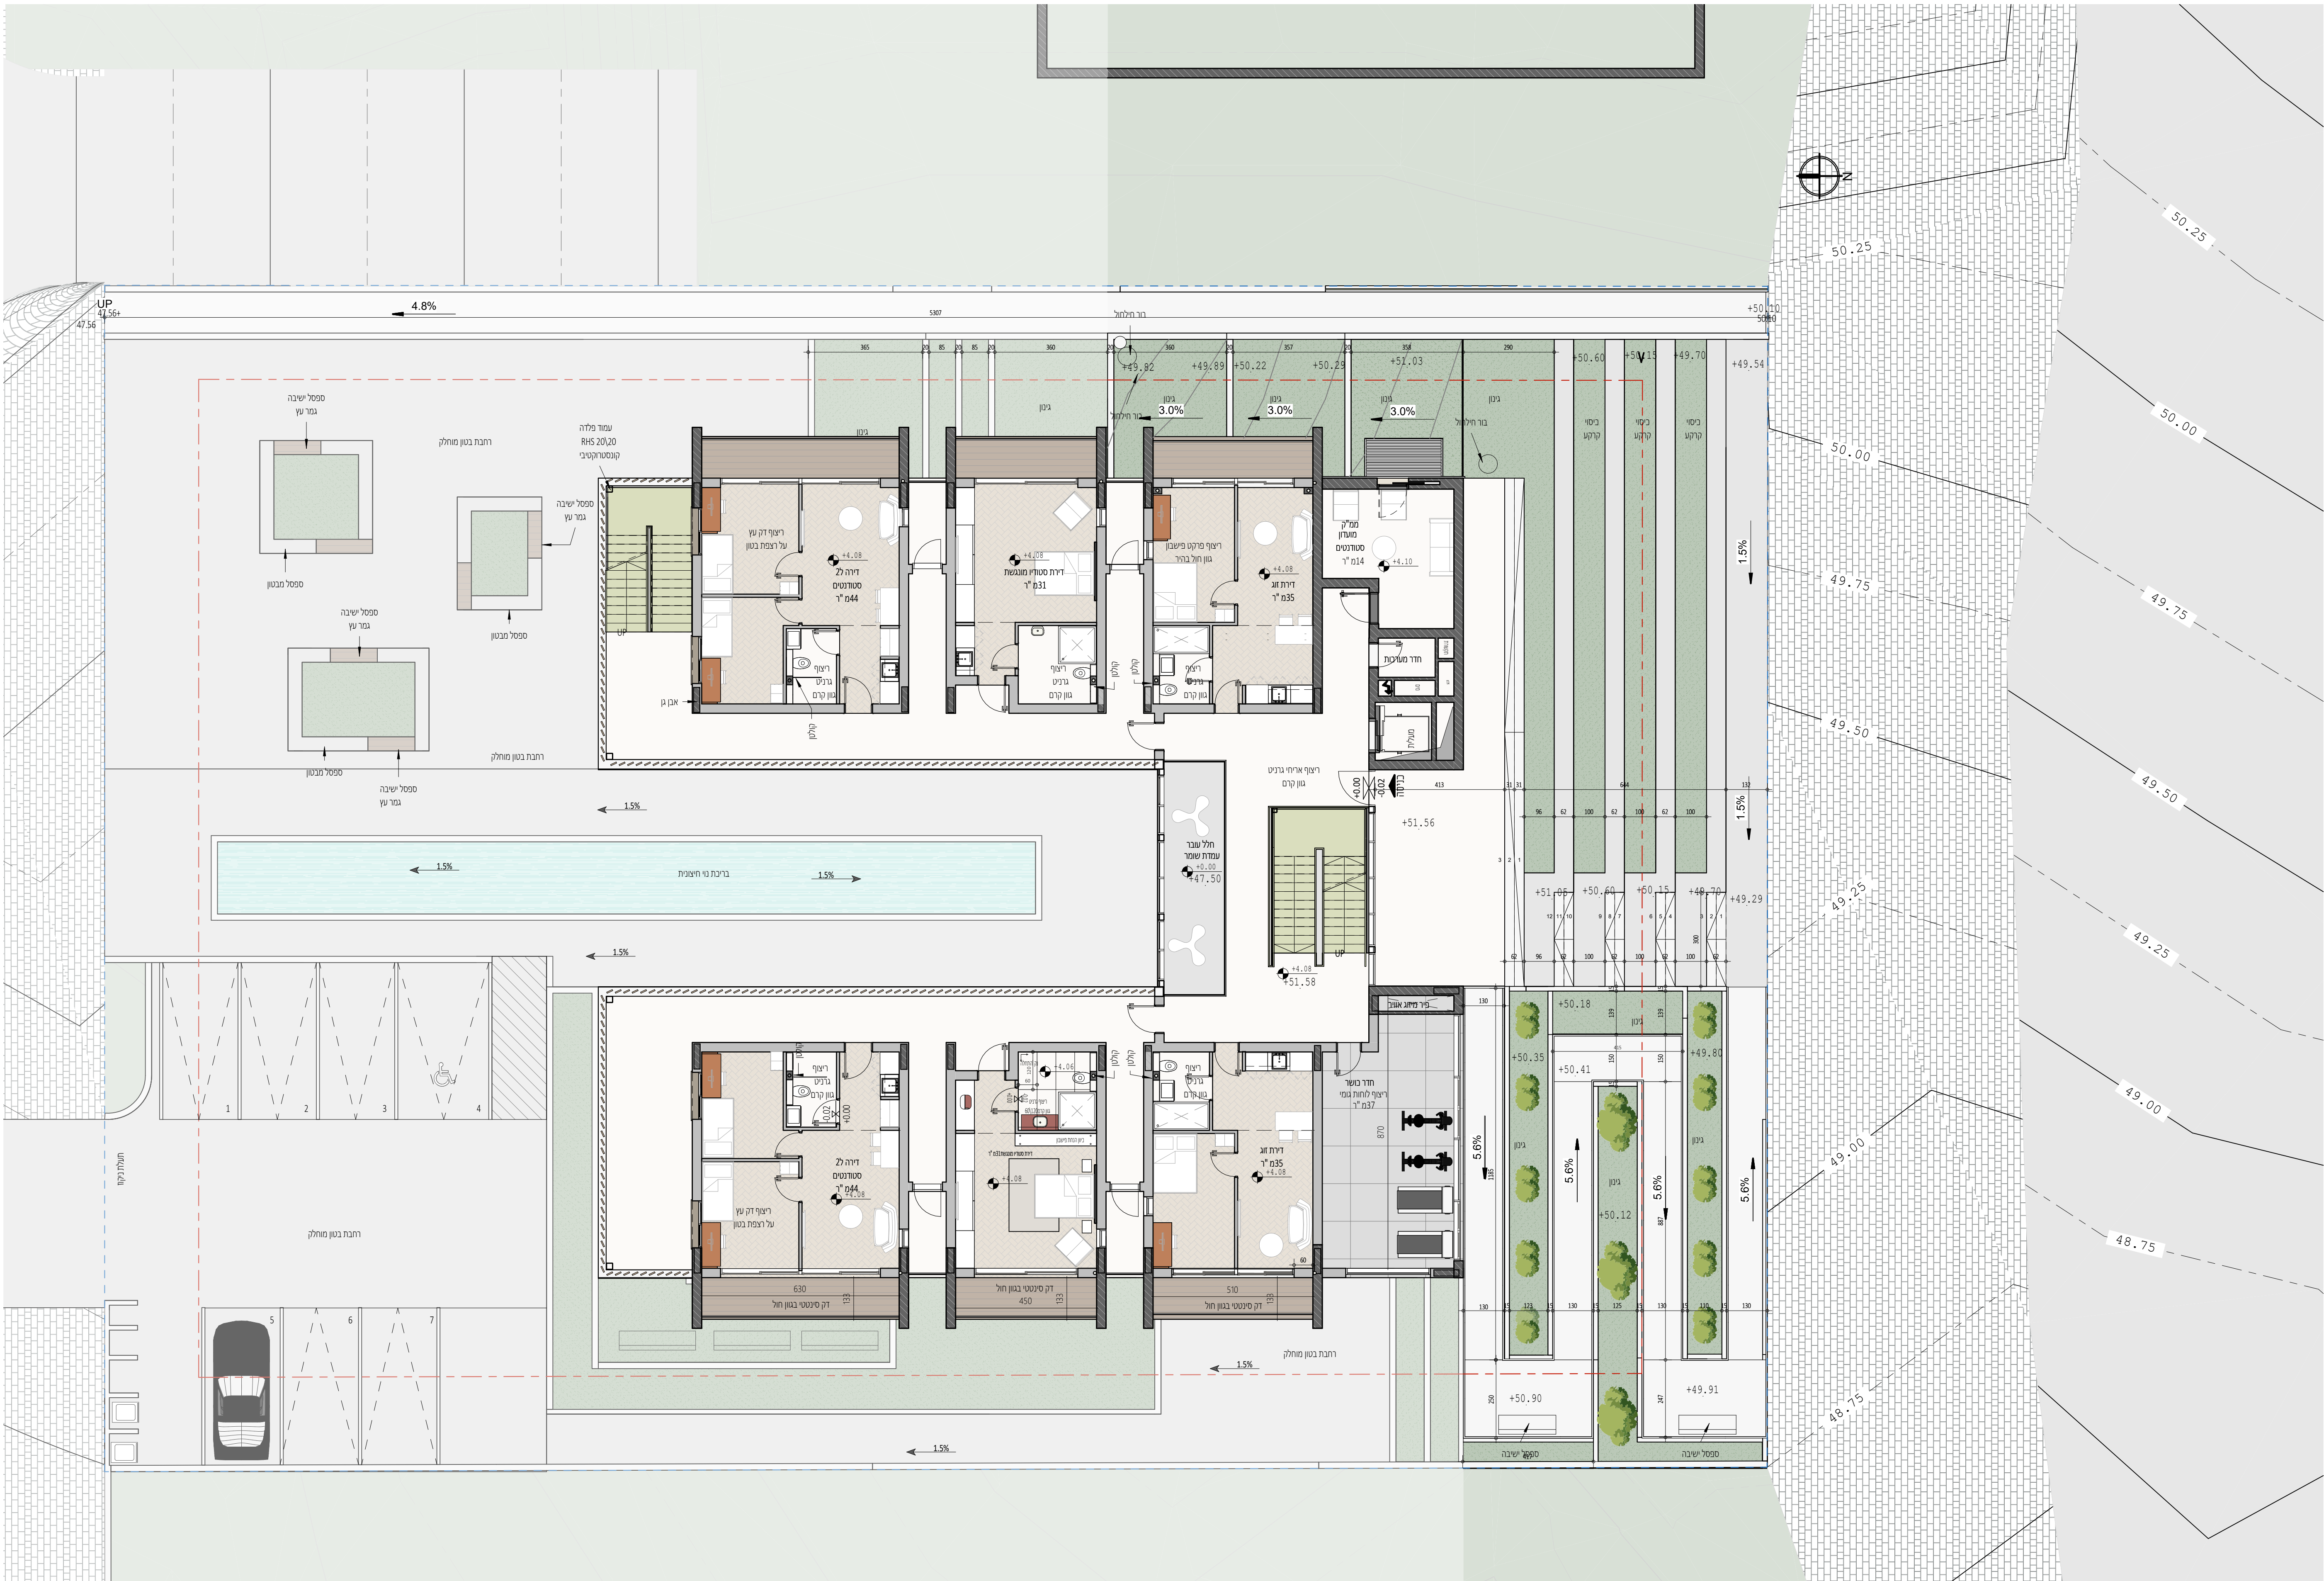

שם הפרויקט:
מעונות סטודנטיים




מס'	תיאור גיליון:	קנ"מ:
-00	שער	
-01	ניתוח סביבה	
-02	סקיצות פרוגרמה	
-03	הדמיות	
פיתוח שטח		
-04	תכנית קומת קרקע	1:100
-05	תכנית קומה א	1:100
תכניות שחור לבן		
-06	תכנית קומת קרקע	1:100
-07	תכנית קומה א	1:100
-08	תכנית קומה ב	1:100
-09	תכנית גגות	1:100
-10	חתכים	1:100
-11	חזיתות	1:100
-12	חזיתות	1:100
תכנית עבודה		
-13	תכנית עבודה קומה א	1:50
-14	חתך א-א', ב-ב'	1:50
-15	חזית צפונית, מערבית	1:50
-16	פרטי בניין	
1:5	מדרגות תכנית, פרטים	1:20
1:20	מדרגות חתכים	1:20
1:20	קיר ייחודי-חתכים	1:20
1:5	קיר ייחודי-פרטים	1:5
-19	קיר ייחודי-פרטים	1:5
עיצוב פנים		
1:50	תכנית ריהוט, רציף	1:50
1:50	תכנית חזקה שטח אוור	1:50
1:50	הדמיות ופריסת קיר	1:50
1:10	תכנון דלפק	1:20
1:50	עיצוב חדר לדגמא	1:50
קונסטרוקציה		
1:100	תכנית קונסטרוקציה	1:100

מגיש/ה:
כרמל סעדון
שם ראש המגמה:
שרון גפני
שם המנחה:
ליית'

תאריך:

23/06/2026

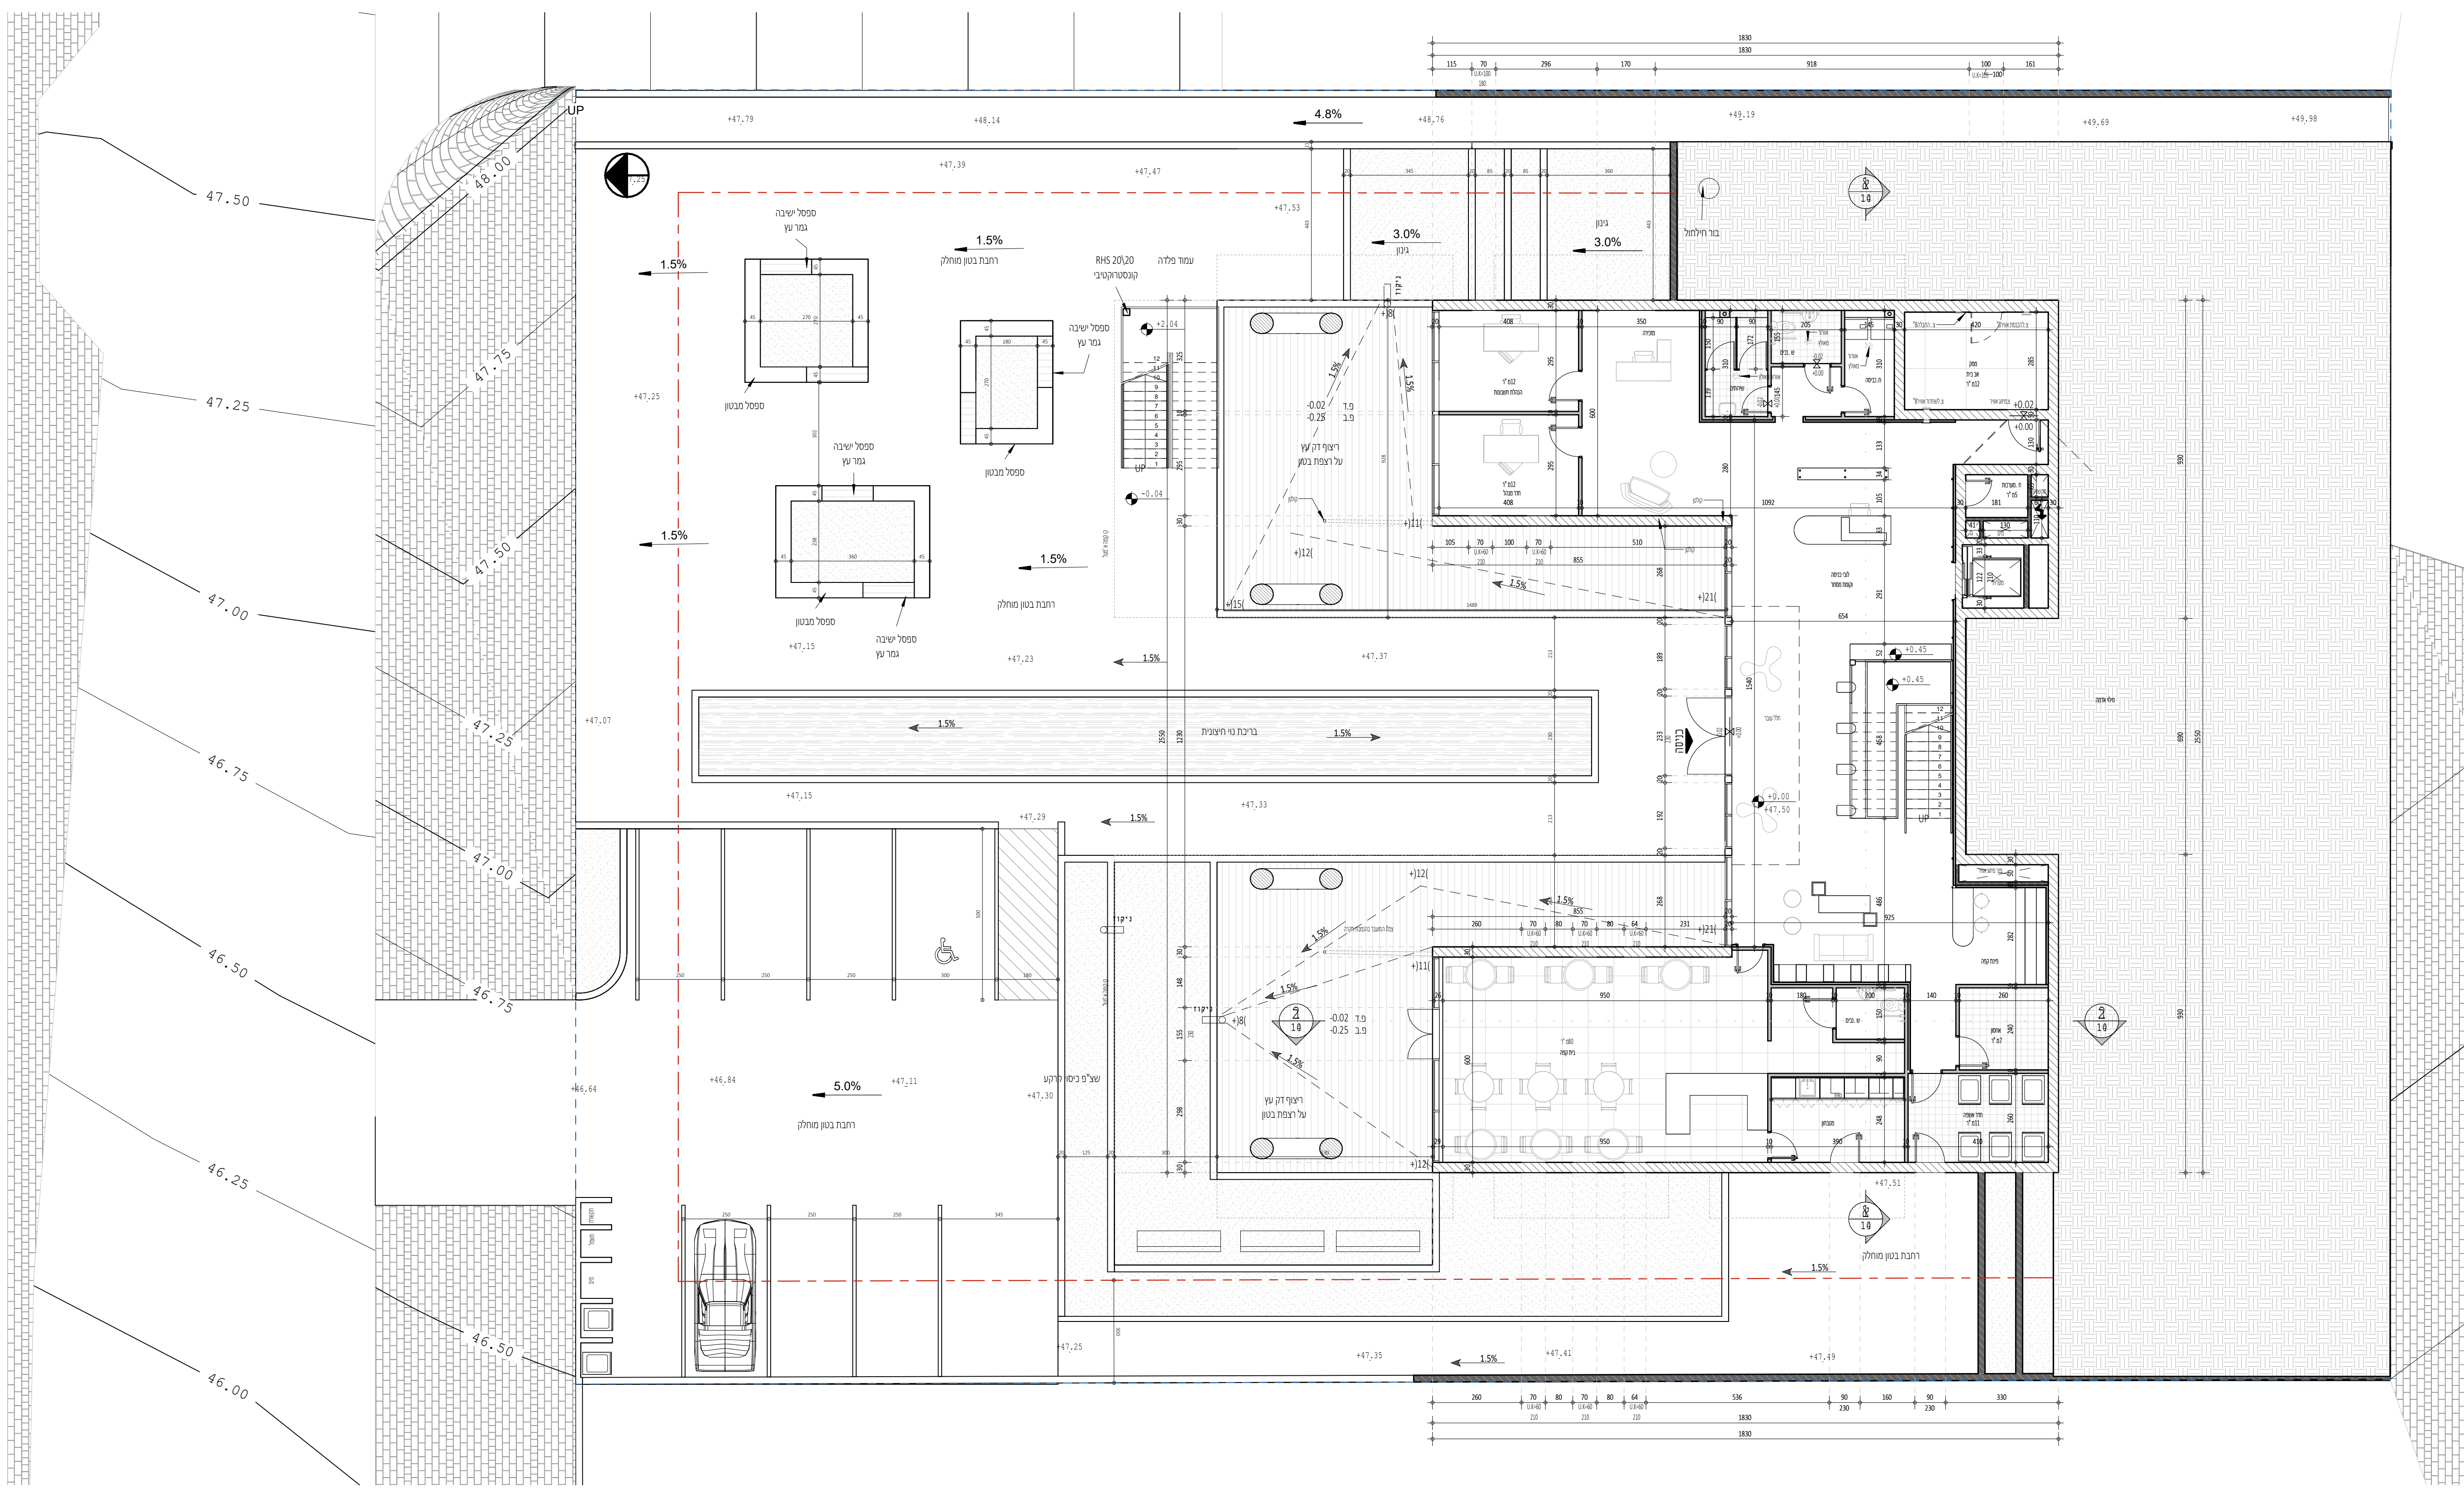

קומת קרקע שחור לבן
1 : 100

שם הפרויקט:

מעונות סטודנטים



מס'	תיאור גיליון:	ק"מ
-00	שער	
-01	ניחוח סביבה	
-02	סקיצות פרוגרמה	
-03	הדמיות	
פיתוח שטח		
-04	תכנית קומות קרקע	1:100
-05	תכנית קומה א	1:100
תכנית שחזור לכן		
-06	תכנית קומות קרקע	1:100
-07	תכנית קומה א	1:100
-08	תכנית קומה ב	1:100
-09	תכנית גגות	1:100
-10	חתיכים	1:100
-11	חזיתות	1:100
-12	חזיתות	1:100
תכנית עבודה		
-13	תכנית עבודה קומה א	1:50
-14	חתך א, א'-ב'	1:50
-15	חזית צפון, מערבית	1:50
-16	פרטי בנין	1:5
-17	מדרגות תכנית, פרטים	1:20
-18	מדרגות-חתיכים	1:20
-19	קיר ייחודי-חתיכים	1:20
-20	קיר ייחודי-פרטים	1:5
עיצוב פנים		
-21	תכנית ריהוט, רציף	1:50
-22	תכנית חזקה שטח אזור	1:50
-23	הדמיות ופריסת קיר	1:50
-24	תכנון דלפק	1:10
-25	עיצוב חדר לדוגמה	1:50
קונסטרוקציה		
-26	תכנית קונסטרוקציה	1:100

מגיש/ה:

כרמל סעדון

שם ראש הממנה:

שרון גפני

שם הממנה:


לית'

תאריך:

23/06/2026

קומה א שחזור לבן

1 : 100

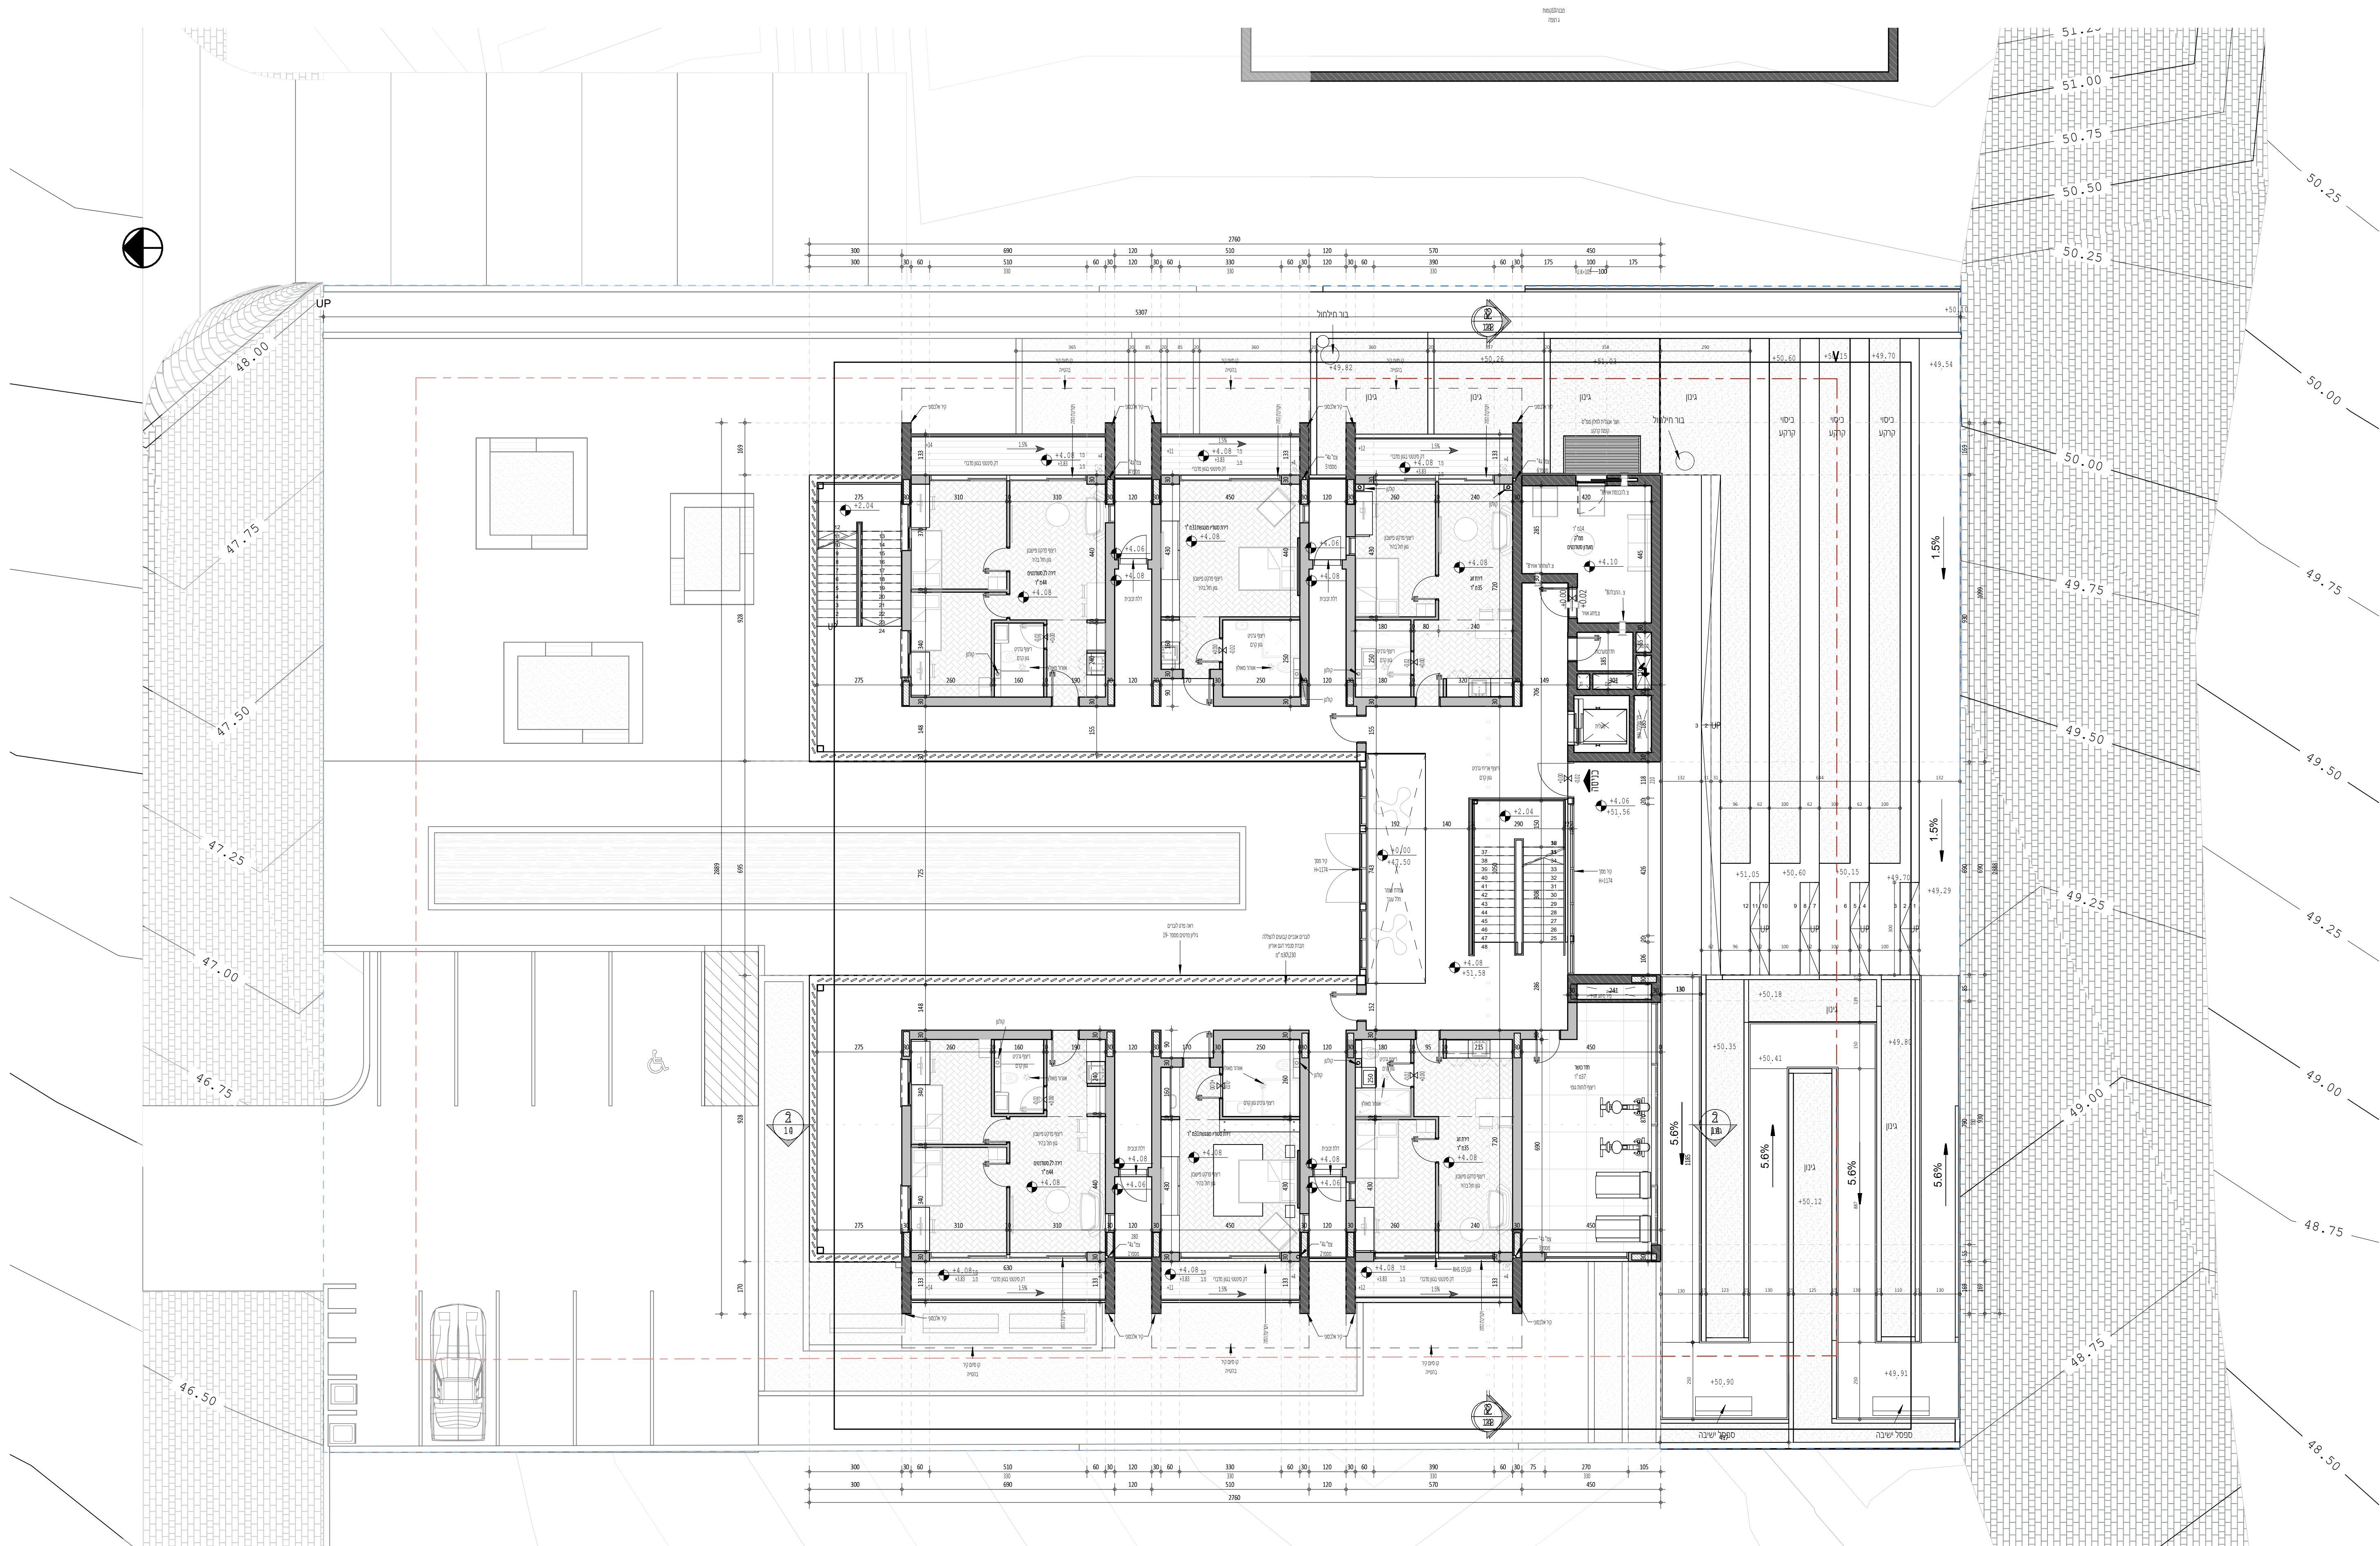

שם הפרויקט:

מעונות סטודנטיים



מס'	תיאור גיליון:	קנ"מ:
-00	שער	
-01	ניתוח סביבה	
-02	סקיצות פרוגרמה	
-03	הדמיות	
פיתוח שטח		
-04	תכנית קומות קרקע	1:100
-05	תכנית קומה א	1:100
תכניות שחזור לבן		
-06	תכנית קומות קרקע	1:100
-07	תכנית קומה א	1:100
-08	תכנית קומה ב	1:100
-09	תכנית גגות	1:100
-10	חתכים	1:100
-11	חזיתות	1:100
-12	חזיתות	1:100
תכנית עבודה		
-13	תכנית עבודה קומה א	1:50
-14	חתך א-א', ב-ב'	1:50
-15	חזית צפונית, מערבית	1:50
-16	פרטי בנין	
1:5	מדרגות-תכנית, פרטים	1:20
-17	מדרגות-חתכים	1:20
-18	קיר ייחודי-חתכים	1:20
-19	קיר ייחודי-פרטים	1:5
עיצוב פנים		
1:50	תכנית ריהוט, רישוף	1:50
1:50	תכנית חקירה שטח אזור	1:50
1:50	הדמיות ופריסת קיר	1:50
1:10	תכנון דלפק	1:20
1:50	עיצוב חדר לדוגמא	1:50
קונסטרוקציה		
1:100	תכנית קונסטרוקציה	1:100
-25	תכנית קונסטרוקציה	1:100

מגיש/ה:

כרמל סעדון

שם ראש המגמה:

שרון גפני

שם המנחה:

לית'

תאריך:

קומה ב שחזור לבן
1 : 100

23/06/2026

שם הפרויקט:
מעונות סטודנטיים



מס'	תיאור גיליון:	קנ"מ:
-00	שער	
-01	ניתוח סביבה	
-02	סקיצות פרוגרמה	
-03	הדמיות	
פיתוח שטח		
-04	תכנית קומת קרקע	1:100
-05	תכנית קומה א	1:100
תכנית שחזור לבן		
-06	תכנית קומת קרקע	1:100
-07	תכנית קומה א	1:100
-08	תכנית קומה ב	1:100
-09	תכנית גגות	1:100
-10	חתכים	1:100
-11	חזיתות	1:100
-12	חזיתות	1:100
תכנית עבודה		
-13	תכנית עבודה קומה א	1:50
-14	חתך א-א', ב-ב'	1:50
-15	חזית צפונית, מערבית	1:50
פרטי בנין		
-16	מדרגות-תכנית, פרטים	1:5 1:20
-17	מדרגות-חתכים	1:20
-18	קיר ייחודי-חתכים	1:20
-19	קיר ייחודי-פרטים	1:5
עיצוב פנים		
-20	תכנית ריהוט, ריצוף	1:50
-21	תכנית חקירה ופנאי	1:50
-22	הדמיות ופריסת קיר	1:50
-23	תכנון דלפק	1:10 1:20
-24	עיצוב חדר לדוגמא	1:50
קונסטרוקציה		
-25	תכנית קונסטרוקציה	1:100

מגיש/ה:

כרמל סעדון

שם ראש המגמה:


שרון גפני

שם המנחה:


ליית'

תאריך:

23/06/2026

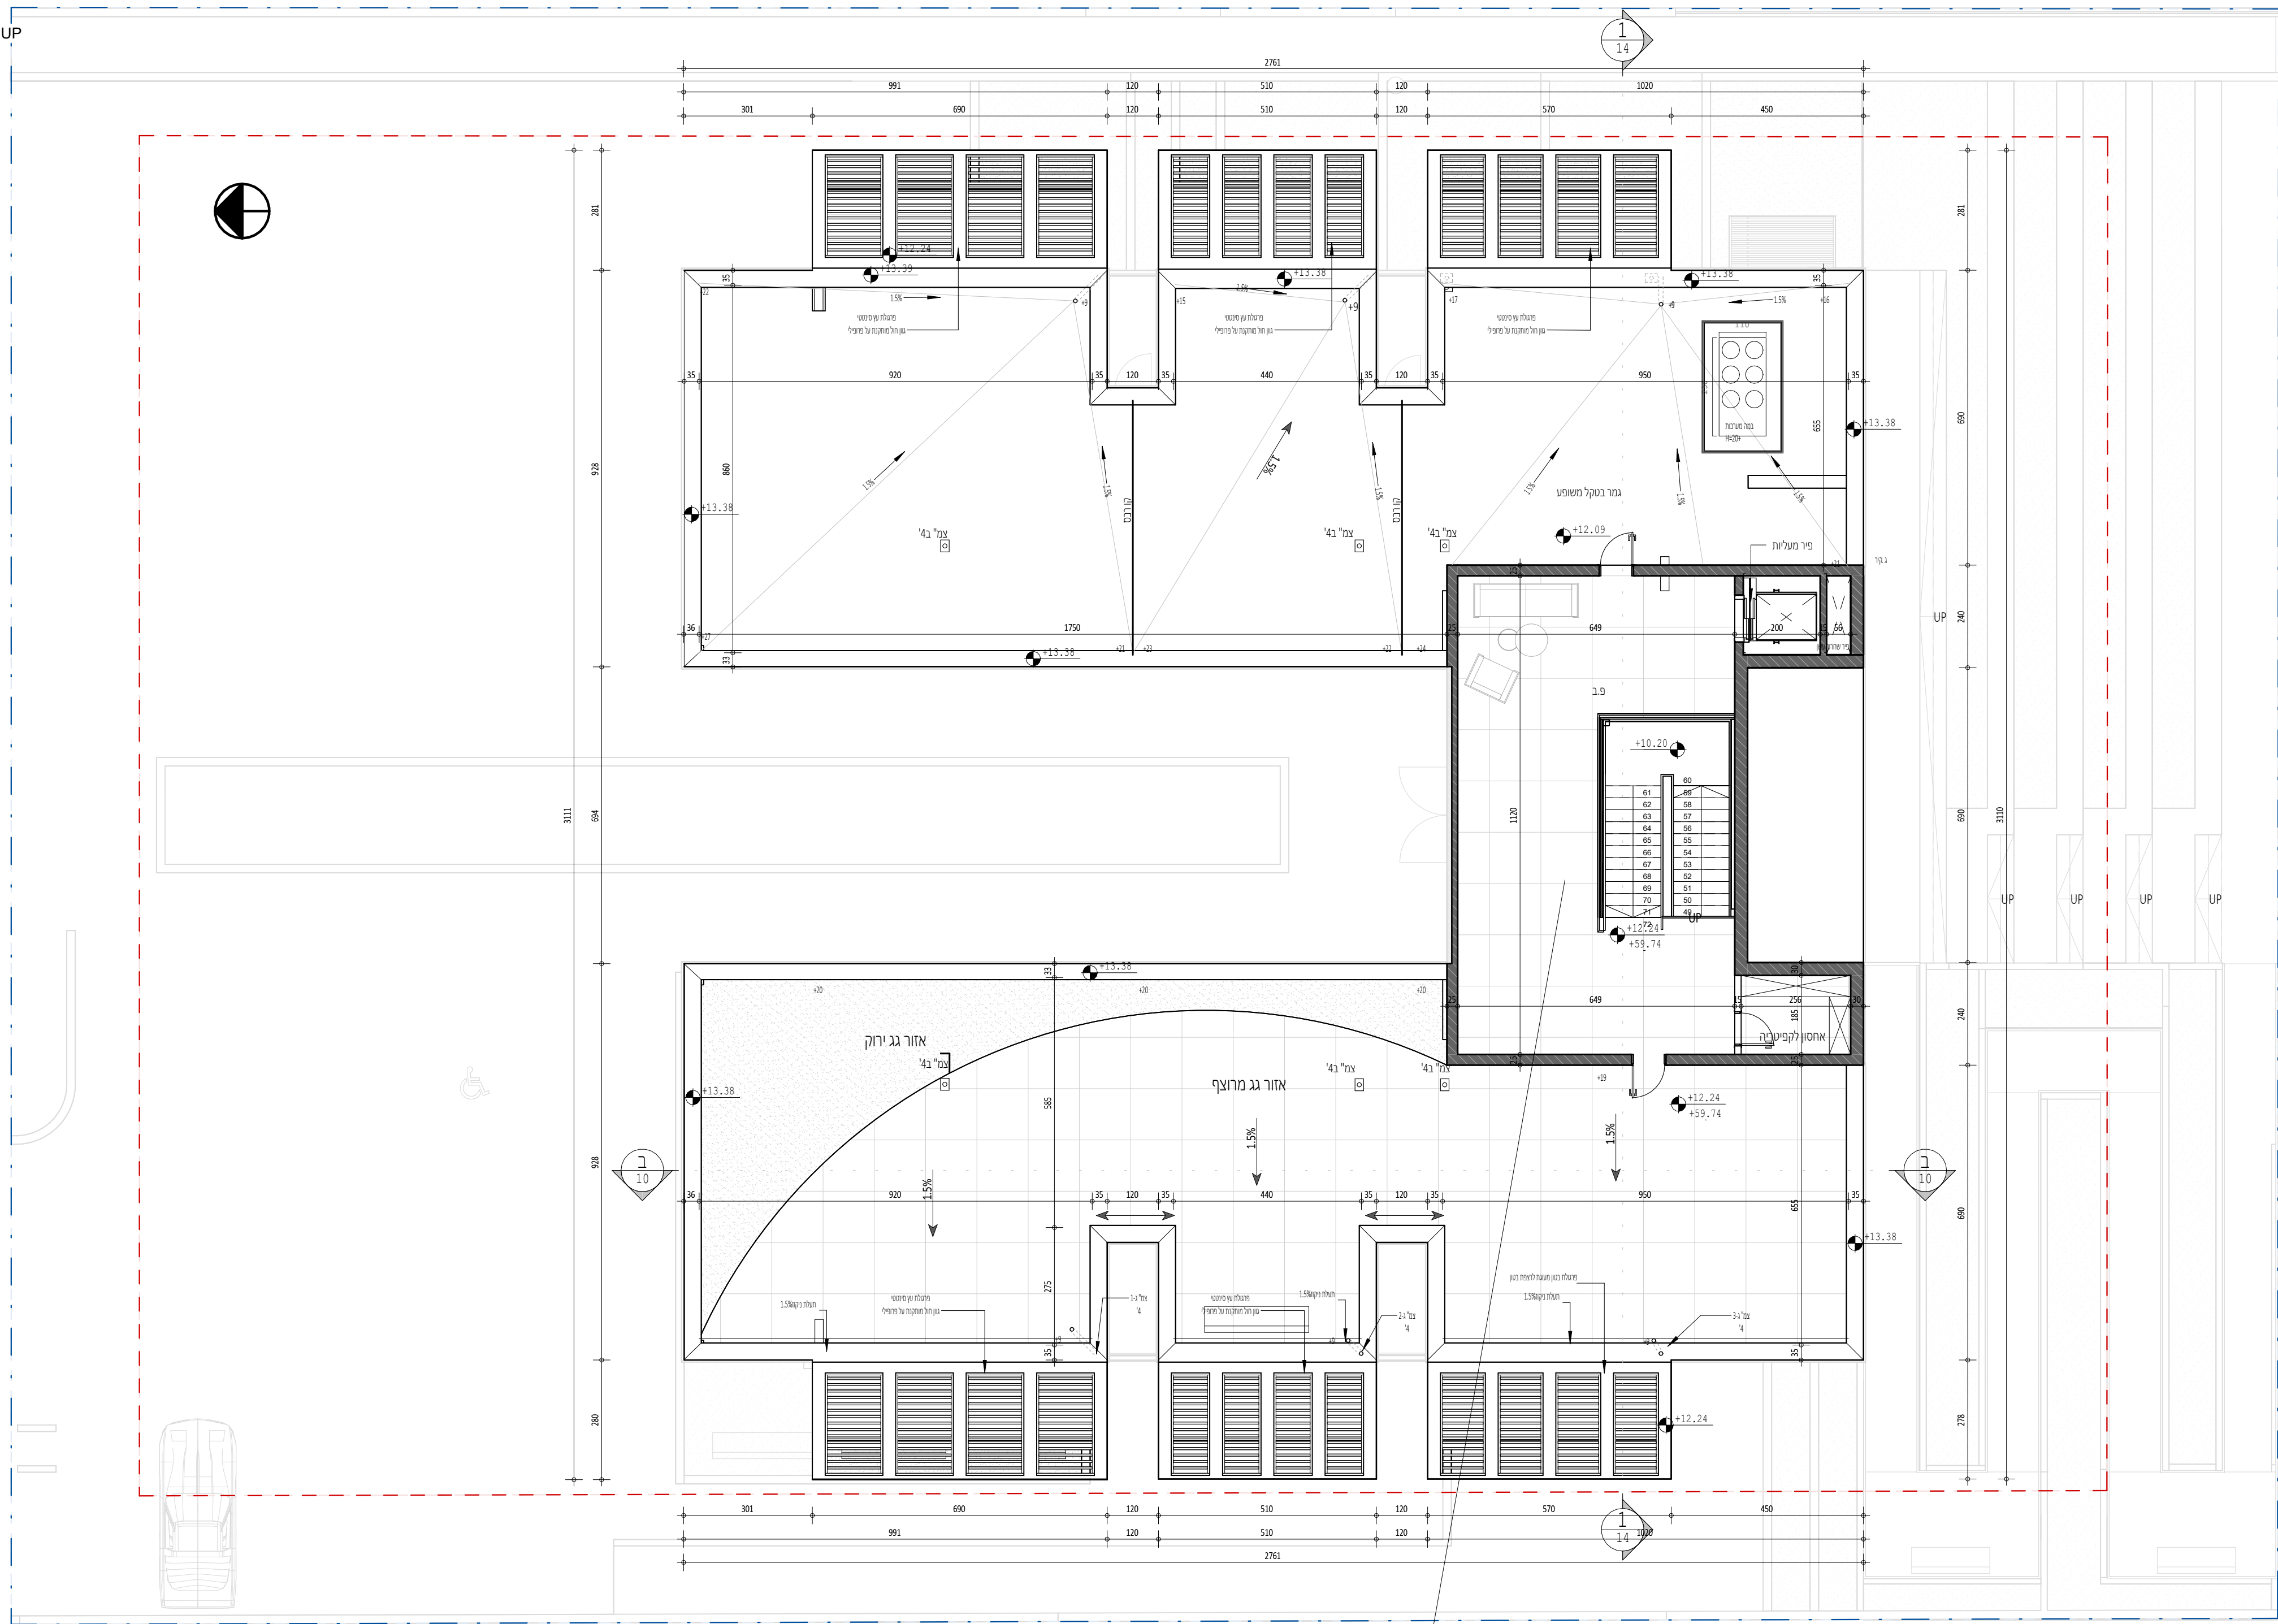

קומת גג שחזור לבן
1 : 100

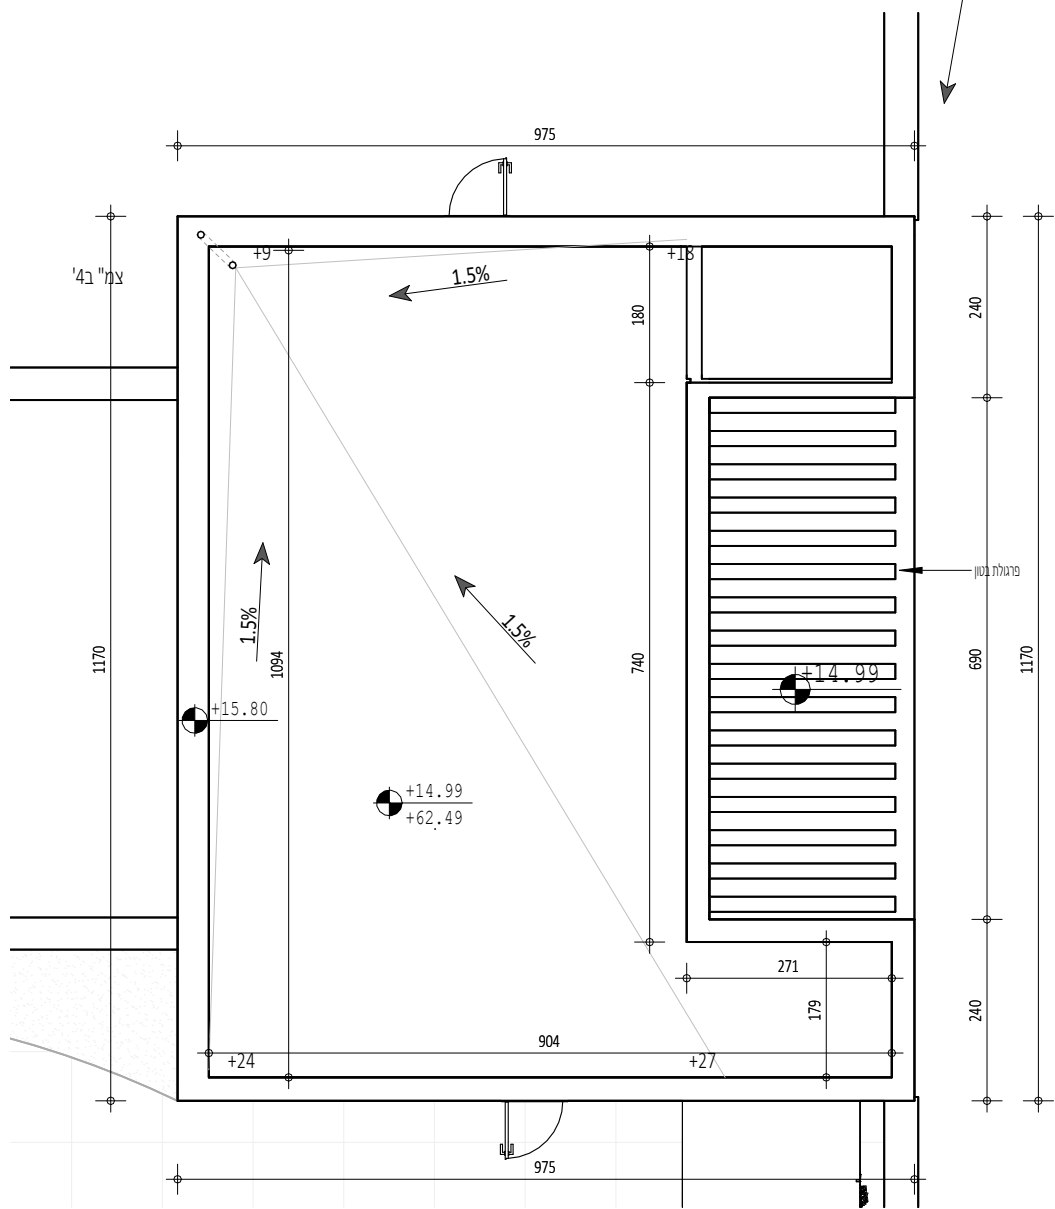

קומת גג עליונה
1 : 100

שם הפרויקט:

מעונות סטודנטים



מס'	תיאור גיליון:	ק"מ:
-00	שער	
-01	ניחוח סביבה	
-02	סקיצות פרוגרמה	
-03	הדמיות	

פיתוח שטח		
1:100	תכנית קומות קרקע	-04
1:100	תכנית קומה א	-05

תכניות שחור לבן		
1:100	תכנית קומות קרקע	-06
1:100	תכנית קומה א	-07
1:100	תכנית קומה ב	-08
1:100	תכנית גגות	-09

1:100	חתכים	-10
1:100	חיתות	-11
1:100	חיתות	-12

תכנית עבודה		
1:50	תכנית עבודה קומה א	-13
1:50	חתך א, א', ב'-ב'	-14
1:50	חזית צפונית, מערבית	-15

פרטי ביניים		
1:5	מדרגות-תכנית, פרטים	-16
1:20	מדרגות-חתכים	-17
1:20	קיר ייחודי-חתכים	-18
1:5	קיר ייחודי-פרטים	-19

עיצוב פנים		
1:50	תכנית ריהוט, רישוף	-20
1:50	תכנית חזקה פחית אזור	-21
1:50	הדמיות ופריסת קיר	-22
1:10	תכנון דלפק	-23
1:50	עיצוב חדר לדגמא	-24

קונסטרוקציה		
1:100	תכנית קונסטרוקציה	-25

מגיש/ה:

כרמל סעדון

שם ראש המגמה:


שרון גפני

שם המנחה:

לית'א


תאריך:

23\06\2026

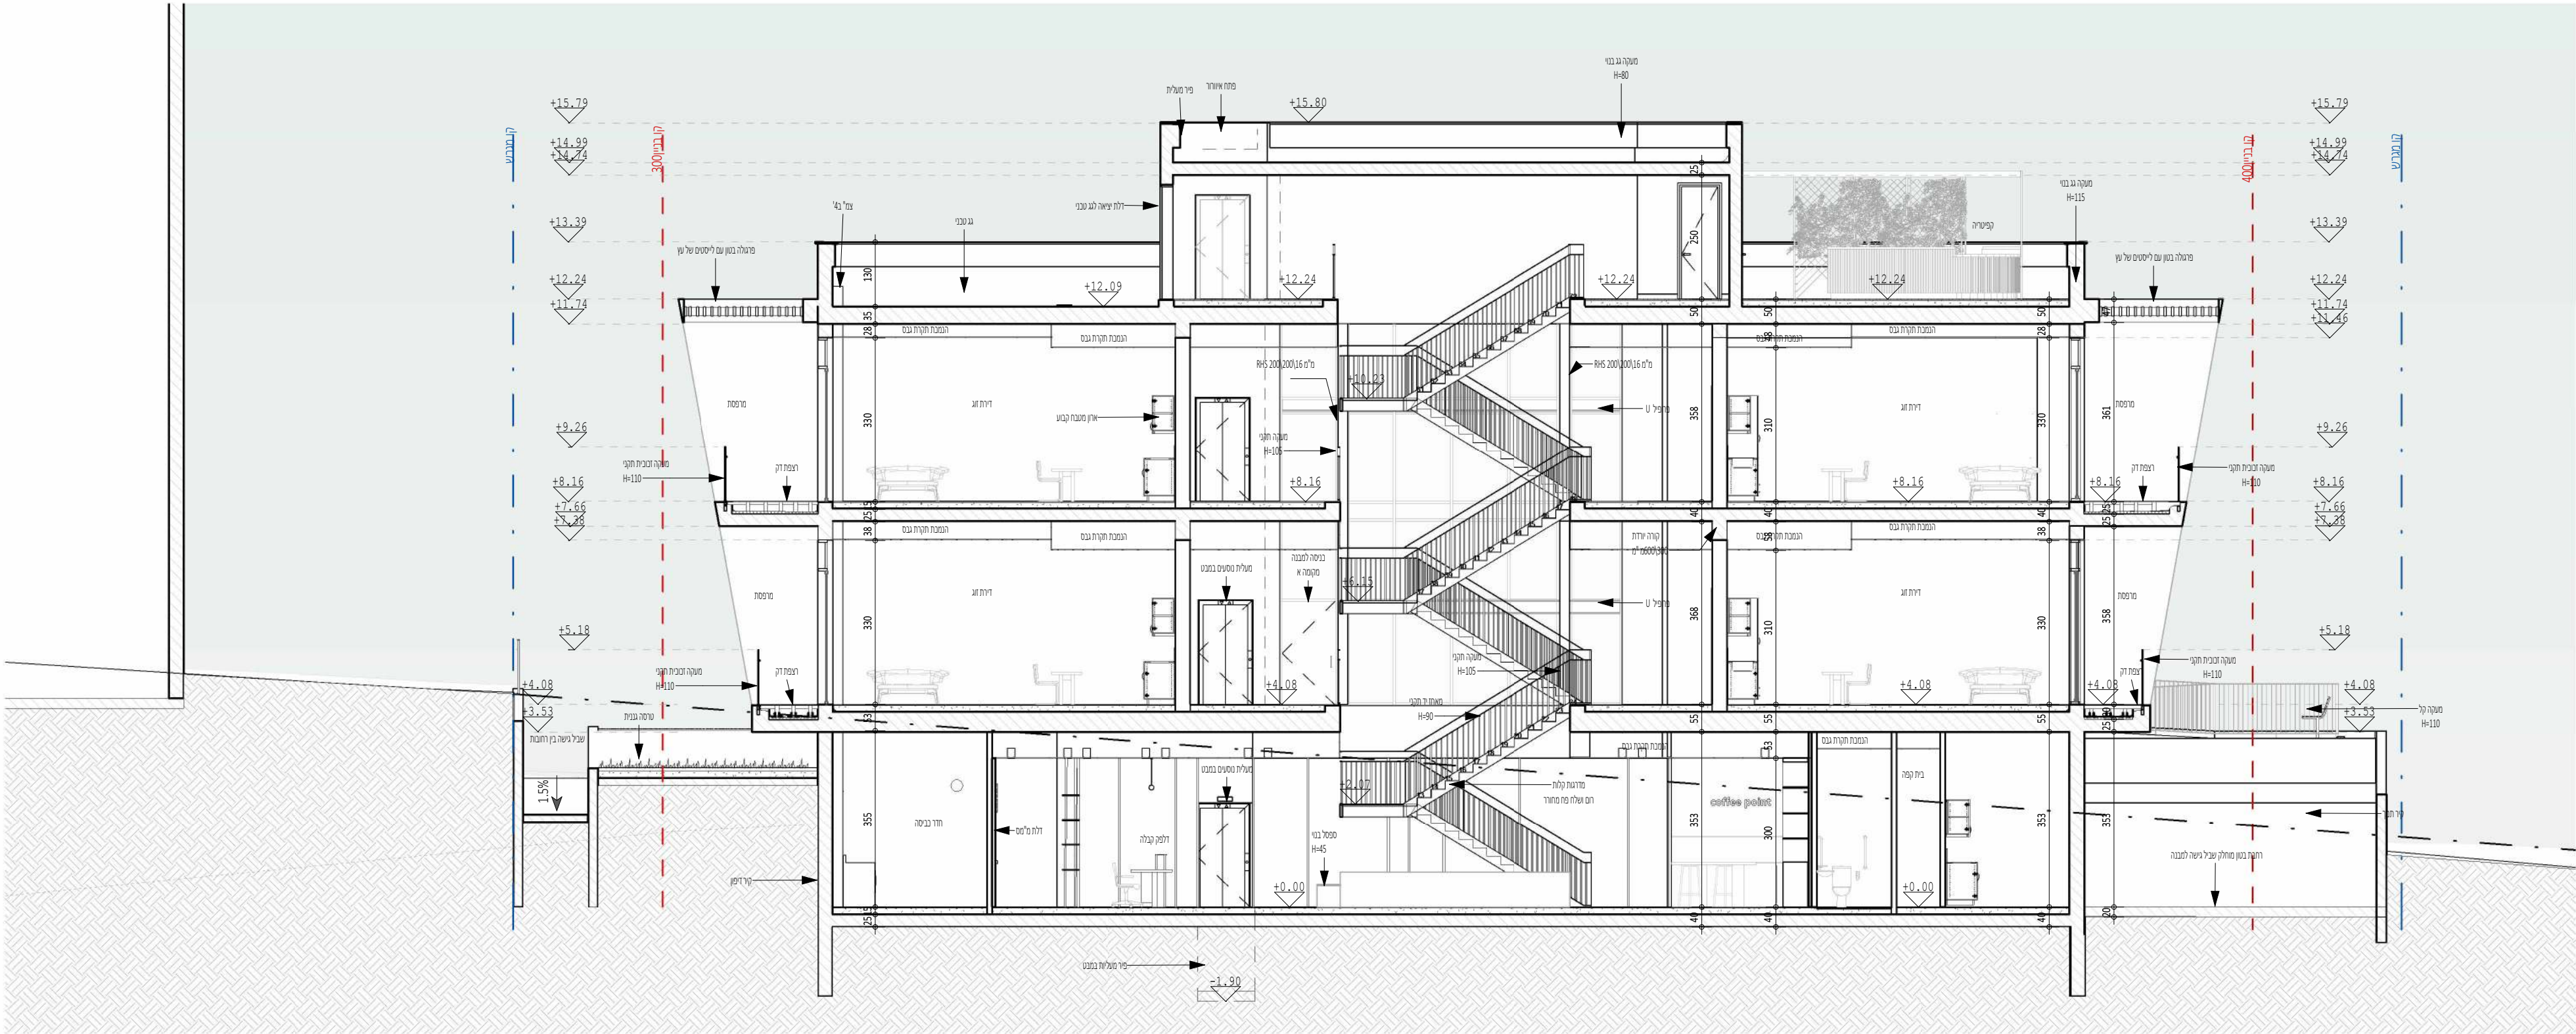

חתך א-א

1 : 100

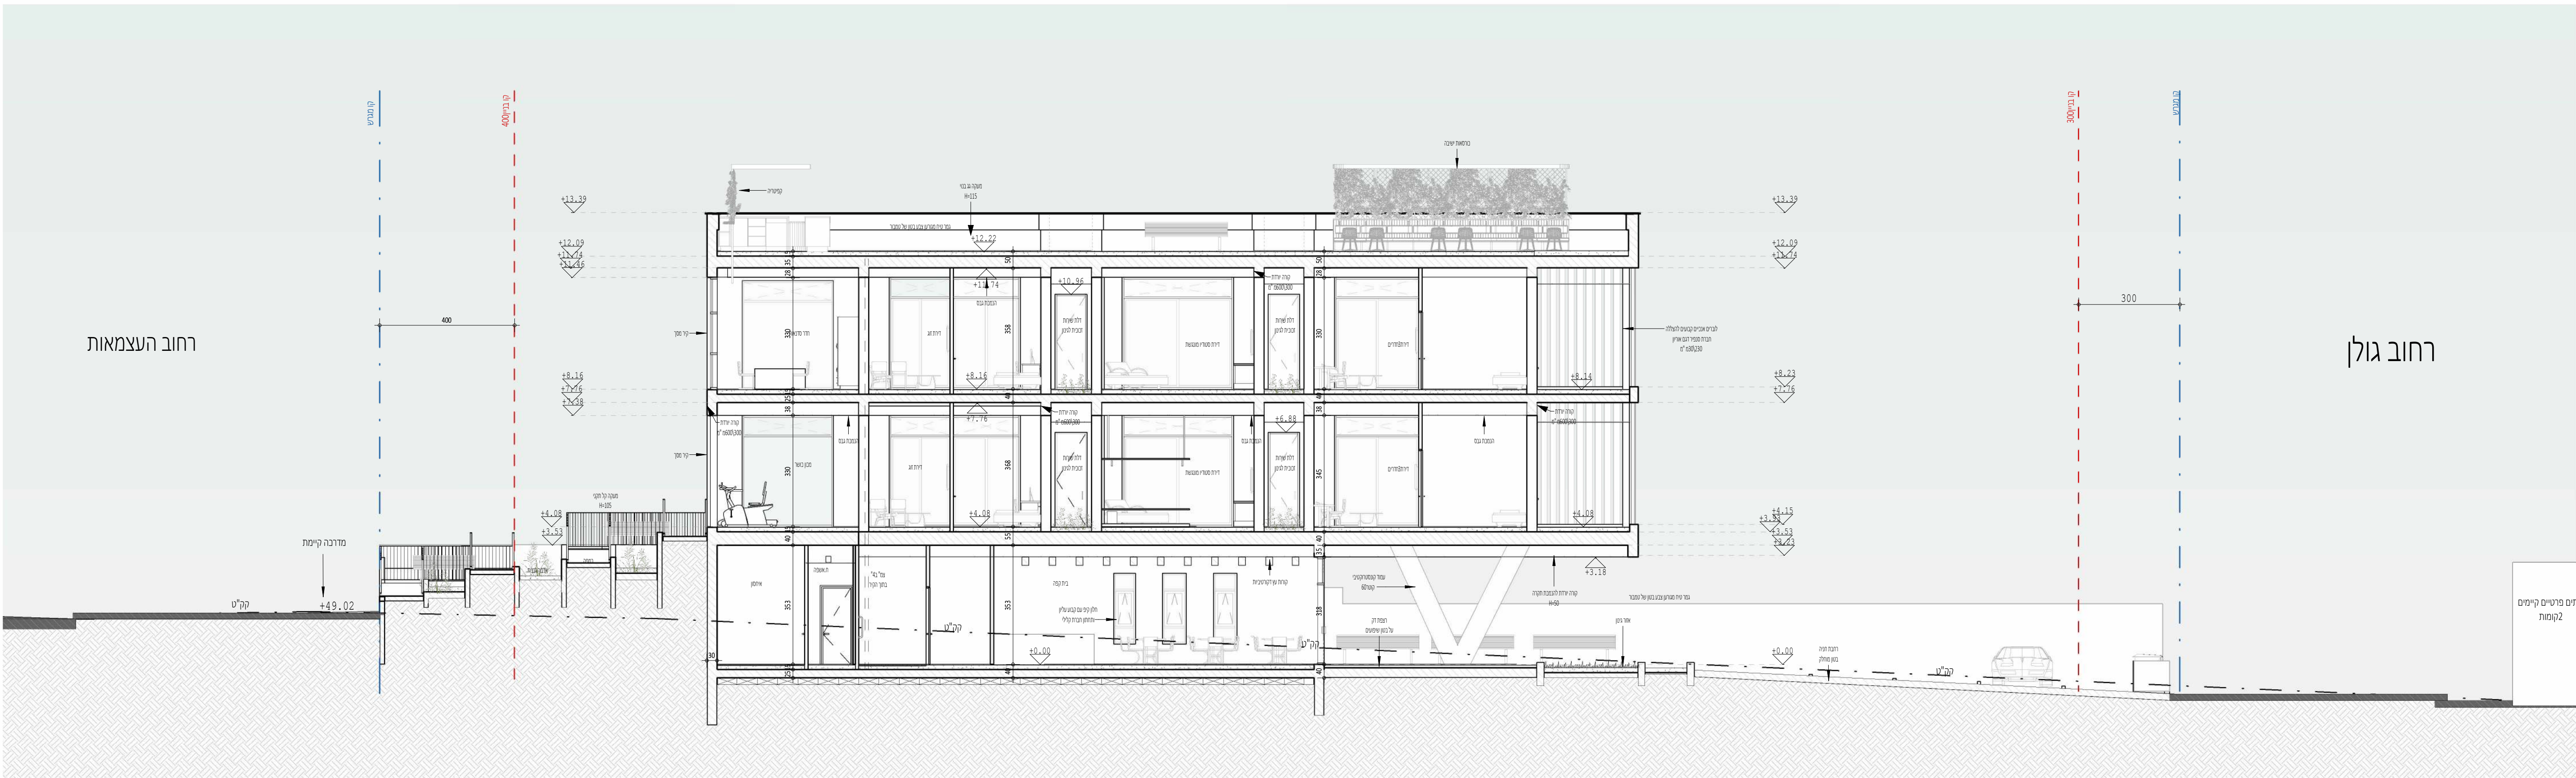

חתך ב-ב

1 : 100

שם הפרויקט:

מעונות סטודנטיים



מס'	תיאור גיליון:	קנ"מ:
-00	שער	
-01	ניתוח סביבה	
-02	סקיצות פרוגרמה	
-03	הדמיות	

פיתוח שטח		
1:100	תכנית קומת קרקע	-04
1:100	תכנית קומה א	-05

תכניות שטח לבן		
1:100	תכנית קומת קרקע	-06
1:100	תכנית קומה א	-07
1:100	תכנית קומה ב	-08
1:100	תכנית גגות	-09
1:100	חתכים	-10
1:100	חיתות	-11
1:100	חיתות	-12

תכנית עבודה		
1:50	תכנית עבודה קומה א	-13
1:50	חתך א-א', ב-ב'	-14
1:50	חזית צפונית, מערבית	-15

1:5	1:20	מדרגות-תכניות, פרטים	-16
	1:20	מדרגות-חתכים	-17
	1:20	קיר ייחודי-חתכים	-18
	1:5	קיר ייחודי-פרטים	-19

עיצוב פנים		
1:50	תכנית ריהוט, ריצוף	-20
1:50	תכנית חקירה ומיזוג אוויר	-21
1:50	הדמיות ופריסת קיר	-22
1:10	1:20 תכנון דלפק	-23
1:50	עיצוב חדר לדוגמא	-24

קונסטרוקציה		
1:100	תכנית קונסטרוקציה	-25

מגיש/ה:

כרמל סעדון

שם ראש המגמה:

שרון גפני

שם המנחה:



לית'א

תאריך:

23\06\2026

צפוןית פרזנטטיבי

1 : 100

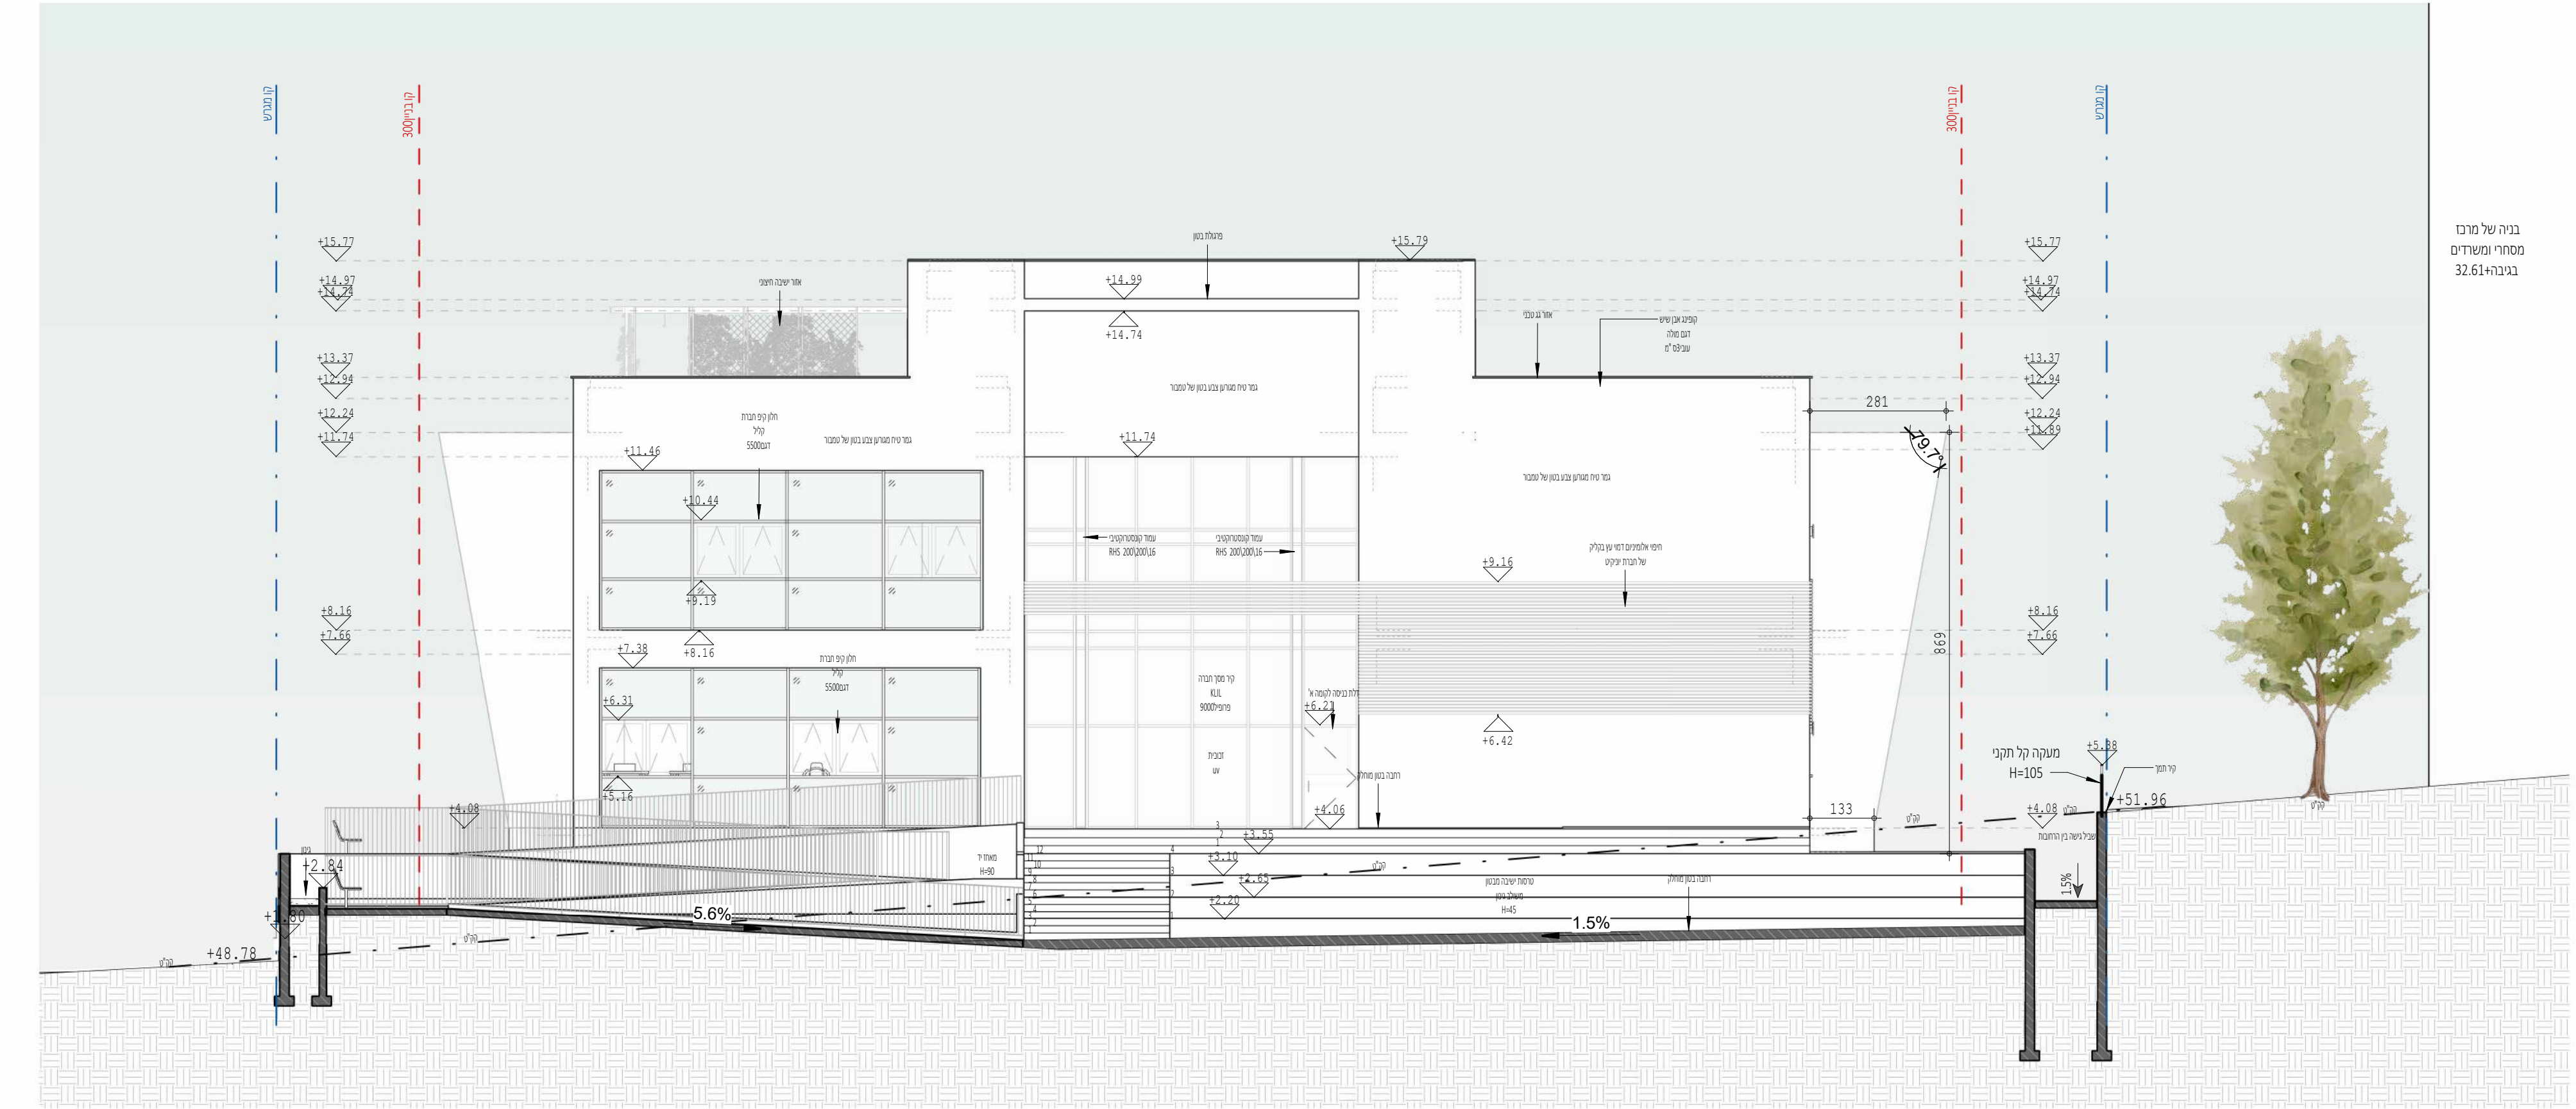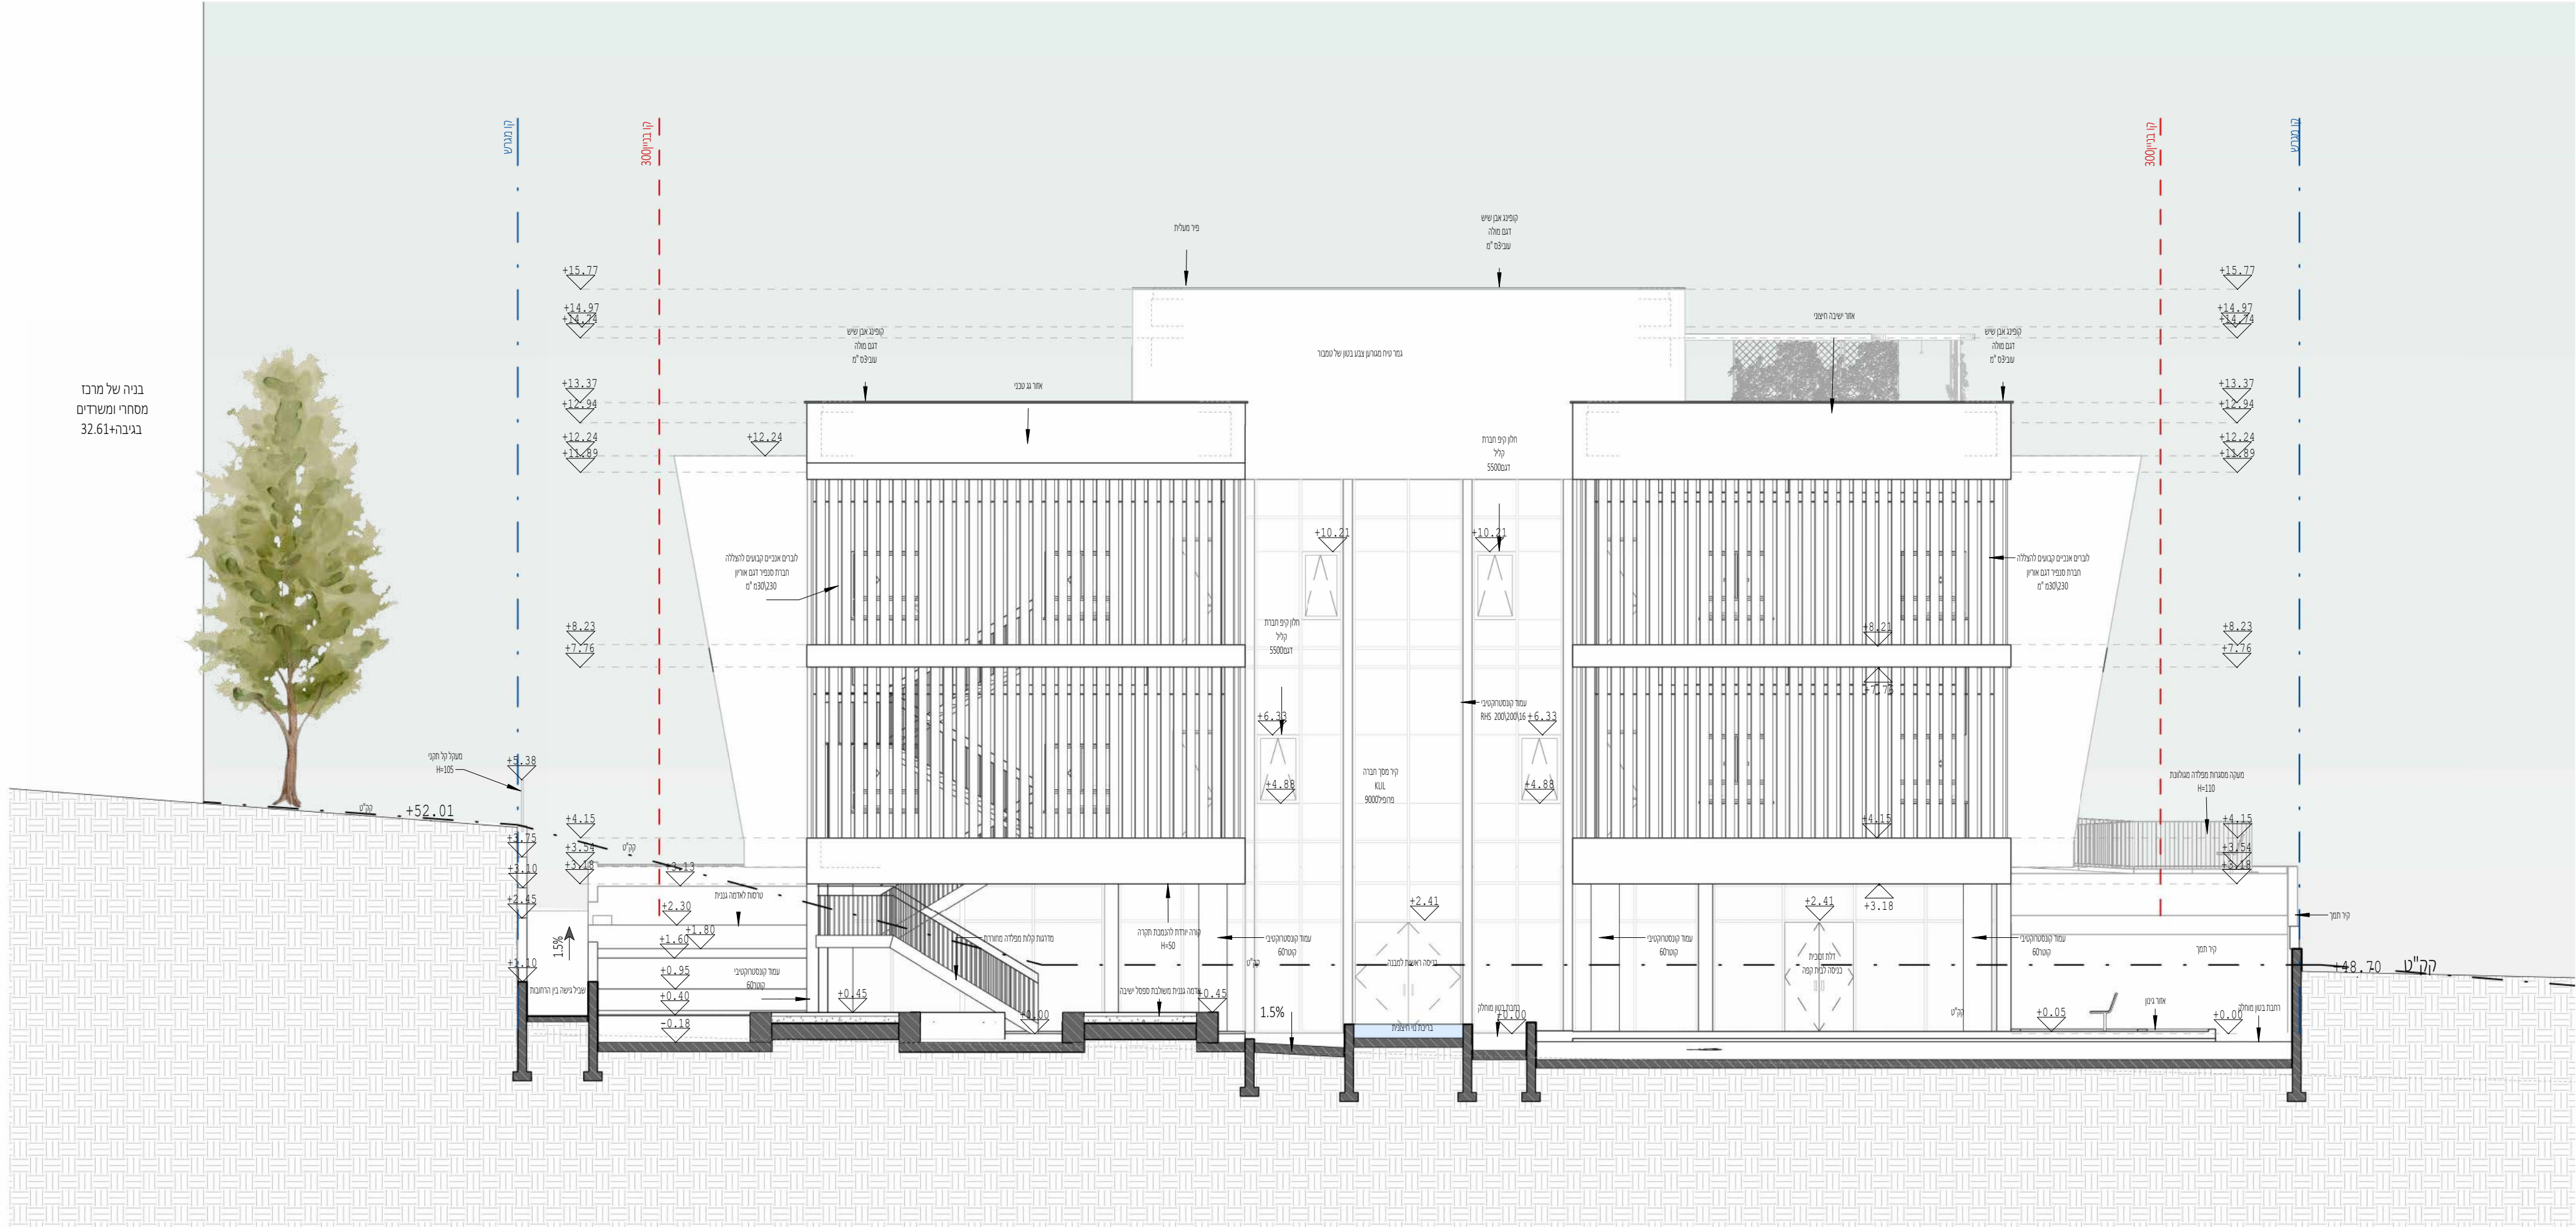

דרומית פרזנטטיבי

1 : 100

שם הפרויקט:

מעונות סטודנטיים



מס'	תיאור גיליון:	קמ"מ:
-00	שער	
-01	ניתוח סביבה	
-02	סקיצות פרוגרמה	
-03	הדמיות	

פיתוח שטח	1:100
-04 תכנית קומת קרקע	
-05 תכנית קומה א	1:100

תכניות שחור לבן	1:100
-06 תכנית קומת קרקע	
-07 תכנית קומה א	1:100
-08 תכנית קומה ב	1:100
-09 תכנית גגות	1:100
-10 חתכים	1:100
-11 חזיתות	1:100
-12 חזיתות	1:100

תכנית עבודה	1:50
-13 תכנית עבודה קומה א	
-14 חתך א-א', ב-ב'	1:50
-15 חזית צפונית, מערבית	1:50

פרטי ביין	1:5
-16 מדרגות-תכנית, פרטים	1:20
-17 מדרגות-חתכים	1:20
-18 קיר ייחודי-חתכים	1:20
-19 קיר ייחודי-פרטים	1:5

עיצוב פנים	1:50
-20 תכנית ריהוט, רישוף	
-21 תכנית חקירה שחור ואדום	1:50
-22 הדמיות ופריסת קיר	1:50
-23 תכנון דלפק	1:10
-24 עיצוב חדר לדוגמה	1:50

קונסטרוקציה	1:100
-25 תכנית קונסטרוקציה	

מגיש/ה:

כרמל סעדון

שם ראש המגמה:


שרון גפני

שם המנחה:

לית'

תאריך:

23\06\2026

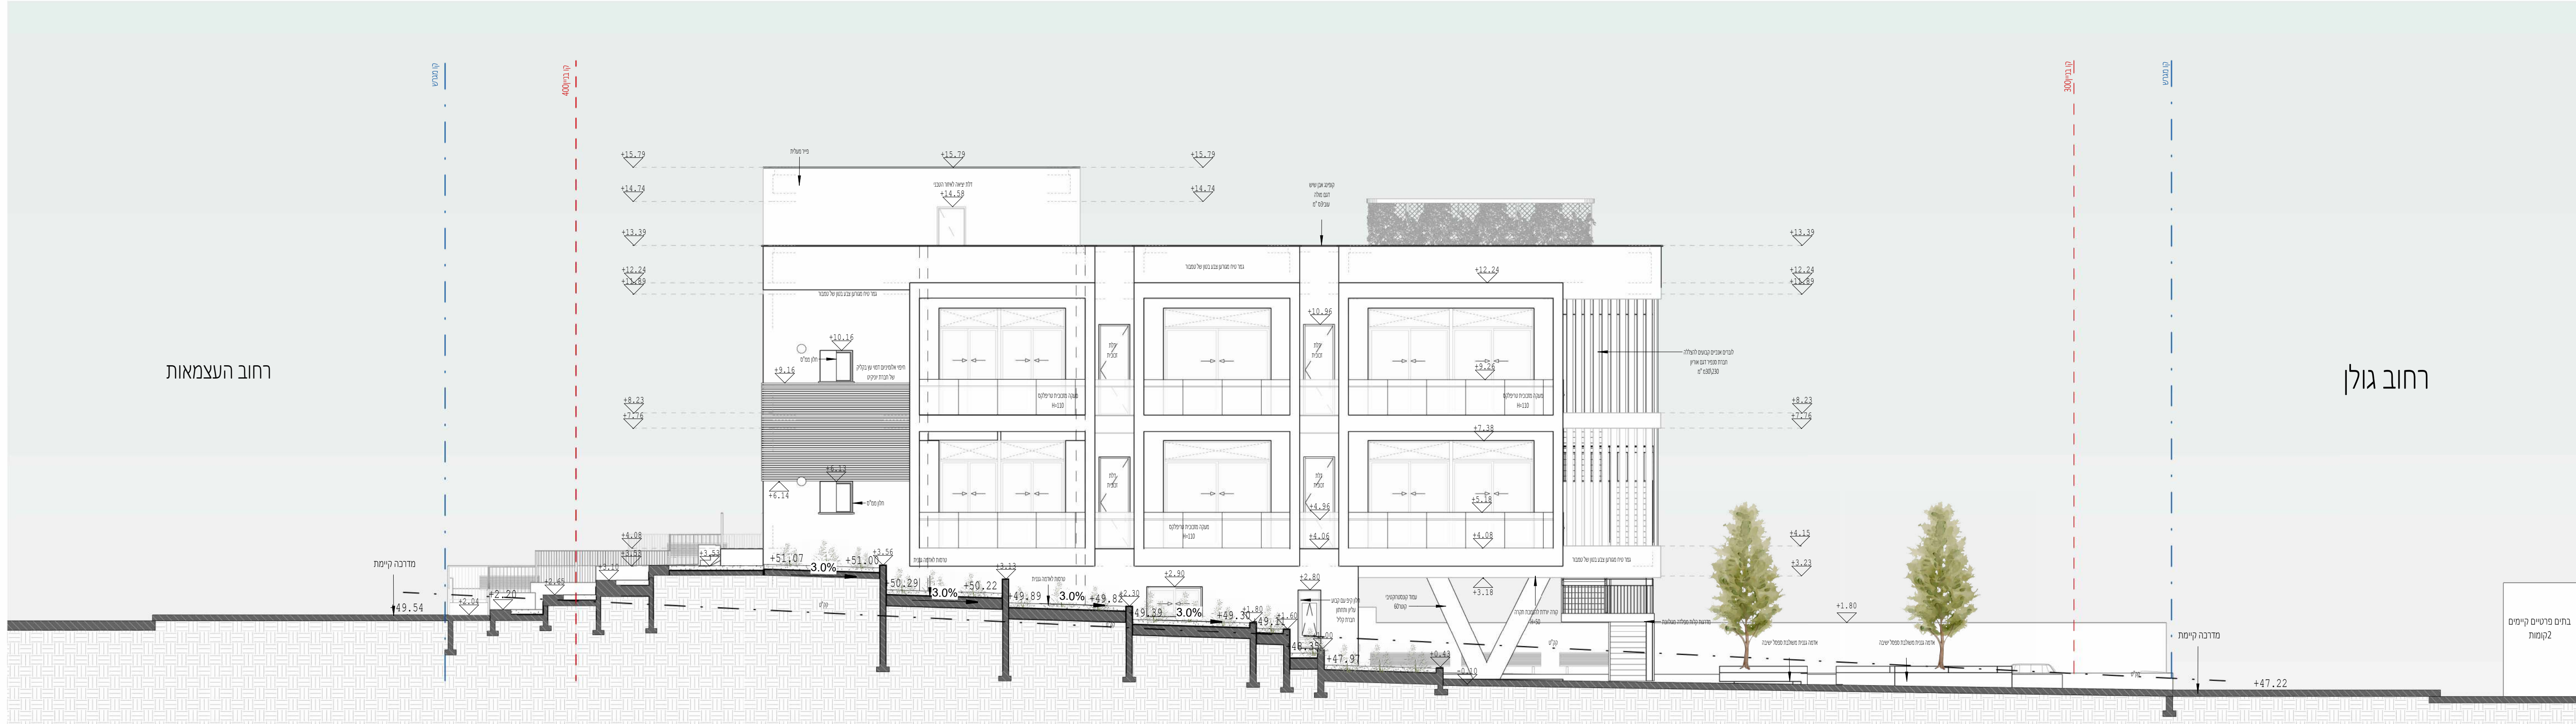

מזרחית פרזנטטיבי

1 : 100



מערבית פרזנטטיבי

1 : 100




מס'	מ"אור גיליון:	קניית:
-00	טער	
-01	ניחוח כבינה	
-02	סקיצות -פרורמה	
-03	הדמיות	

פירוט שטח		
1:100	תכנית קומת קרקע	-04
1:100	תכנית קומה א	-05
תכניות שטח לבן		
1:100	תכנית קומת קרקע	-06
1:100	תכנית קומה א	-07
1:100	תכנית קומה ב	-08
1:100	תכנית גגות	-09
1:100	חזכים	-10
1:100	חחיות	-11
1:100	חחיות	-12

תכניות עבודה		
1:50	תכנית עבודה קומה א	-13
1:50	חקר א'-א',כ'-כ'	-14
1:50	חזית צפונית, מערבית	-15
פרט בוויזן		
1:5 1:20	מדרגות-תכנית, פרטים	-16
1:20	מדרגות-תחכים	-17
1:20	קיר ייחודי-תחכים	-18
1:5	קיר ייחודי-פרטים	-19
עיצוב פנים		
1:50	תכנית ריהוט, ריצוף	-20
1:50	תכנית הקומה וסיווג אזורי	-21
1:50	הדמיות ופריסת קיר	-22
1:10 1:20	תכנון דלפק	-23

קונסטרוקציה		
1:100	תכניות קונסטרוקציה	-24

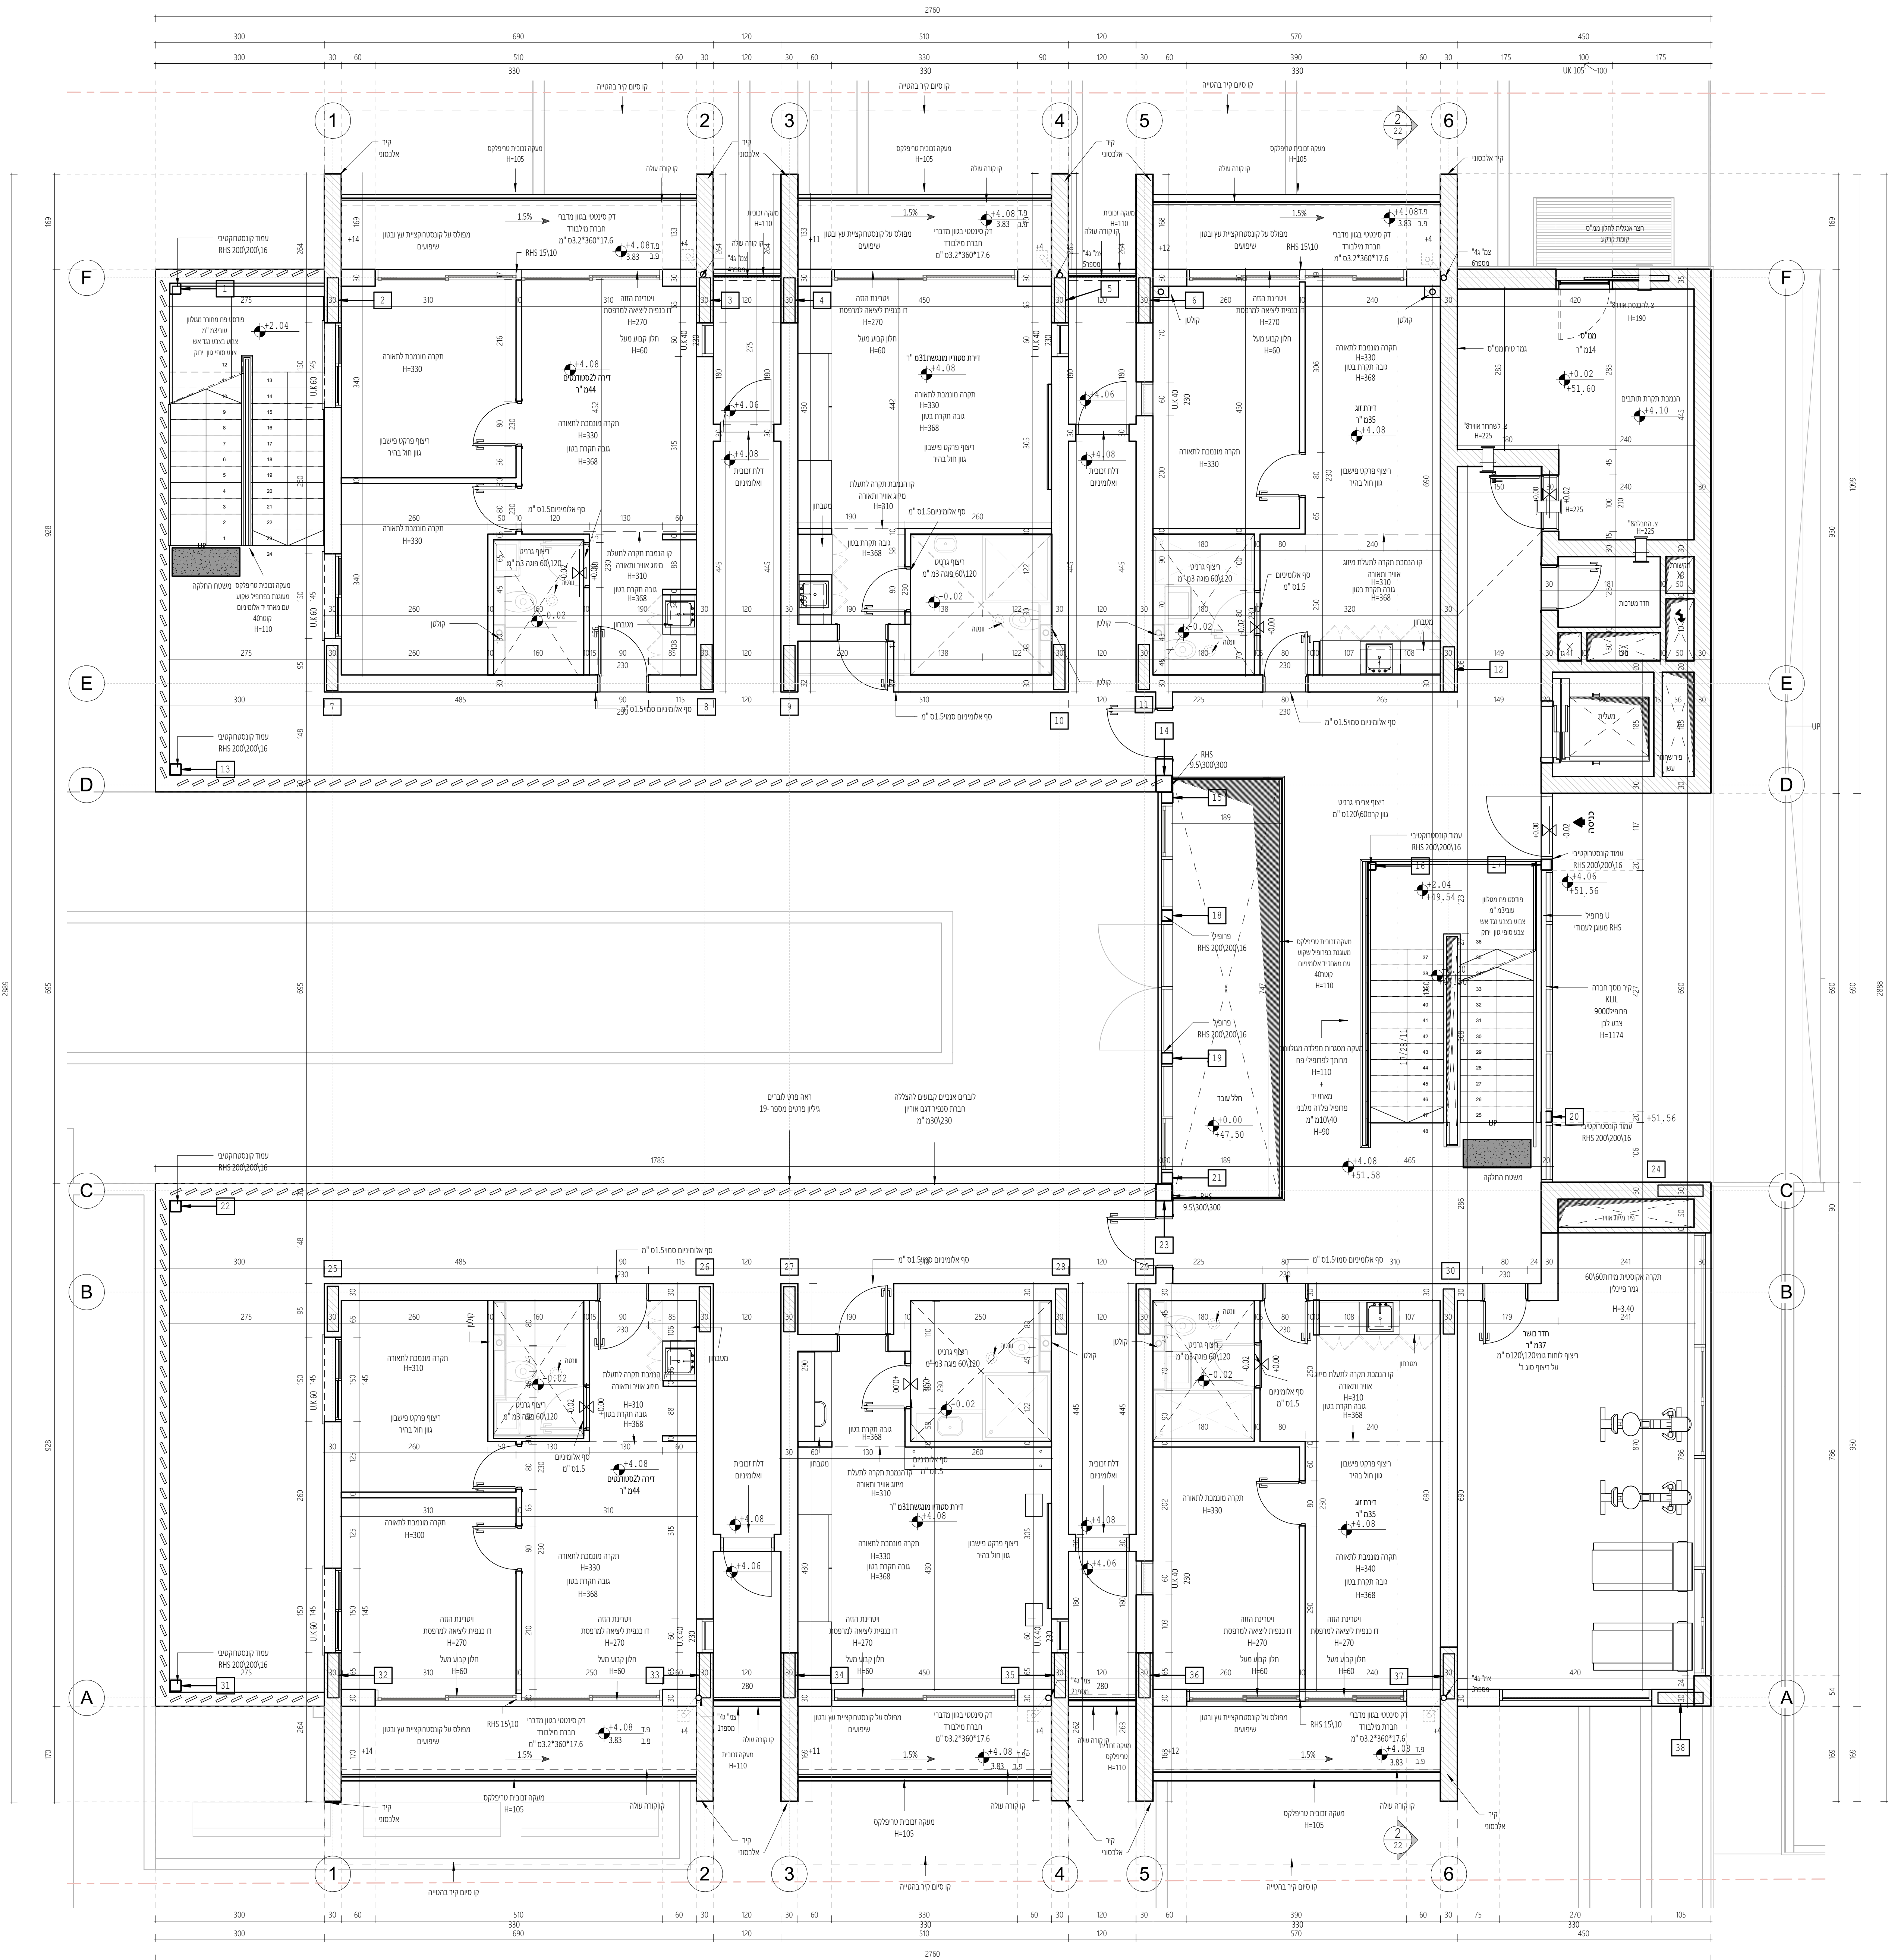

מגישה:

כרמל טעדון

שם ראש המגמה:

שרון גפני

שם המנחה:

ליית'



תאריך:

23\06\2026

שם הפרויקט:
מעונות טיפוליים



מס'	מ'אור גיליון:	קניית:
-00	טער	
-01	גיתות סביבה	
-02	סקיצות פרויקט	
-03	הדמיות	
פירוט שטח		
-04	הכנית קומת קרקע	1:100
-05	הכנית קומת א'	1:100
הכניות מסור לבן		
-06	הכנית קומת קרקע	1:100
-07	הכנית קומת א'	1:100
-08	הכנית קומת ב'	1:100
-09	הכנית גגות	1:100
-10	החכים	1:100
-11	חיתומות	1:100
-12	חיתומות	1:100
הכניות עבודה		
-13	הכנית עבודה קומת א'	1:50
-14	תוכן א'-א', ב'-ב'	1:50
-15	חזית צפוןית, מערבית	1:50
פרט בניין		
-16	מדרגות-הכניות, פרטים	1:5 1:20
-17	מדרגות-חכים	1:20
-18	קיר ייחודי-חכים	1:20
-19	קיר ייחודי-פרטים	1:5
שיעור פנים		
-20	הכנית ריהוט, ריצוף	1:50
-21	הכנית קומת סיווג אוויר	1:50
-22	הדמיות ופריסת קיר	1:50
-23	הכנית דלפק	1:10 1:20
קונסטרוקציה		
-24	הכניות קונסטרוקציה	1:100

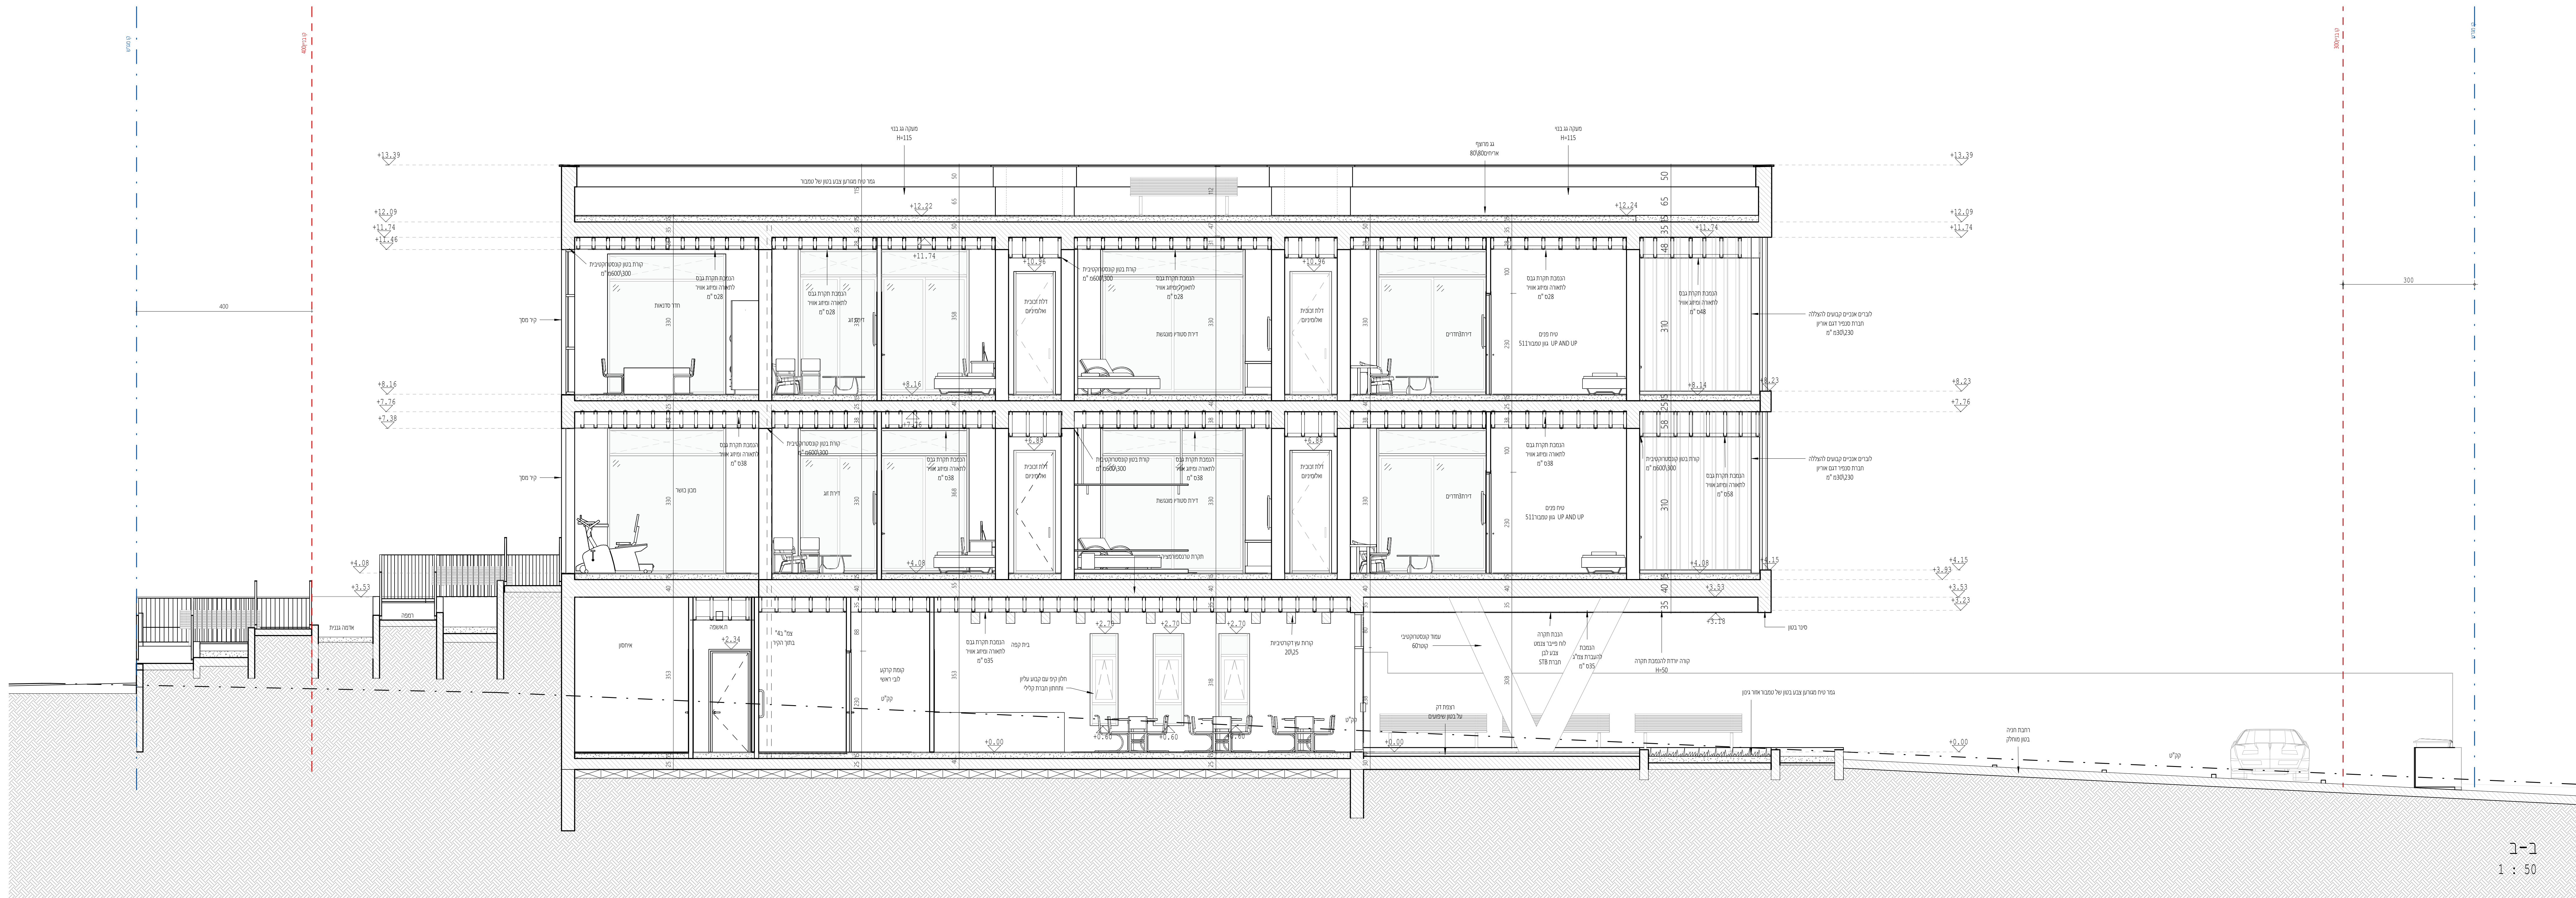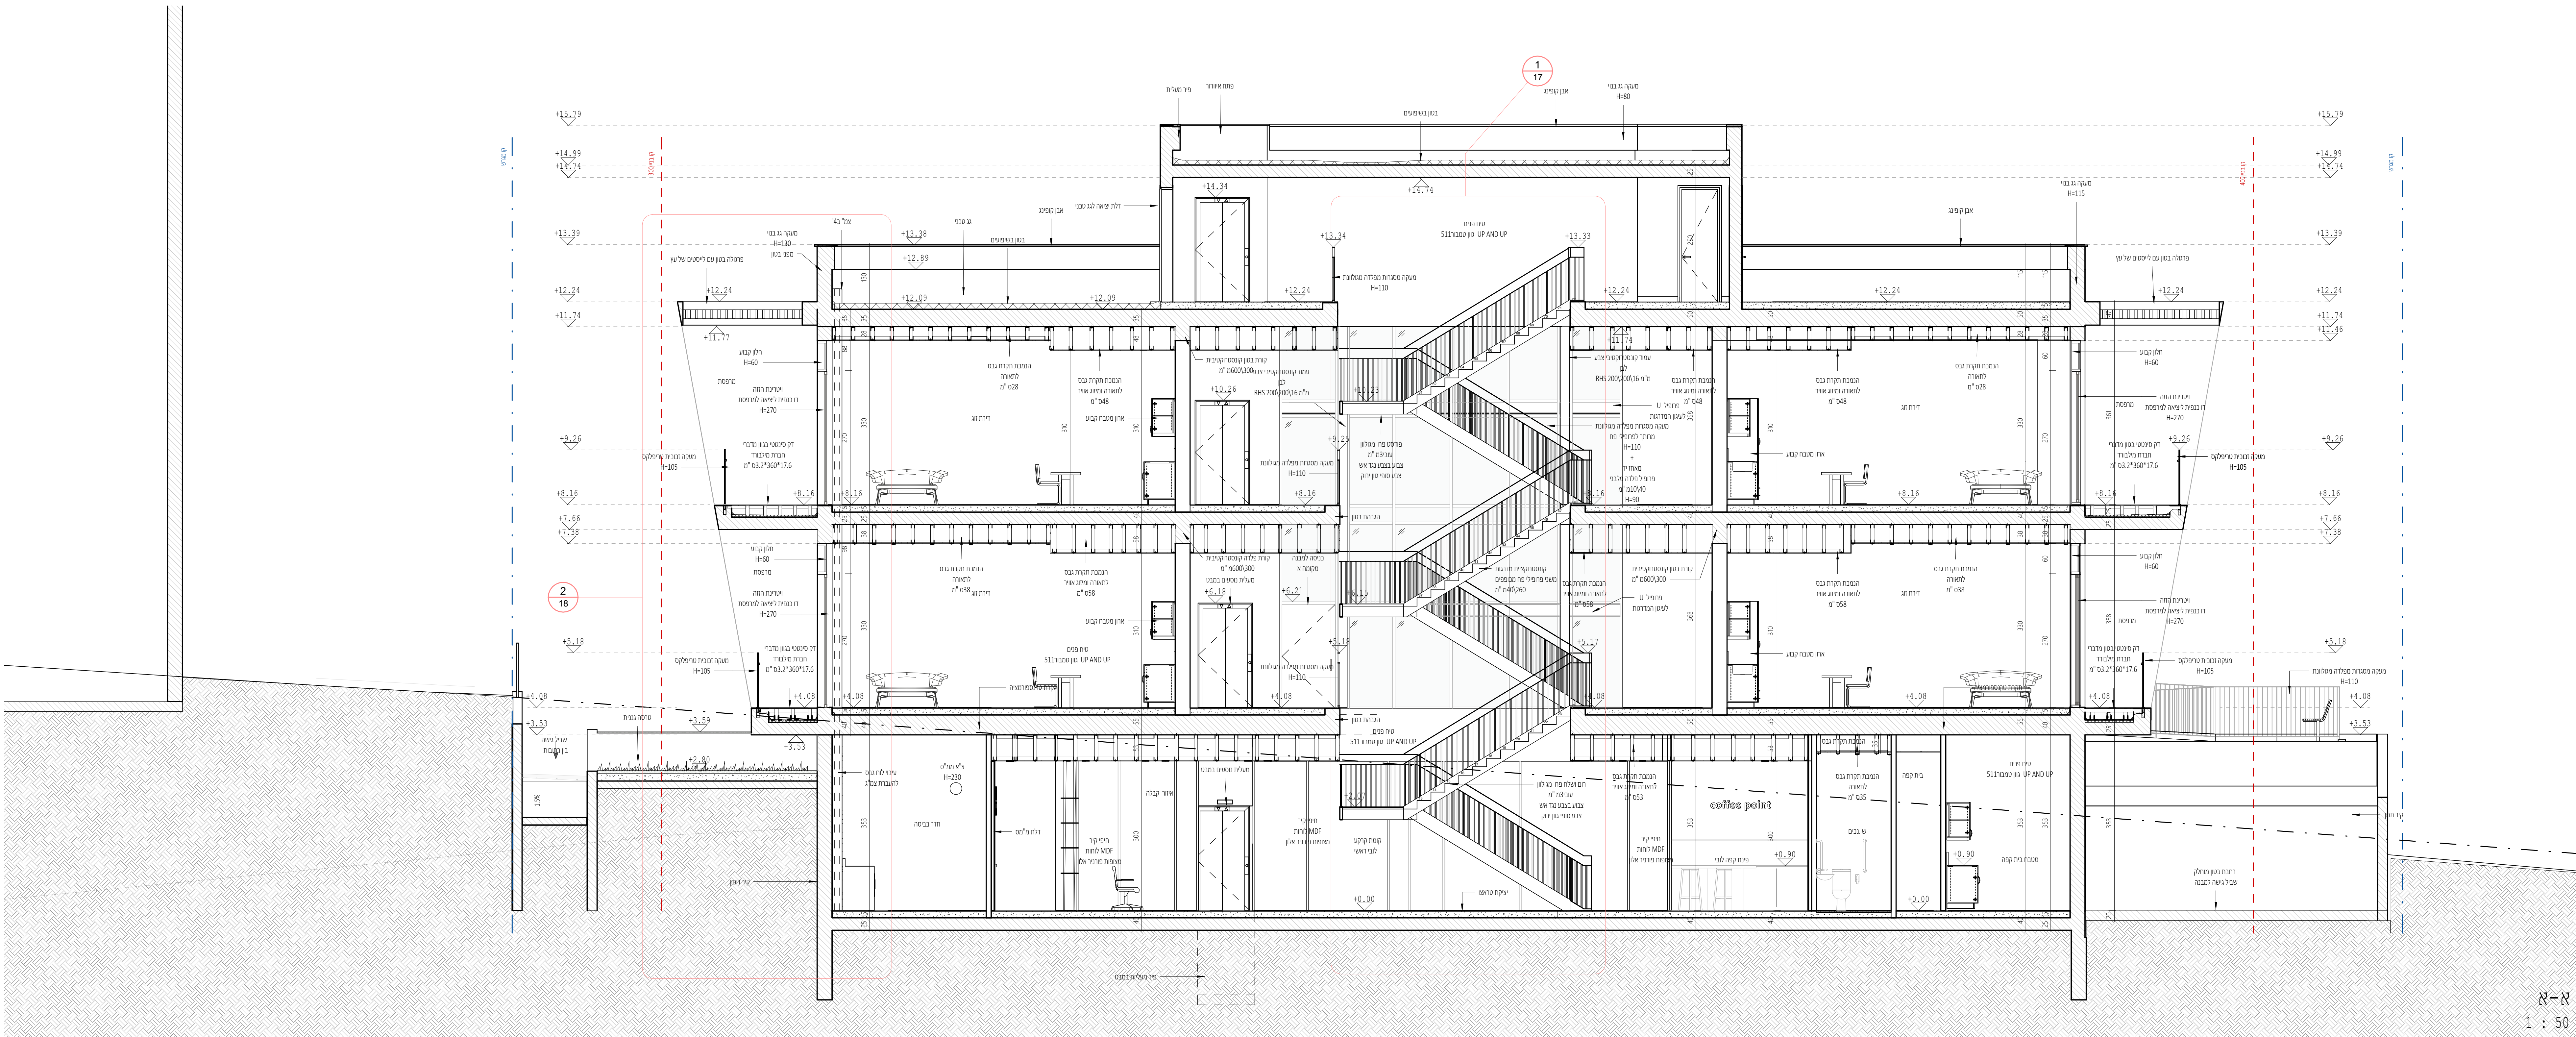

שם הפרויקט:
מעונות סטודנטים



מס'	מ'אור גיליון:	קנייט:
-00	טער	
-01	גיתוח כביה	
-02	סקיפיות -פרוגרמה	
-03	הדמיות	

פירוט שטח
-04 הכנית קומת קרקע
-05 הכנית קומה א


תכניות שטח לבן
-06 הכנית קומת קרקע
-07 הכנית קומה א
-08 הכנית קומה ב
-09 הכנית גנות
-10 חתכים
-11 חתומות
-12 חתומות

תכנית עבודה
-13 תכנית עבודה קומה א
-14 תכנית א"א, ב"ב
-15 חזית צפוןית, מערבית

פרוי בוי"ו
-16 מדרגות-תכנית, פרטים
-17 מדרגות-חתכים
-18 קיר ייחודי-חתכים
-19 קיר ייחודי-פרטים
עיצוב פנים
-20 תכנית ריהוט, ריצוף
-21 תכנית תקרה וריפוד אנודי
-22 הדמיות ופריסת קיר
-23 תכנון דלפק

קונסטרוקציה
-24 תכנית קונסטרוקציה

חזית צפוןית
1 : 50

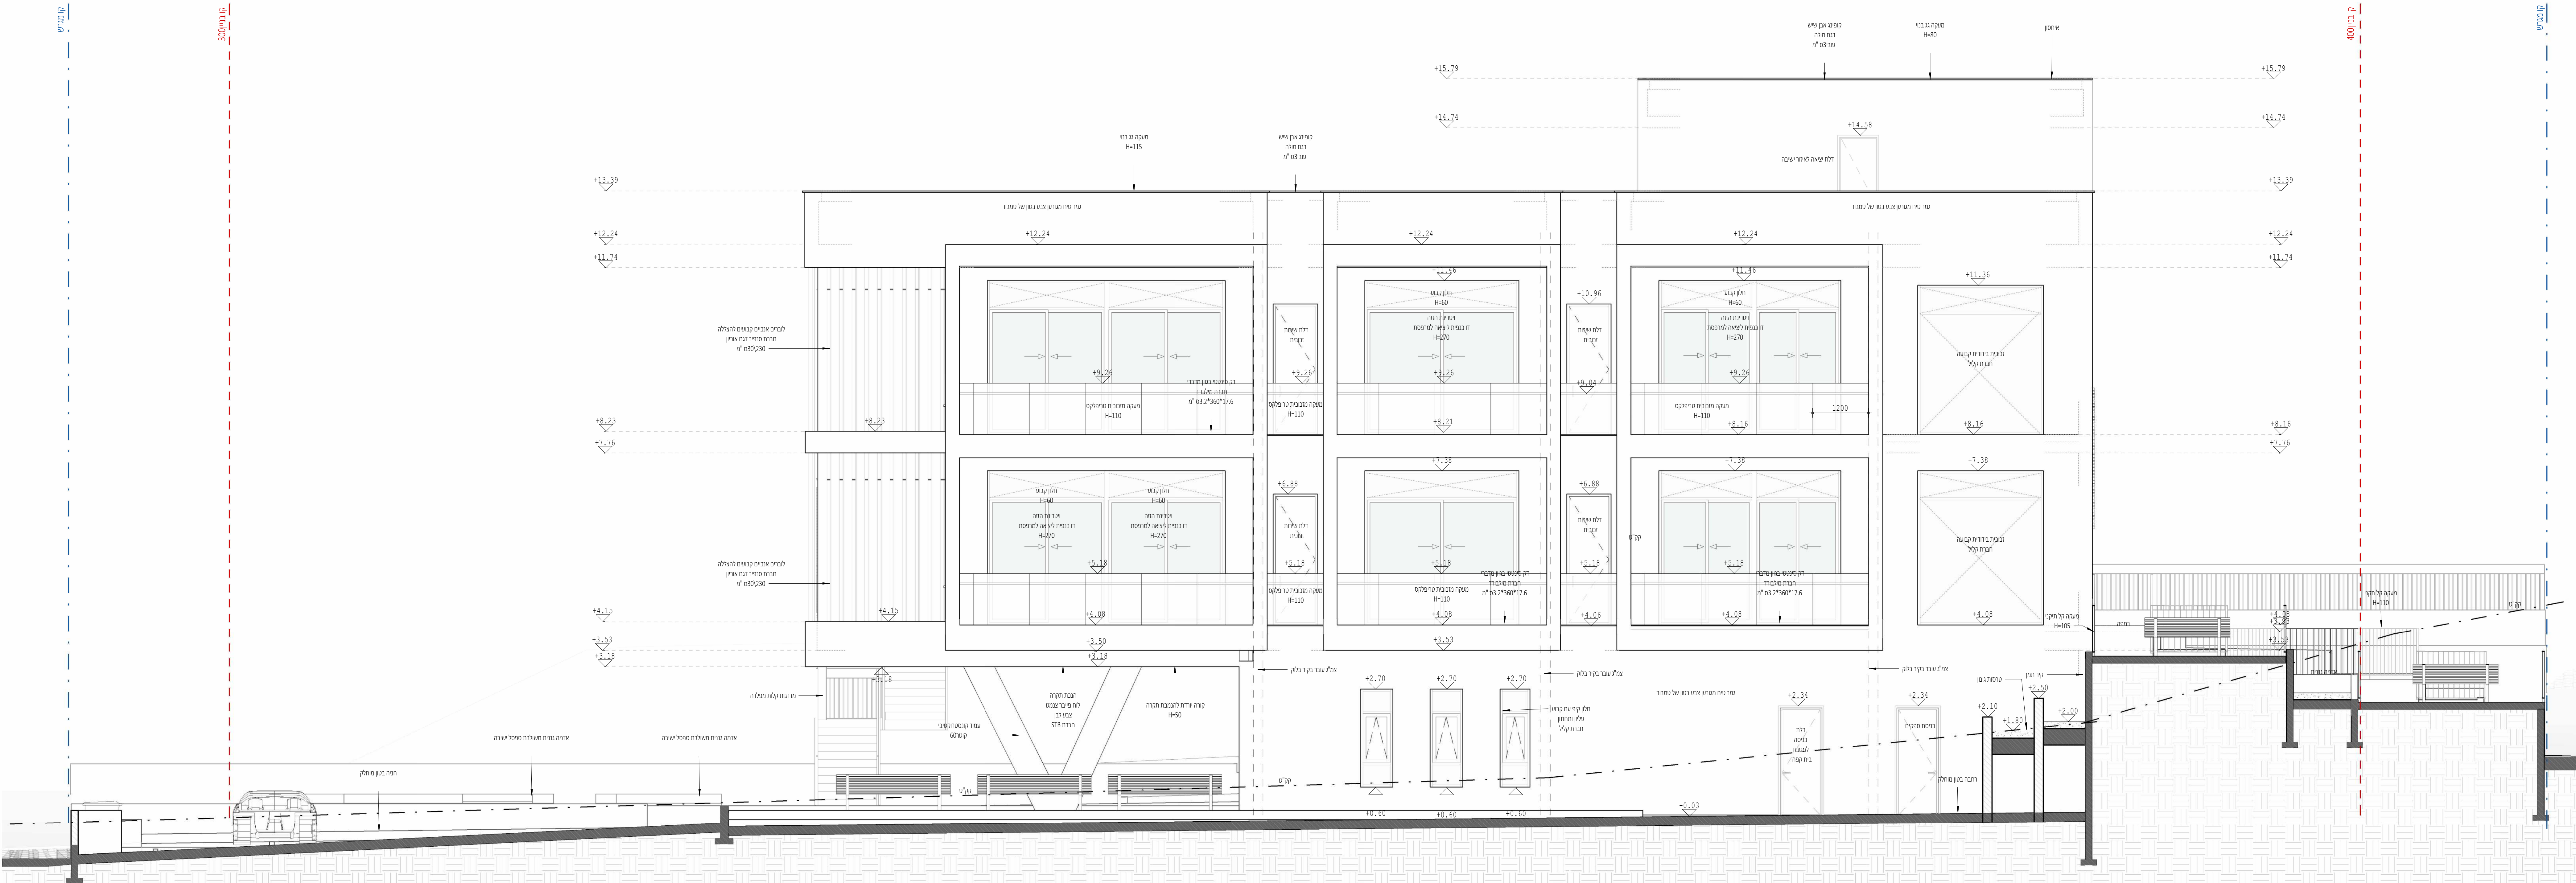

חזית מערבית
1 : 50

מגיש/ה:

כרמל סעדון

שם ראש המגמה:

שרון גפני

שם המנחה:

לייט'


תאריך:

23\06\2026


שם הפרויקט:
מעונות סטודנטים




מס'	מ"אור גיליון:	קניית:
-00	שטר	
-01	ניתוח כביב	
-02	סקיצות -פרוגמה	
-03	הדמיות	
פירוט שטח		
-04	הכנית קומת קרקע	1:100
-05	הכנית קומה א	1:100
הכניות שטח לבן		
-06	הכנית קומת קרקע	1:100
-07	הכנית קומה א	1:100
-08	הכנית קומה ב	1:100
-09	הכנית גגות	1:100
-10	החכים	1:100
-11	חתימות	1:100
-12	חתימות	1:100
הכניות עבודה		
-13	הכנית עבודה קומה א	1:50
-14	חתך א-א', ב-ב'	1:50
-15	חזית צפוןית, מערבית	1:50
פרטי בניין		
-16	מדרגות-הכניות, פרטים	1:50, 1:20
-17	מדרגות-חכים	1:20
-18	קיר ייחודי-חכים	1:20
-19	קיר ייחודי-פרטים	1:5
עיצוב פנים		
-20	הכנית ריהוט, ריצוף	1:50
-21	הכנית תקרה וריפוד אזורי	1:50
-22	הדמיות ופריסת קיר	1:50
-23	הכנית דלפק	1:10, 1:20
קונסטרוקציה		
-24	הכניות קונסטרוקציה	1:100

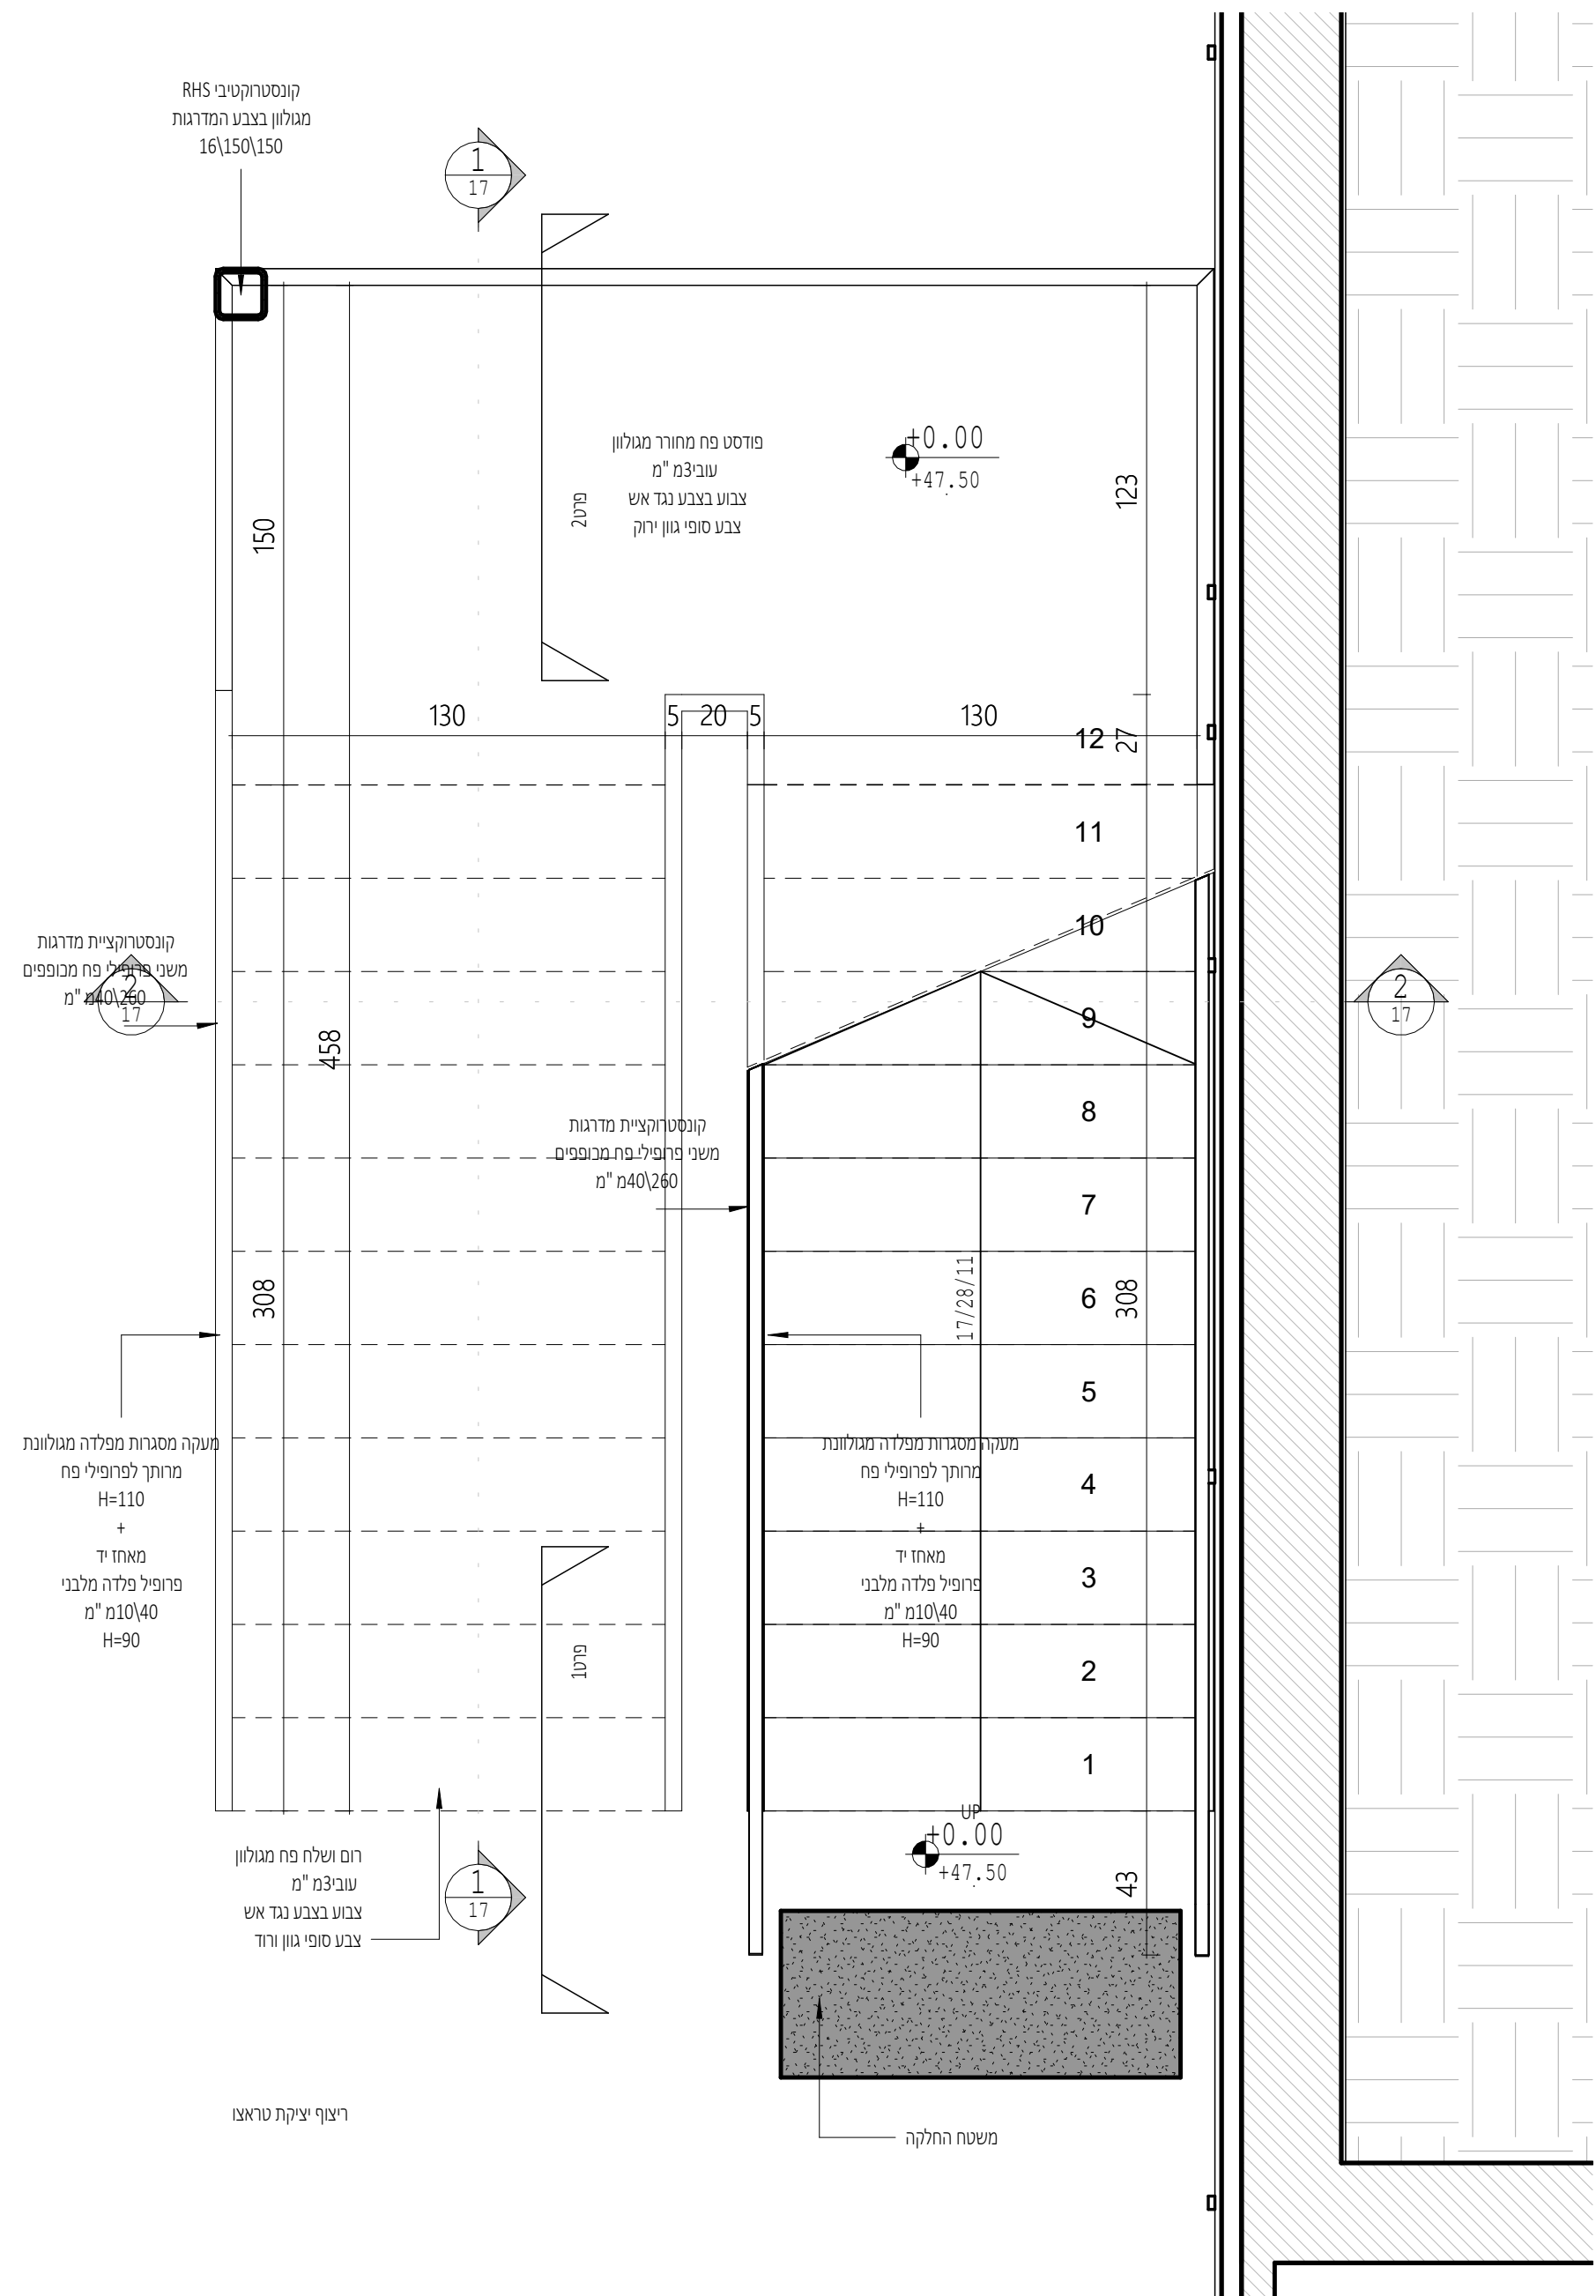


תוכנית קומת קרקע ומדרגות
1 : 20

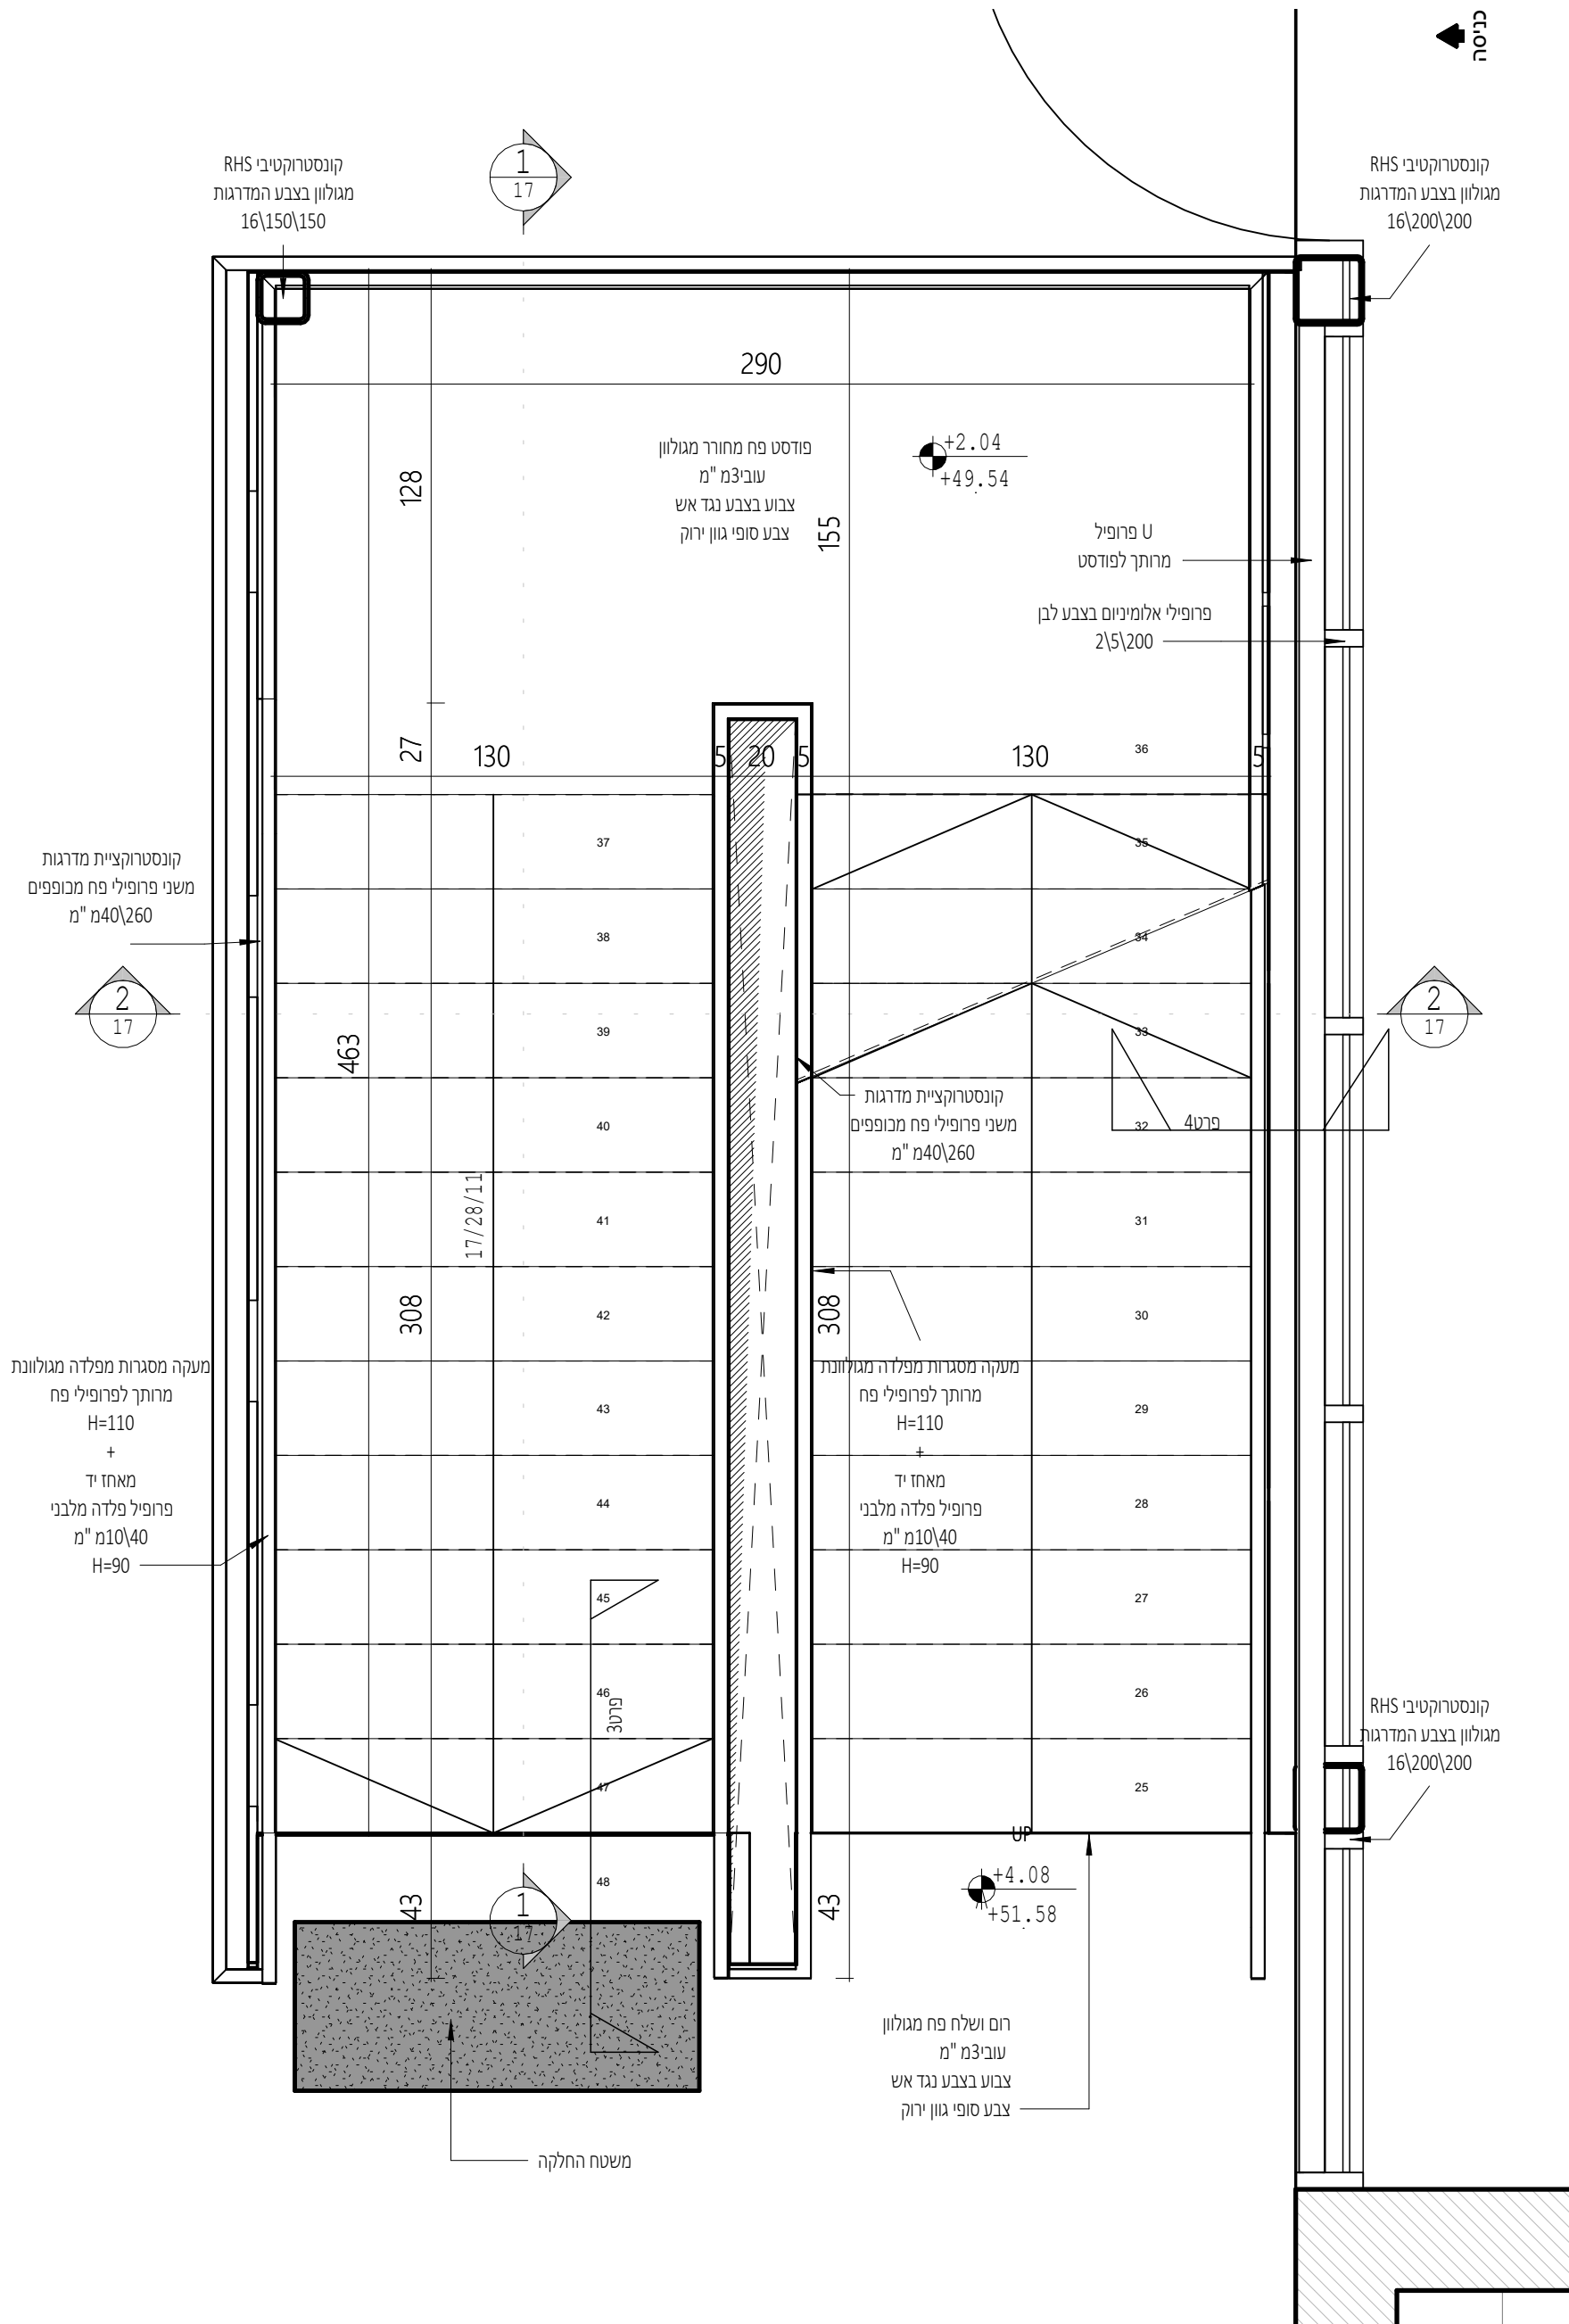


תכנית קומה א ומדרגות
1 : 20

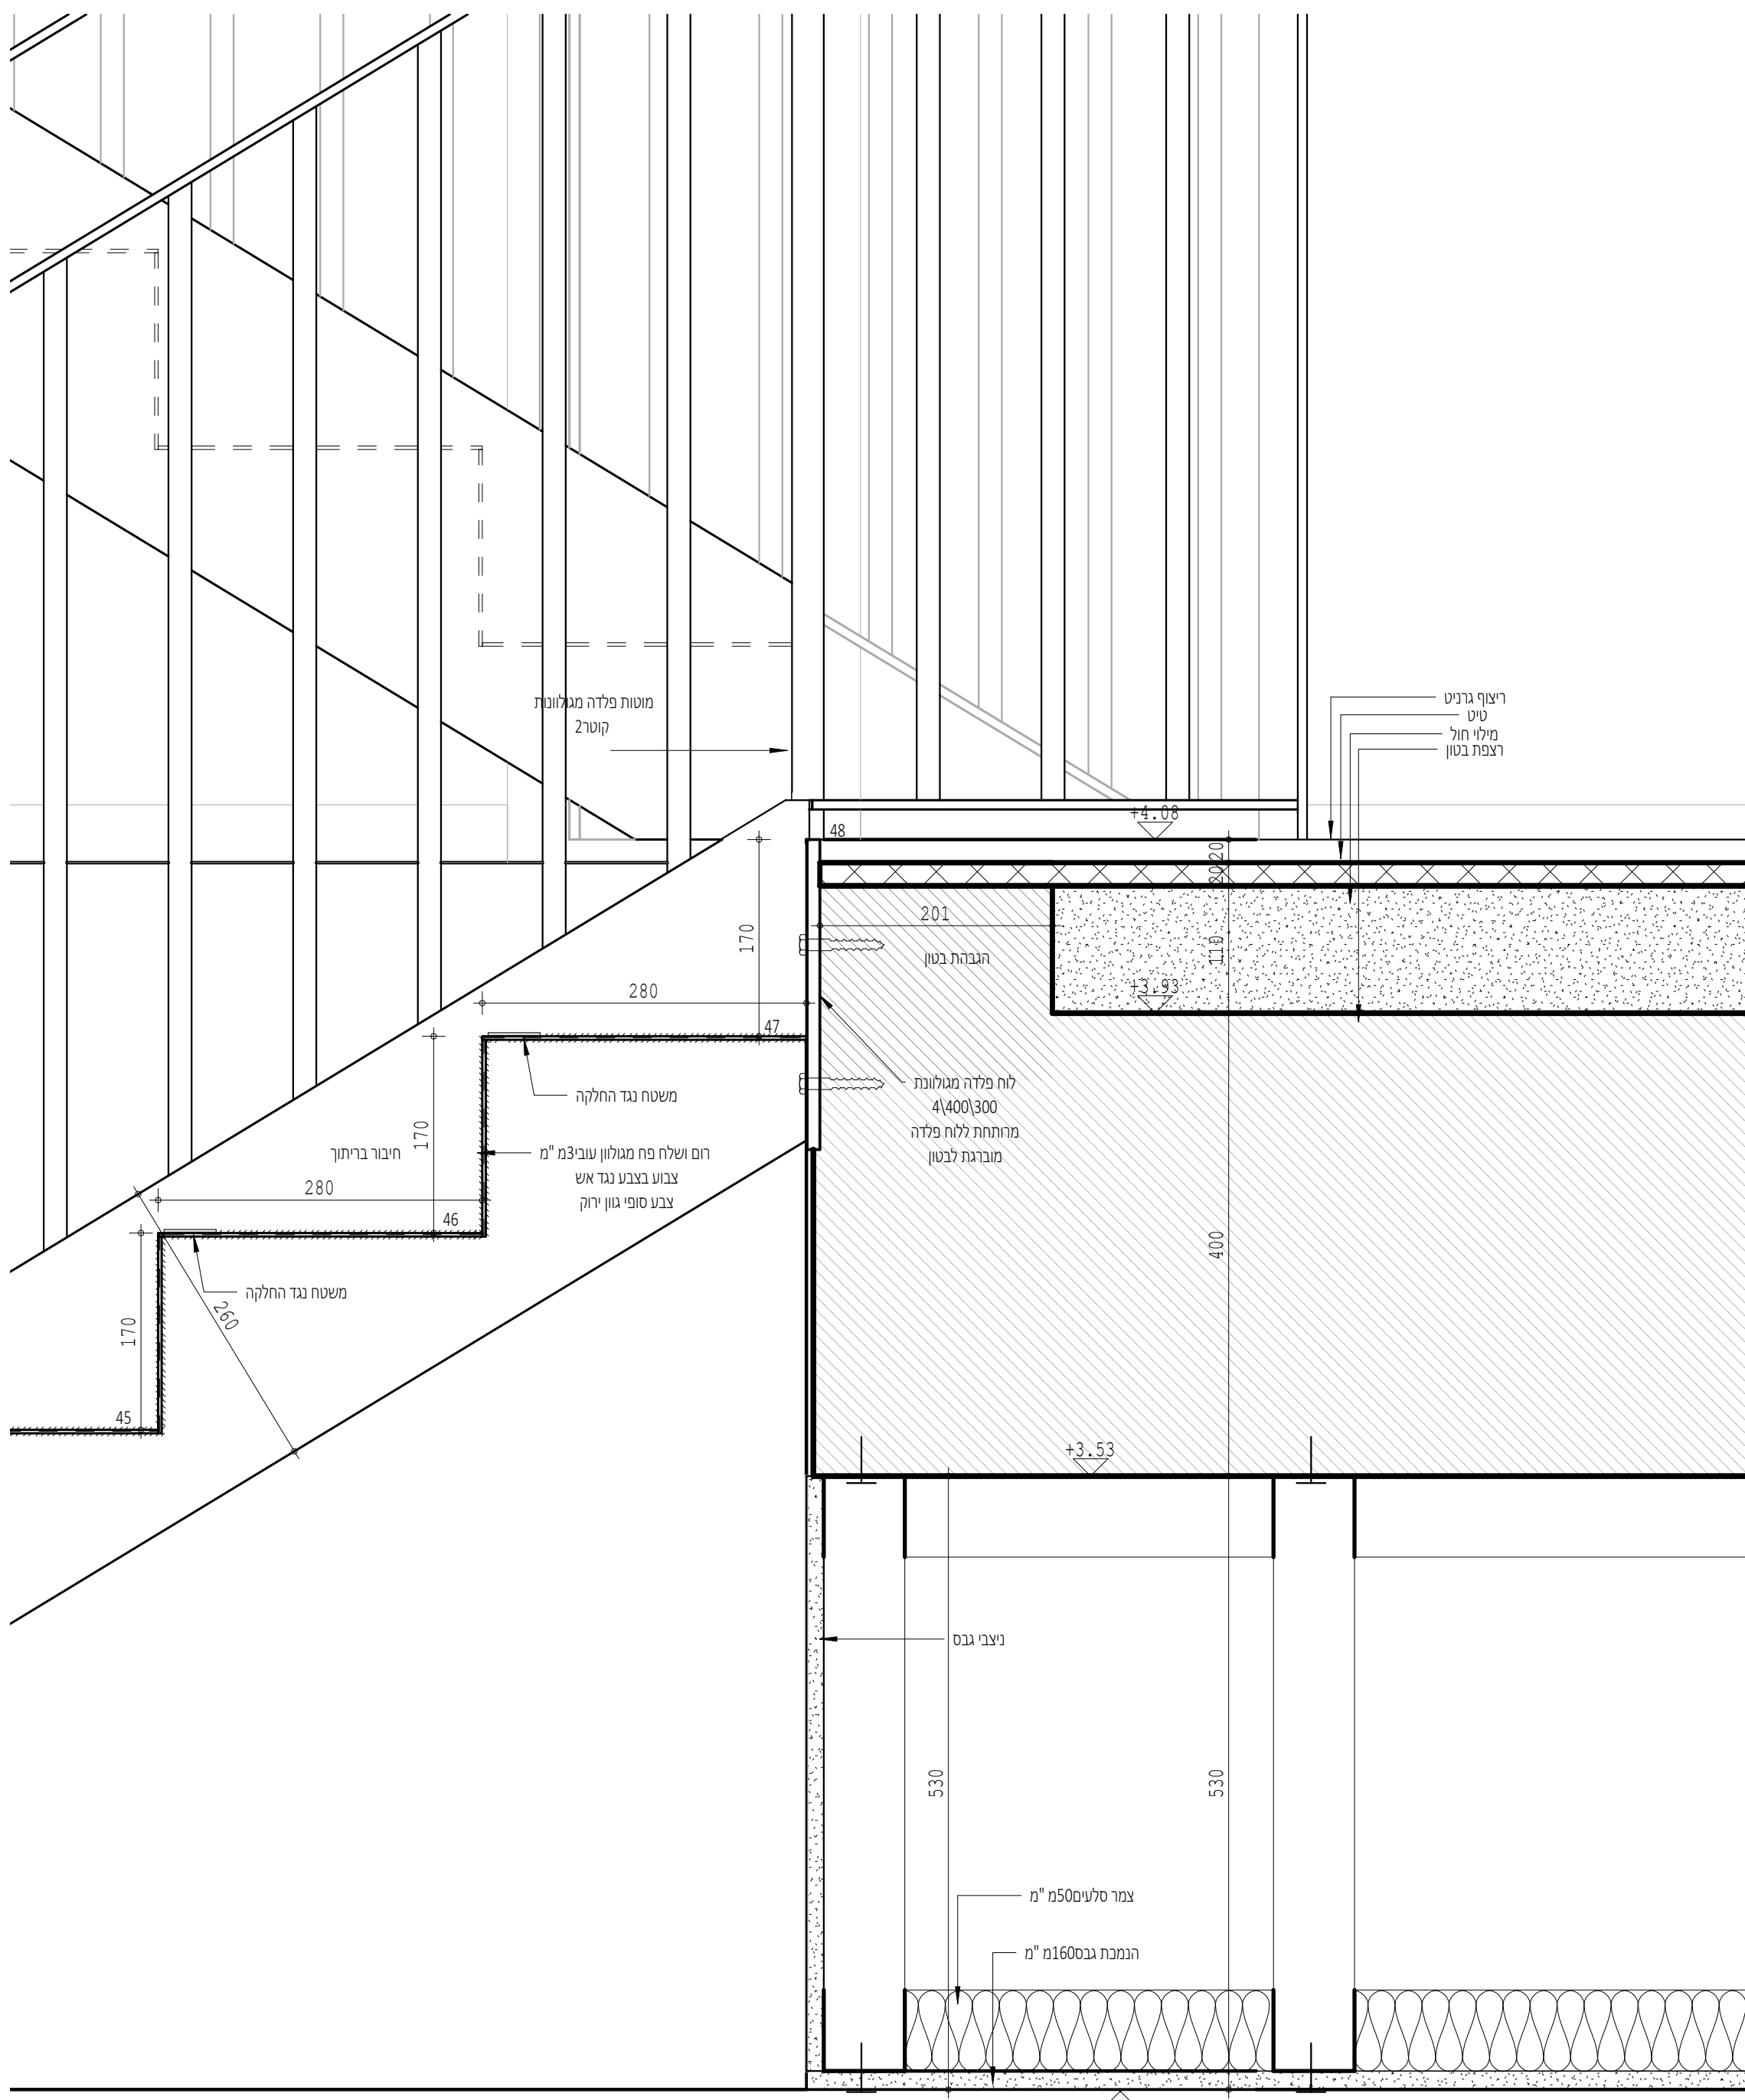


פרט חיבור מדרגה לרצפה
1 : 5

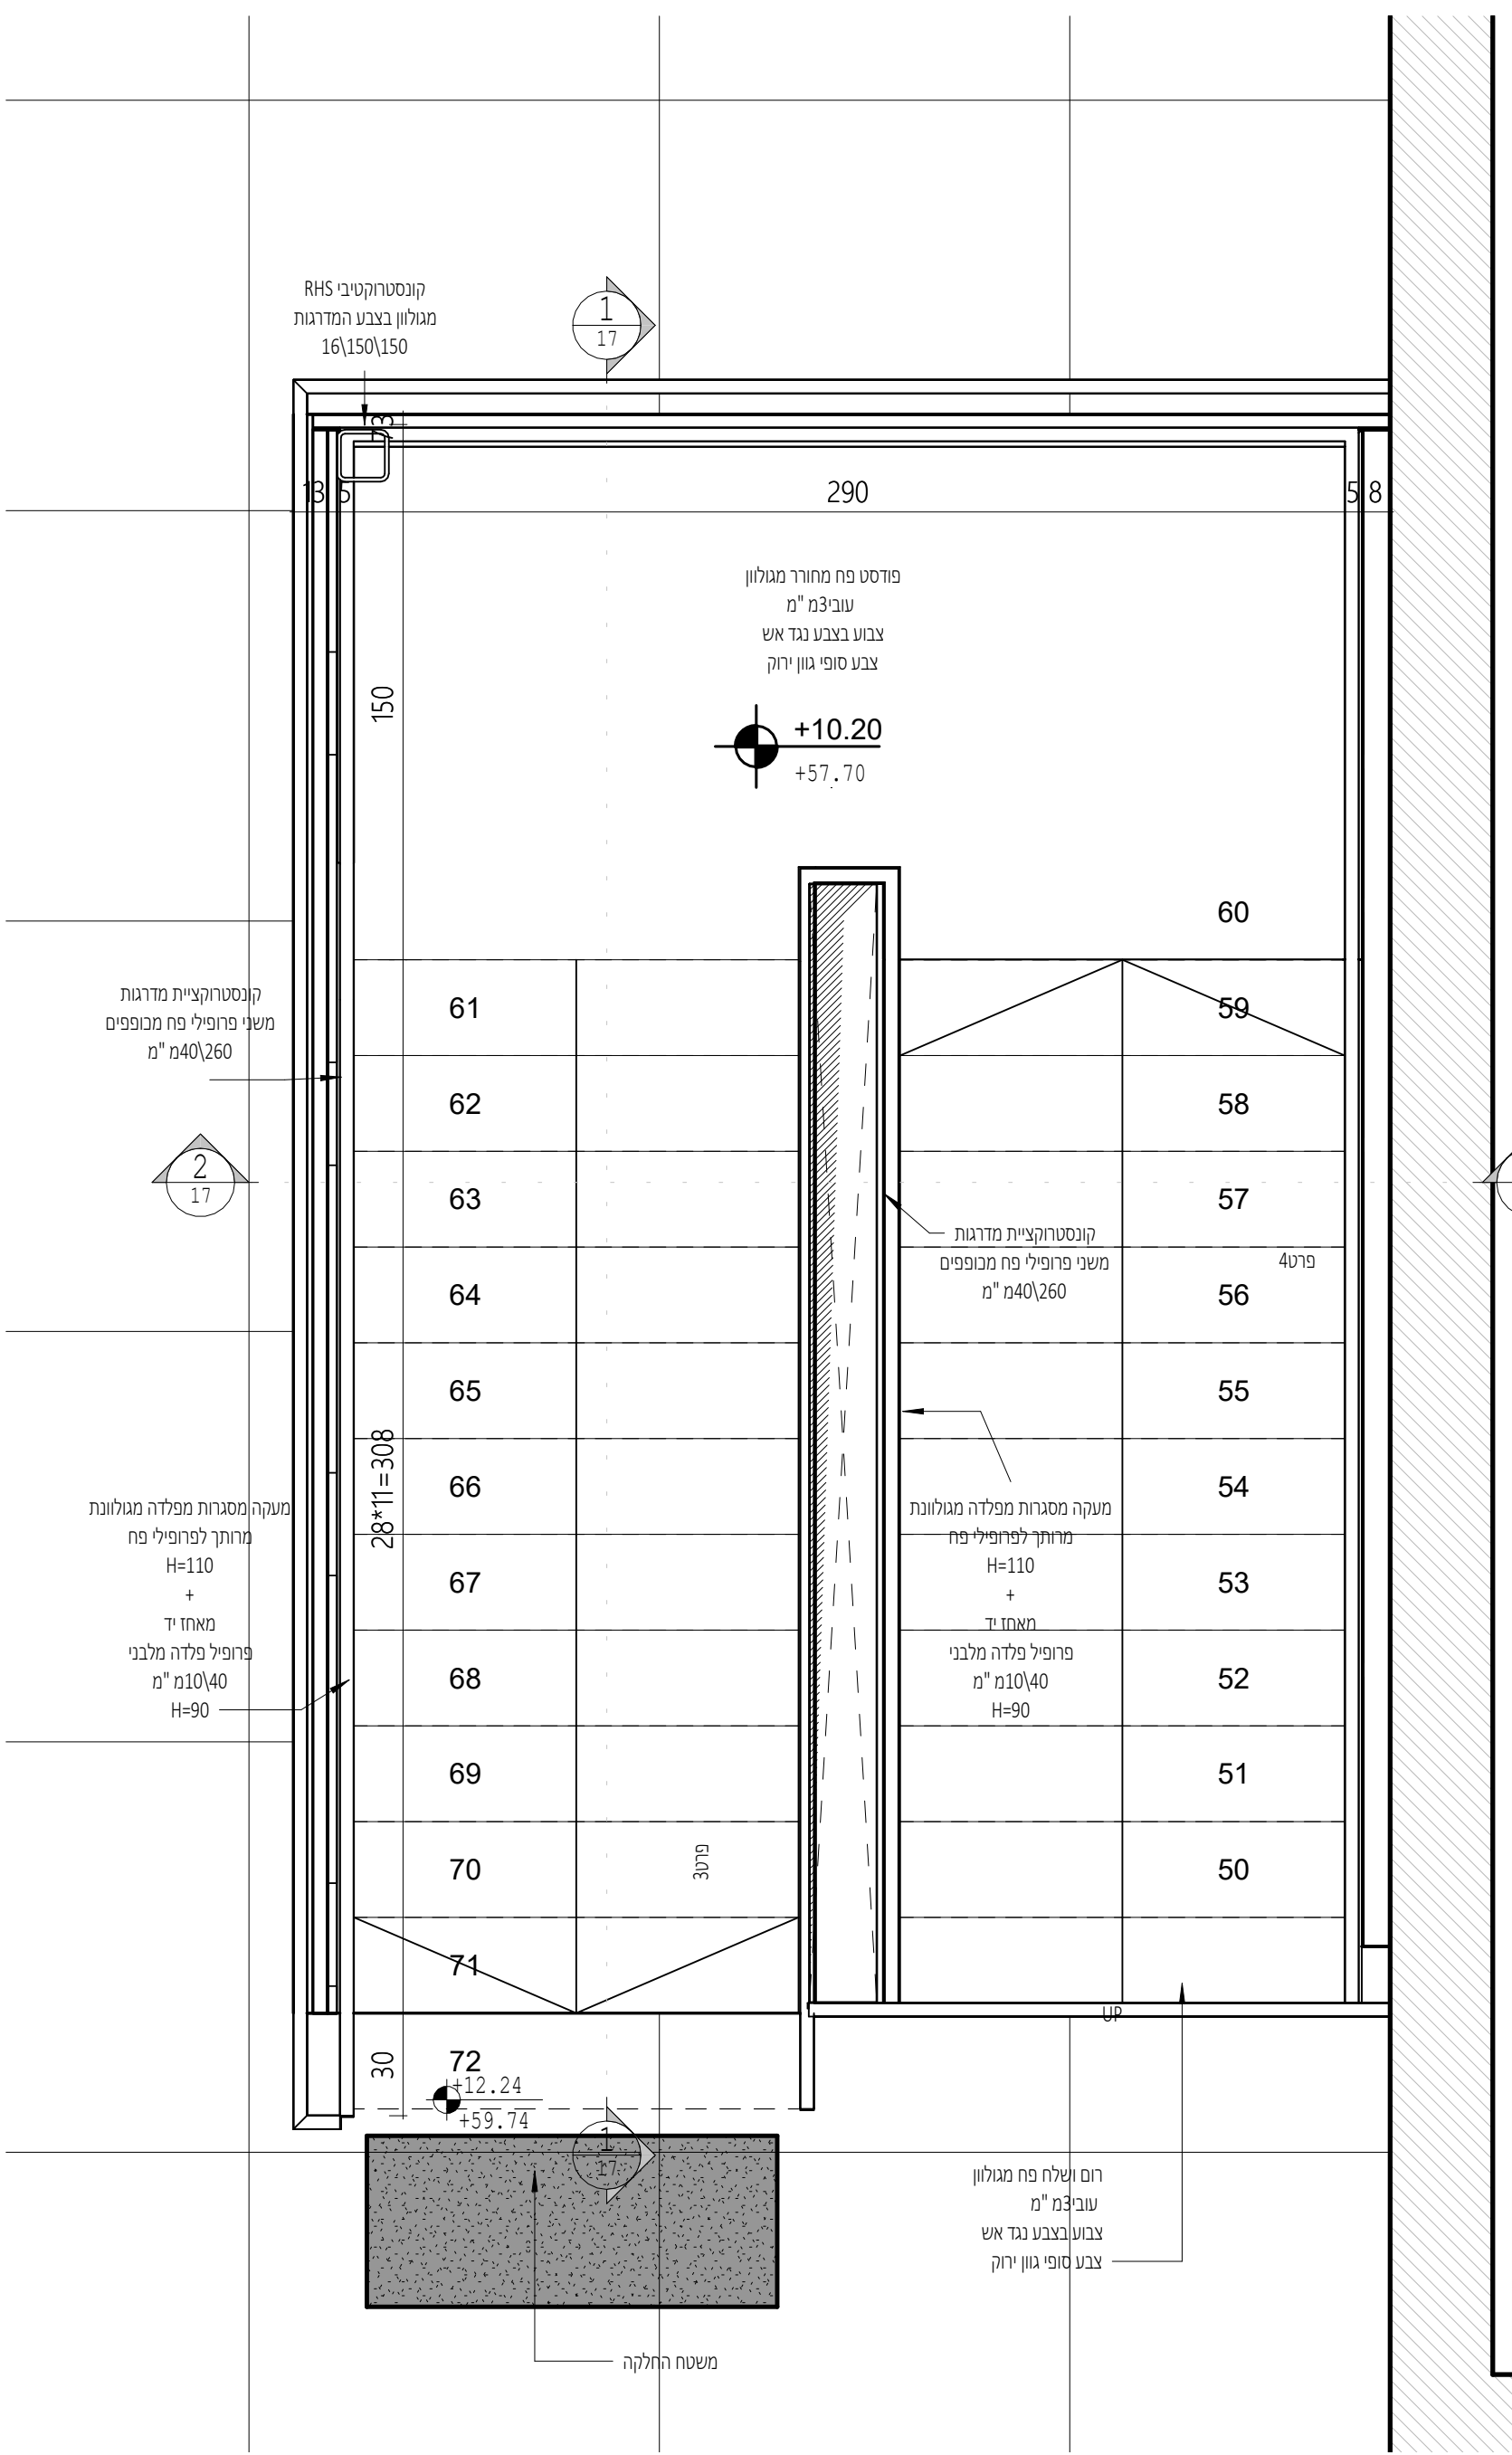


תכנית גג ומדרגות
1 : 20

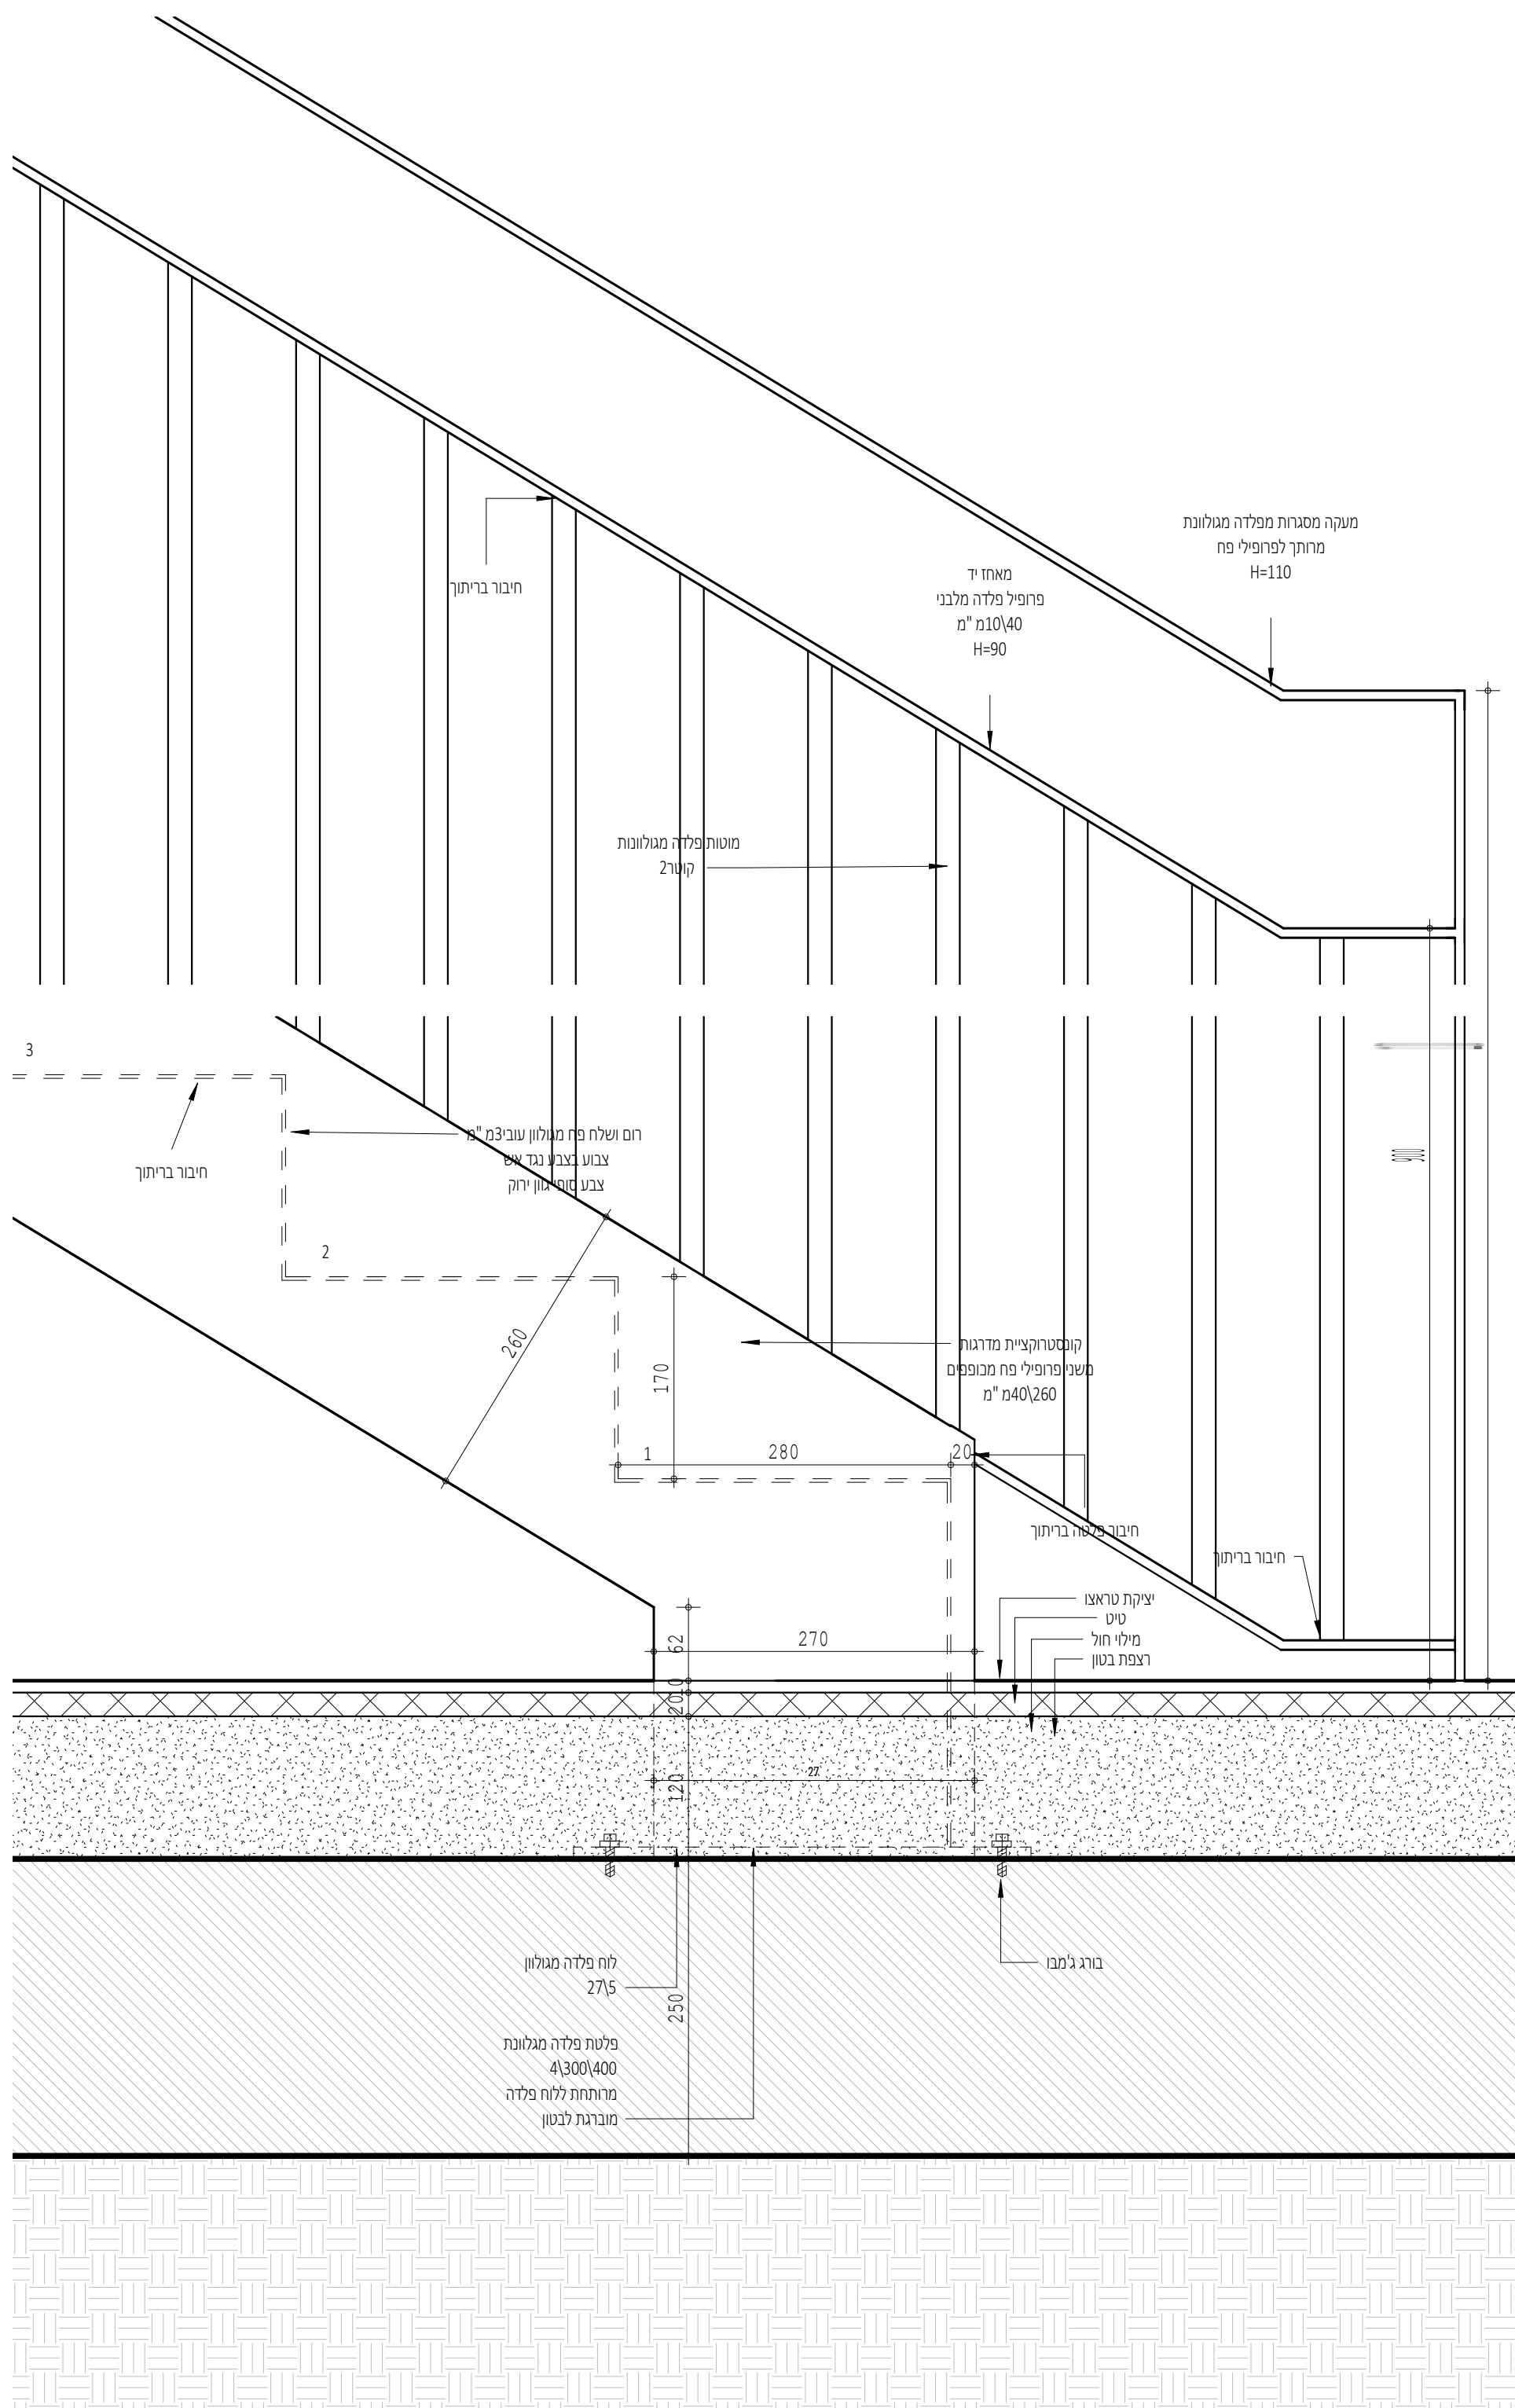

פרט מדרגות ראשונות
1 : 5

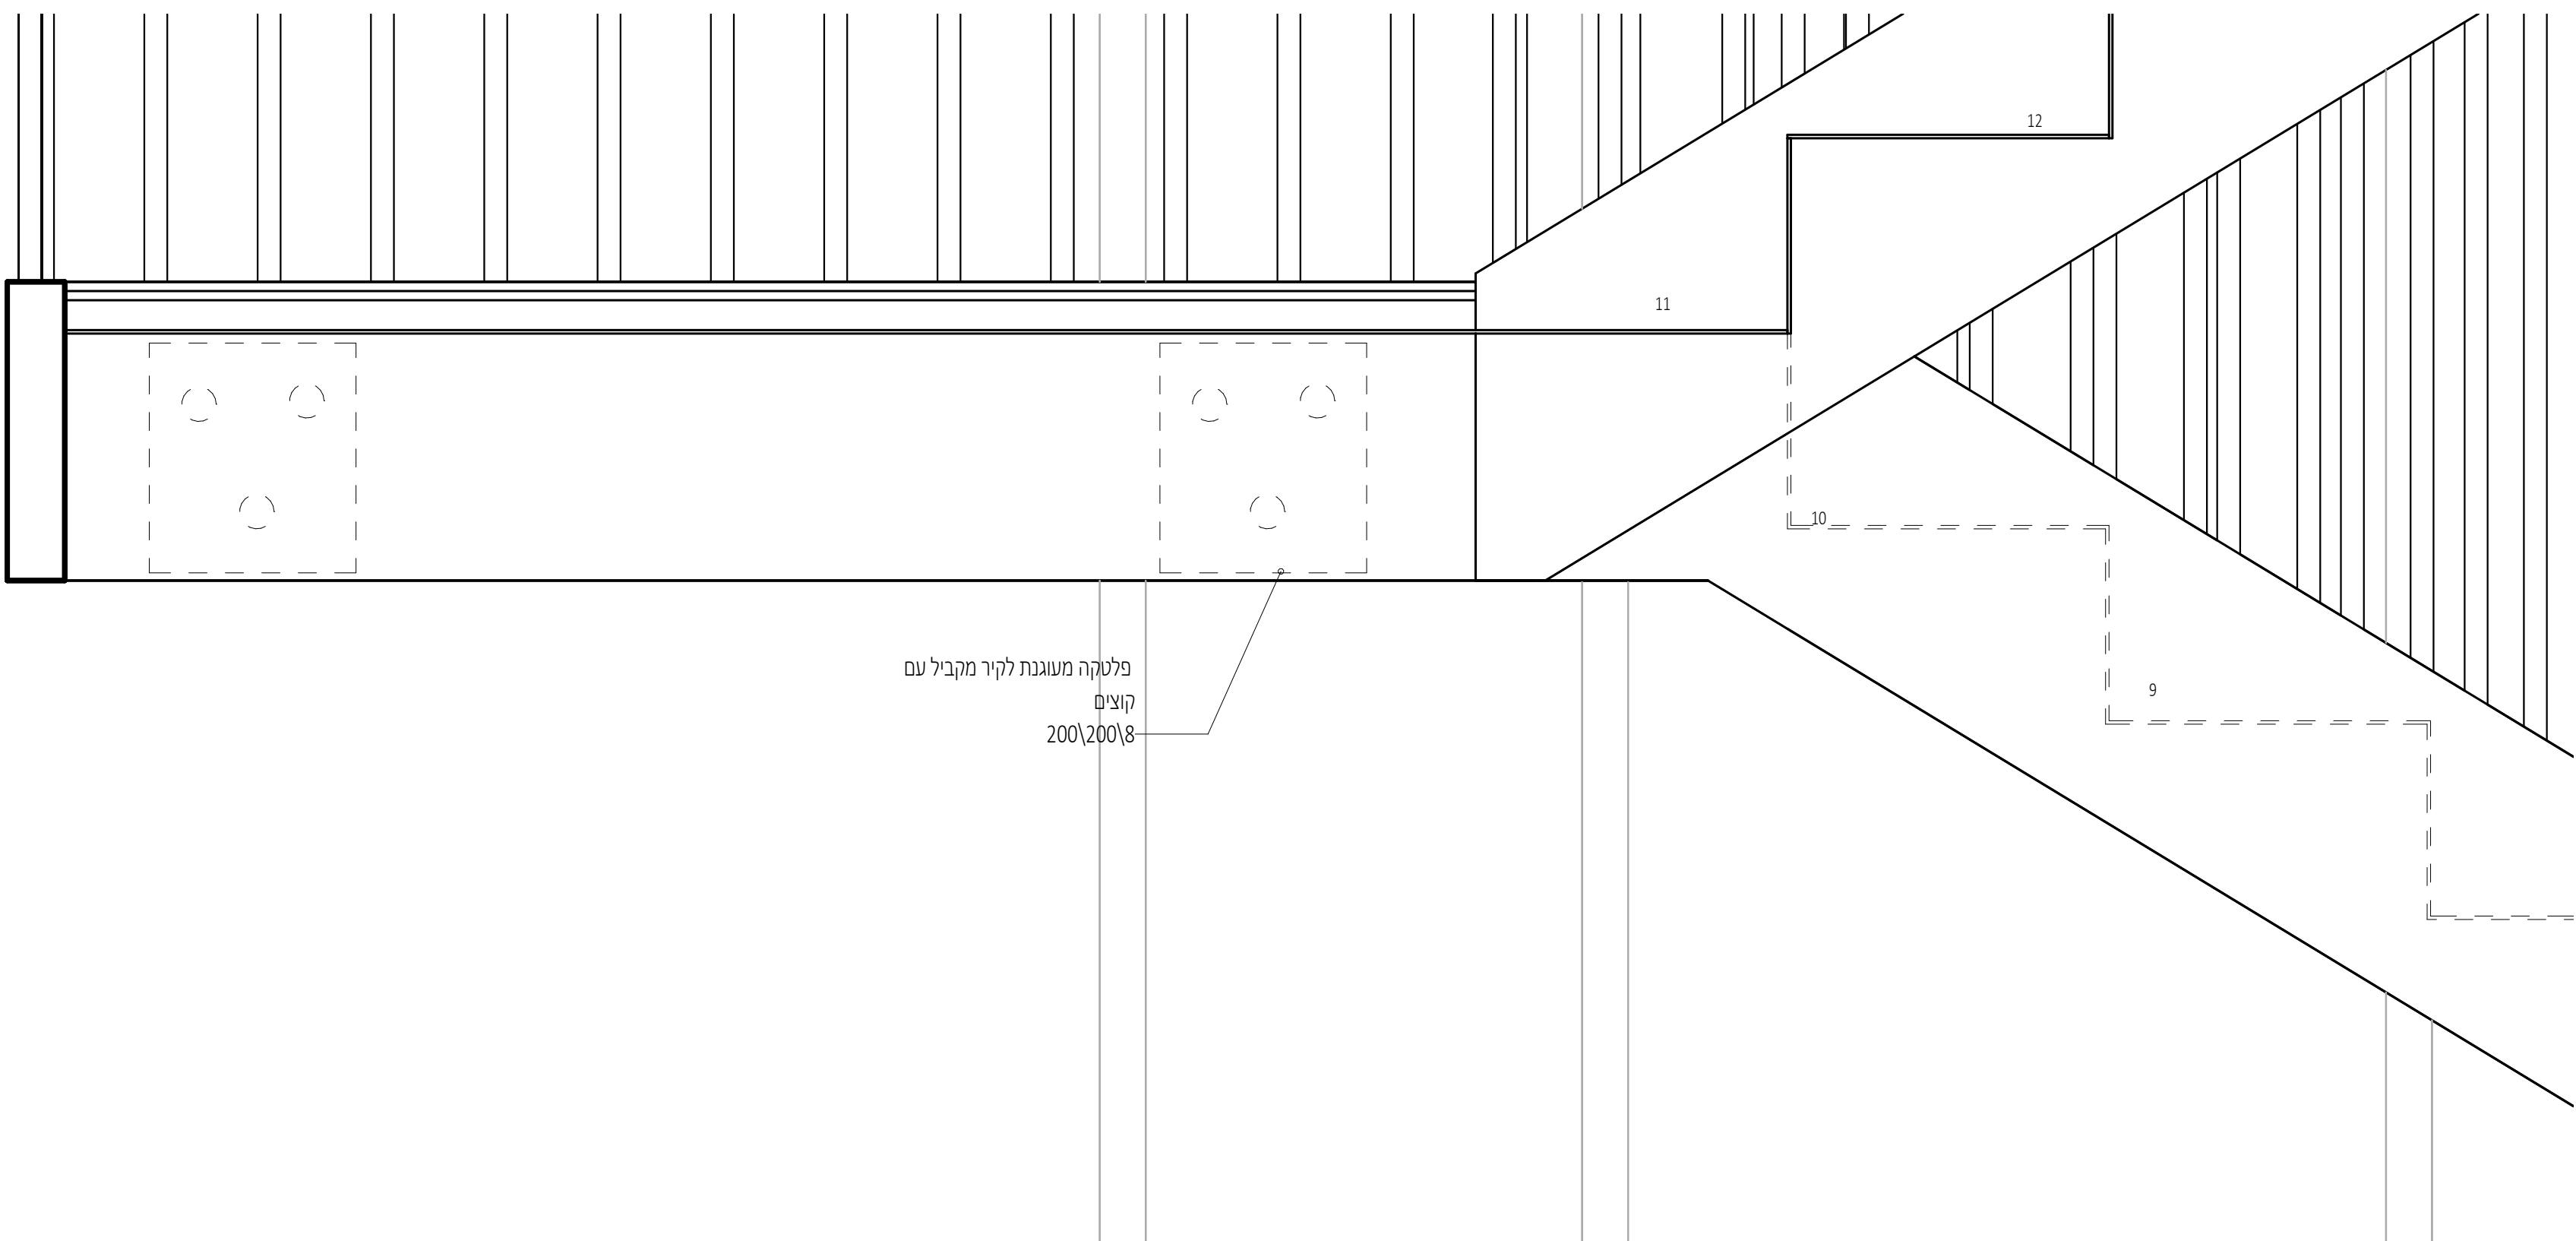


פרט 2 - מדרגות אחרונות
1 : 5

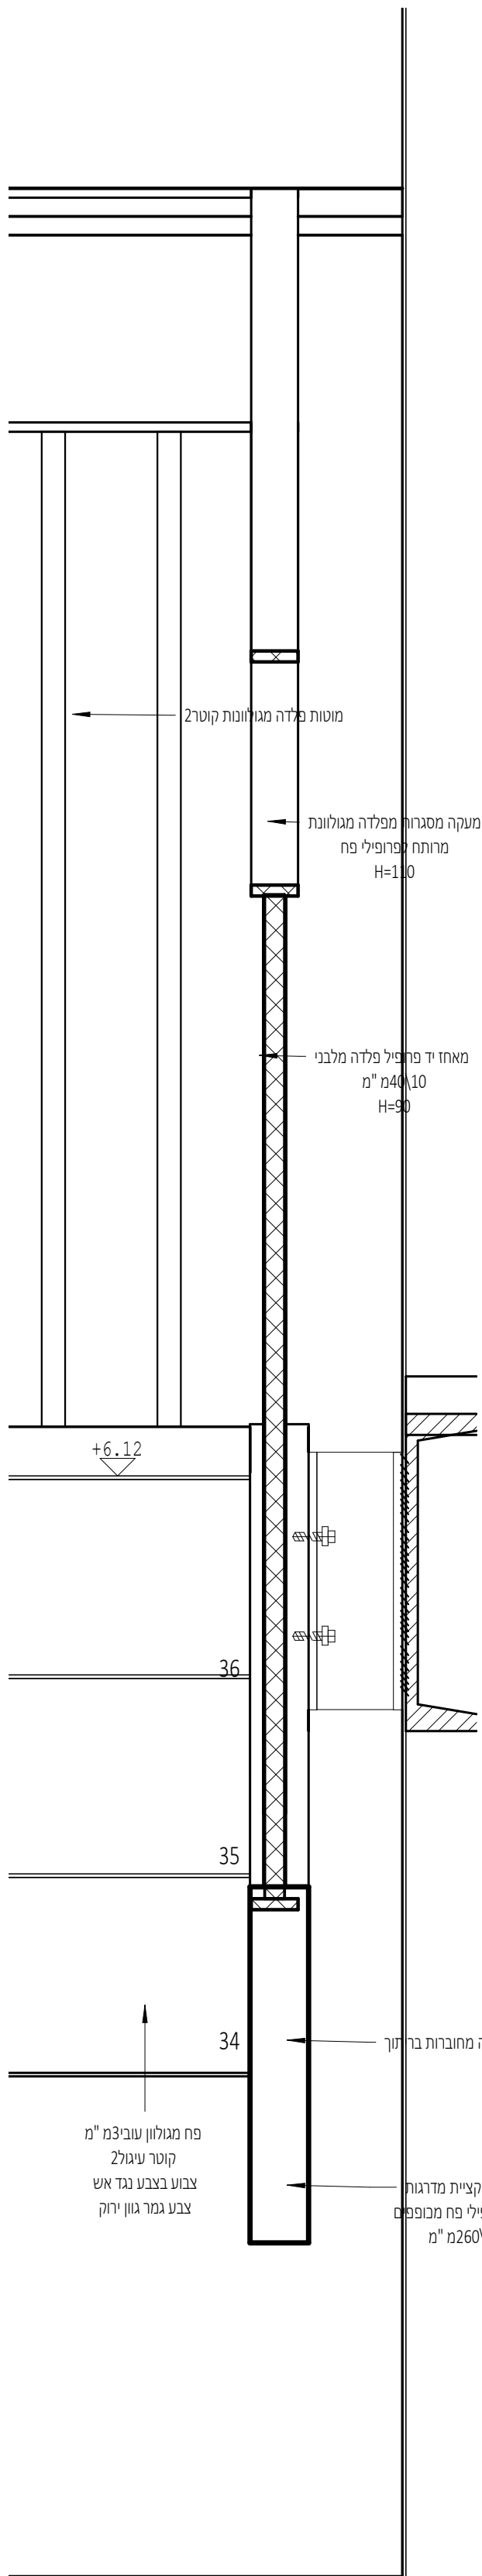


פרט 4 - חיבור מעקה ומדרגות
1 : 5




מס'	מ"אור גיליון:	קניית:
-00	טער	
-01	גיתוח סביבה	
-02	סקיצות -פרוגרמה	
-03	הדמיות	
פירוט טעם		
-04	הכנית קומות קרקע	1:100
-05	הכנית קומות א	1:100
הכניות שטור לבן		
-06	הכנית קומות קרקע	1:100
-07	הכנית קומות א	1:100
-08	הכנית קומות ב	1:100
-09	הכנית גגות	1:100
-10	החכים	1:100
-11	חתימות	1:100
-12	חתימות	1:100
הכניות עבודה		
-13	הכנית עבודה קומות א	1:50
-14	חתך א'-א', א'-ב', ב'-ב'	1:50
-15	חזית צפוןית, מערבית	1:50
פרטי בניין		
-16	מדרגות-החכים, פרטים	1:20 1:5
-17	מדרגות-החכים	1:20
-18	קיר ייחודי-החכים	1:20
-19	קיר ייחודי-פרטים	1:5
עיצוב פנים		
-20	הכנית ריהוט, ריצוף	1:50
-21	הכנית תקרה וסיווג אוויר	1:50
-22	הדמיות ופריסת קיר	1:50
-23	הכנית דלפק	1:10 1:20
קונסטרוקציה		
-24	הכניות קונסטרוקציה	1:100

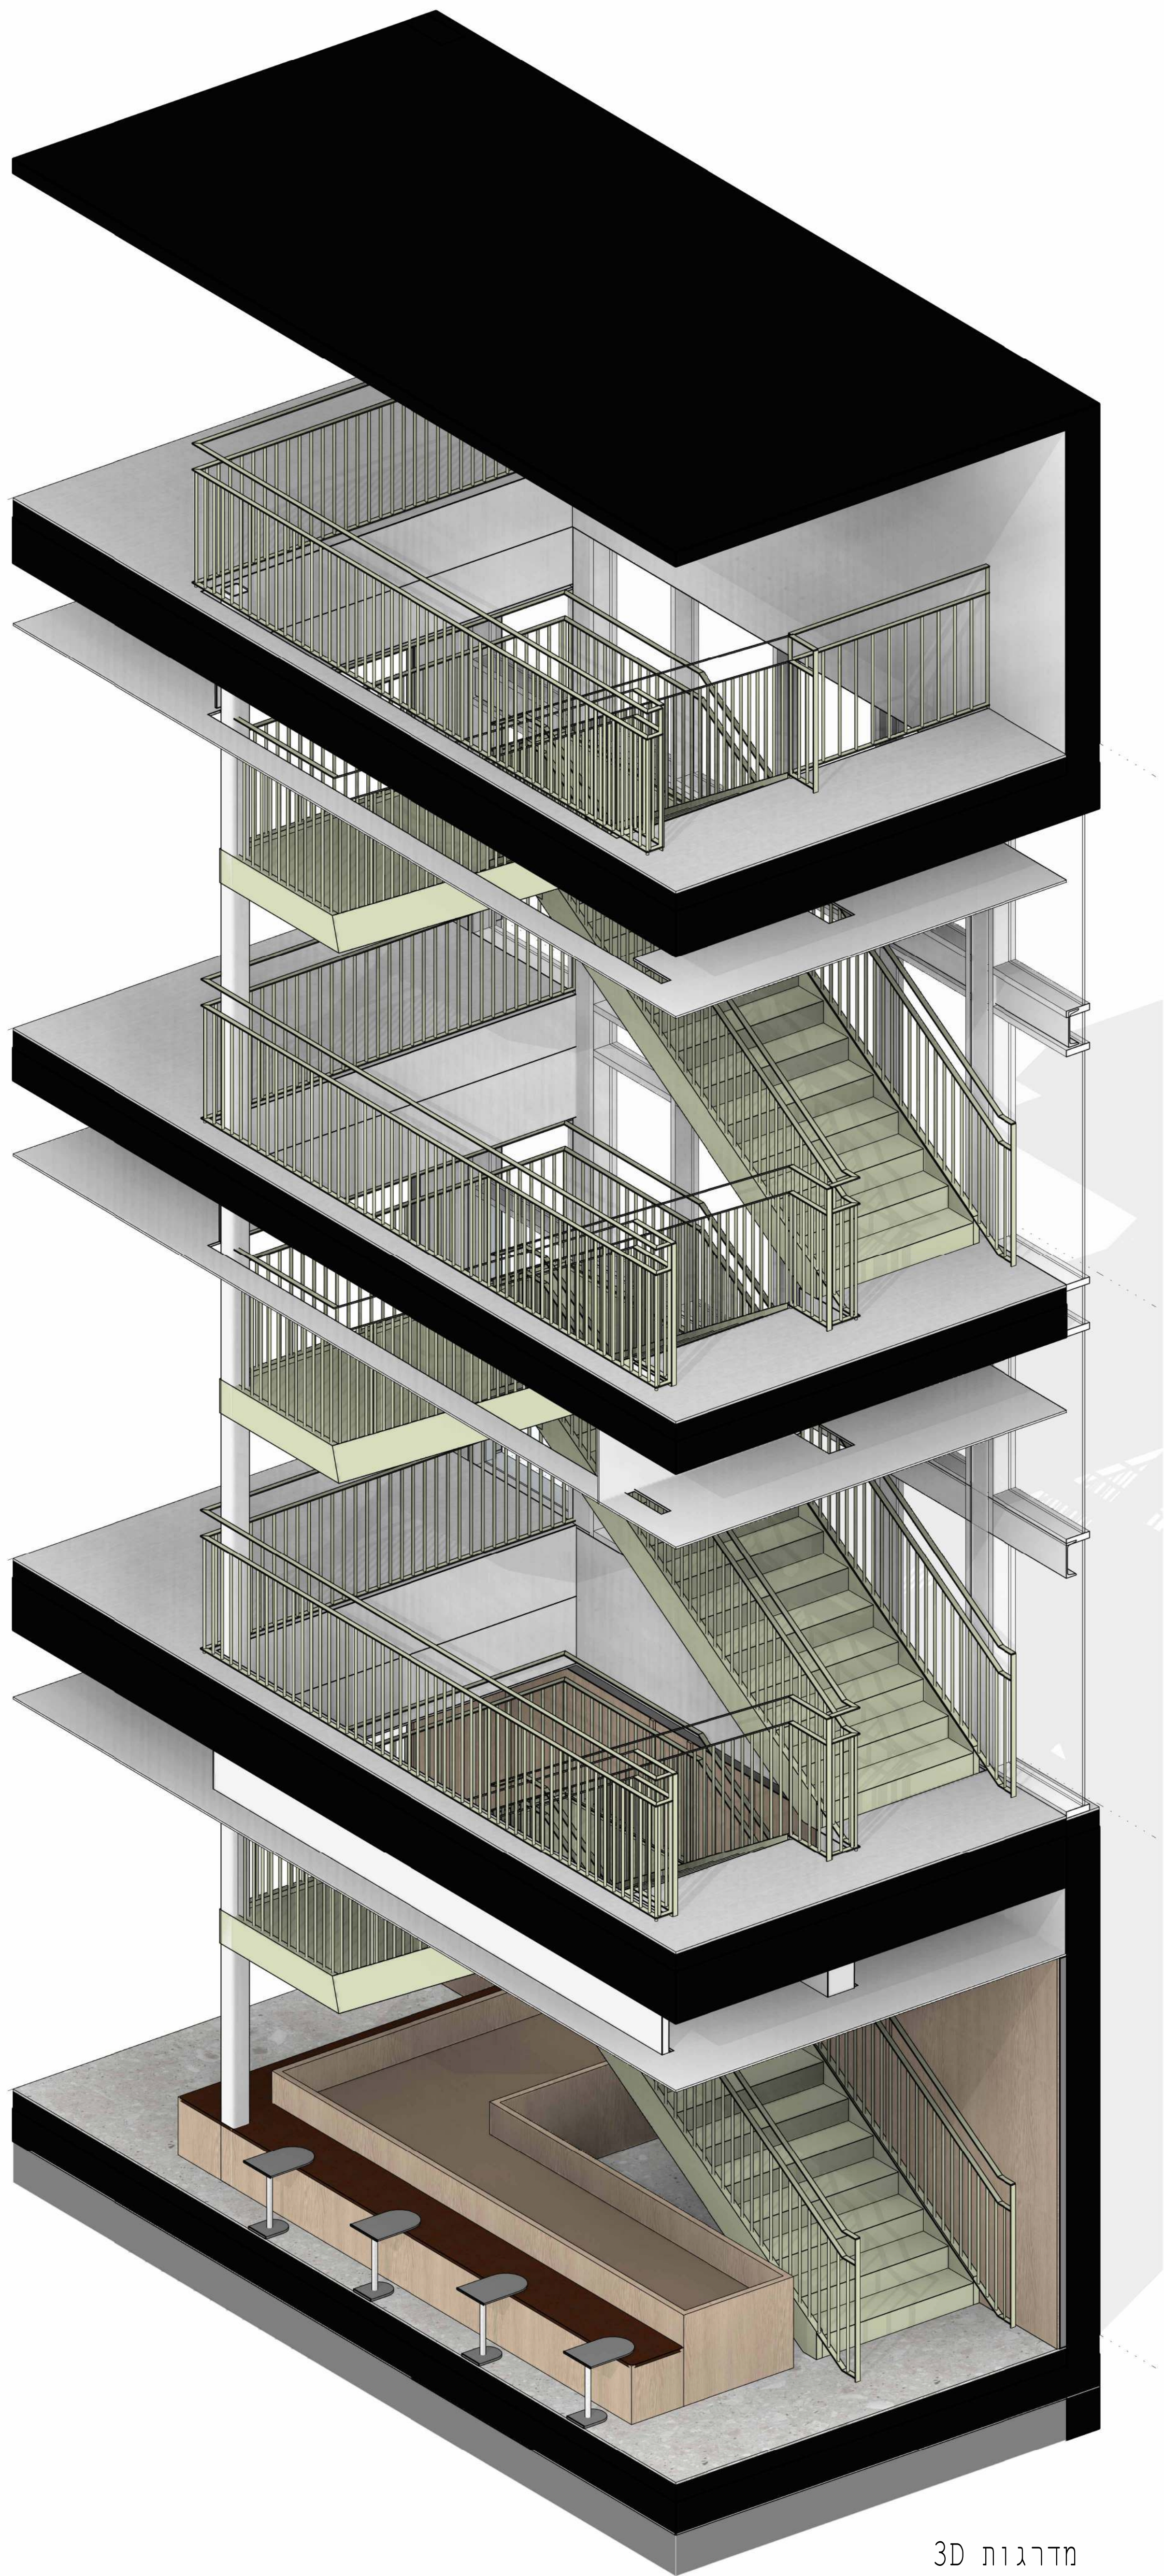

3D מדרגות

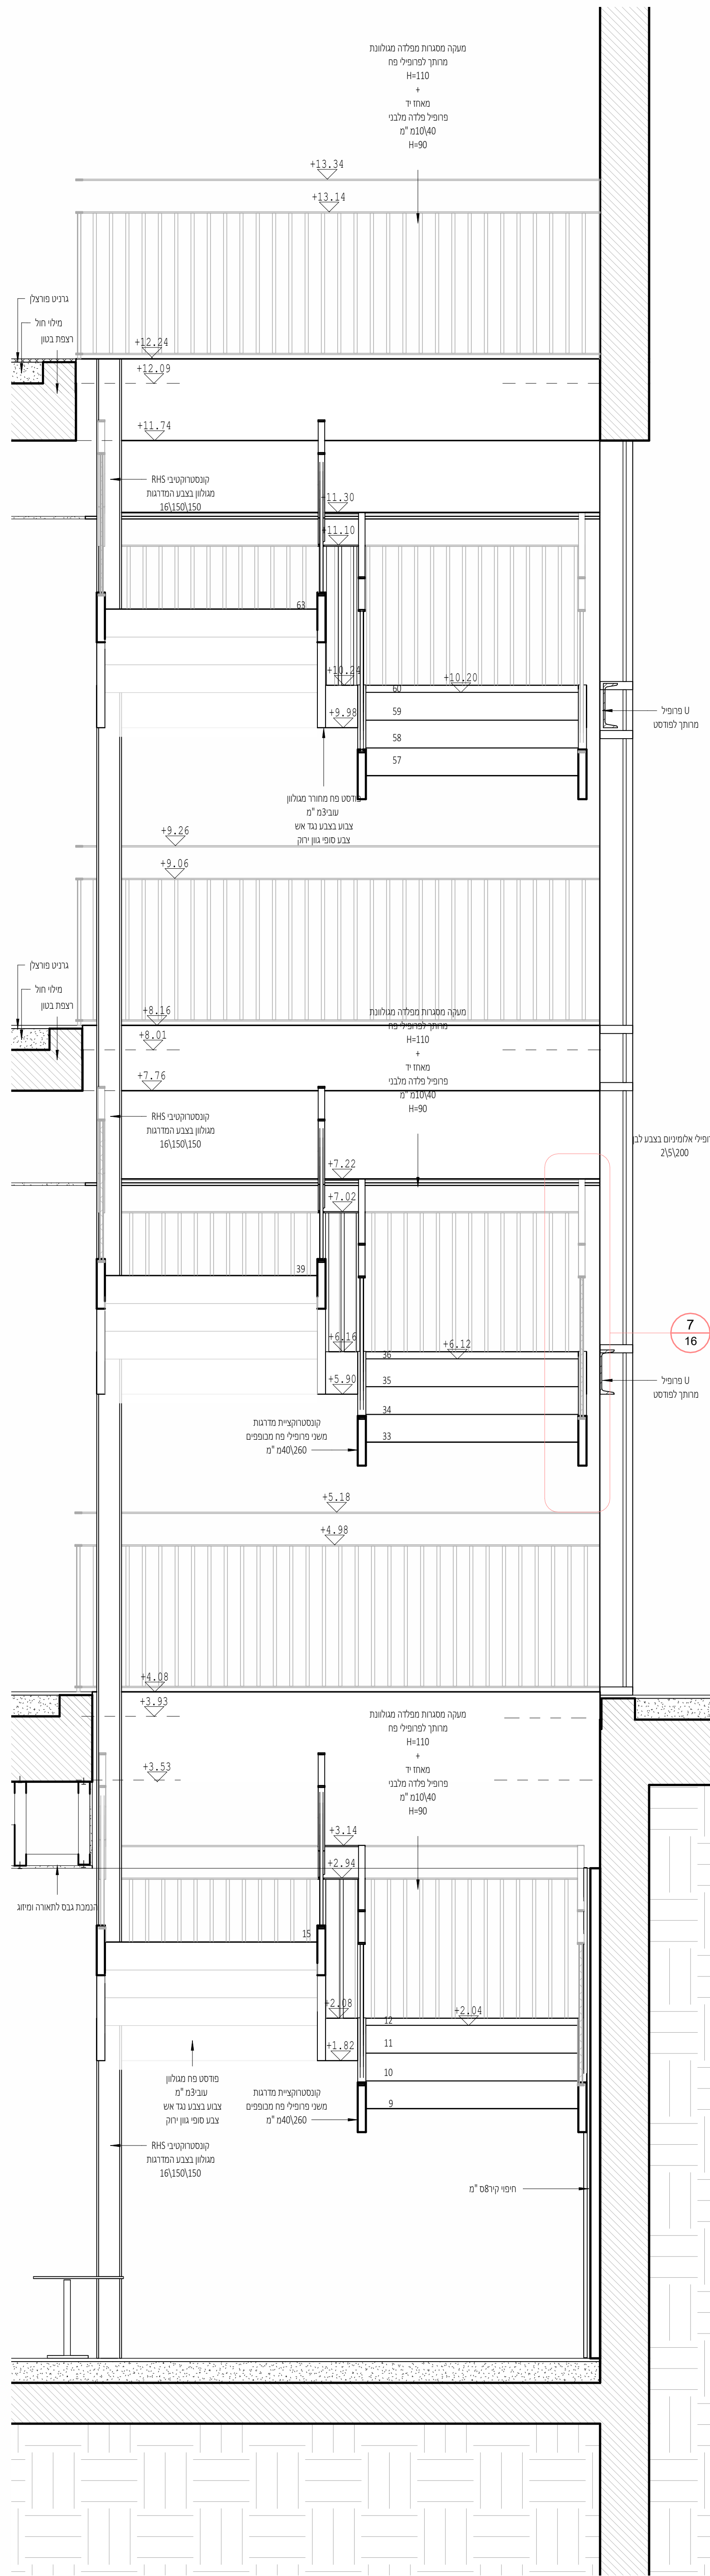

חתך רוחב מדרגות

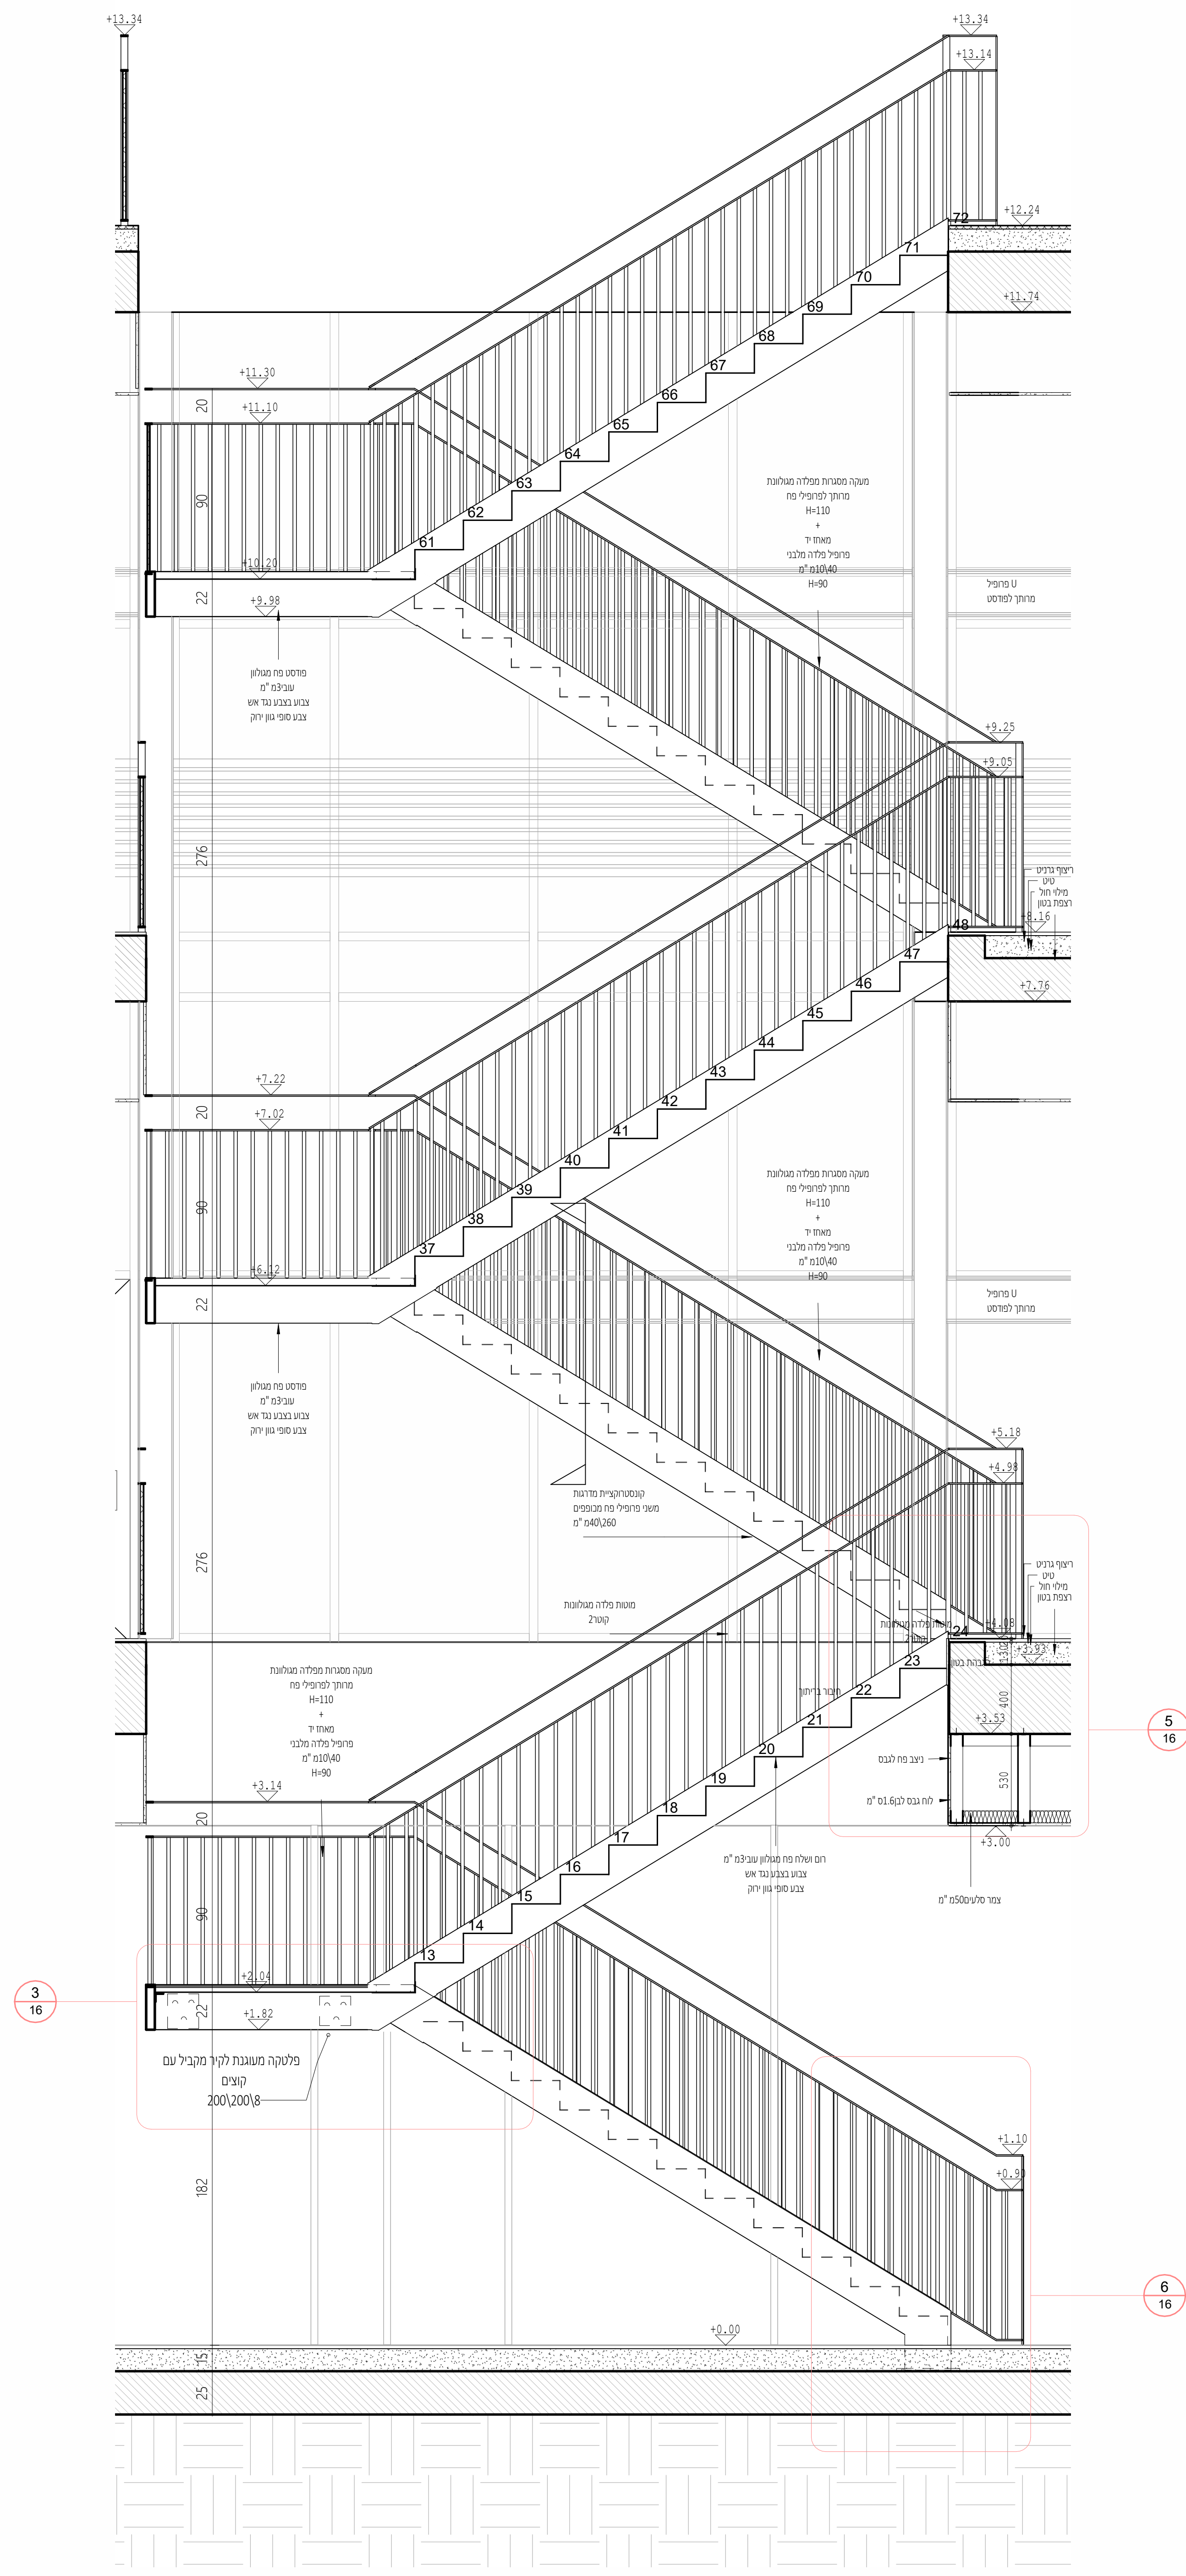

חתך אורך מדרגות

שם הפרויקט:
מעונות טטודנטים



מס'	מ'אור גיליון:	קניית:
-00	טער	
-01	גיתוח סביבה	
-02	סקיצות -פרוגרמה	
-03	הדמיות	
פירוט שטח		
-04	הכנית קומת קרקע	1:100
-05	הכנית קומה א	1:100
הכניות שטח לבן		
-06	הכנית קומת קרקע	1:100
-07	הכנית קומה א	1:100
-08	הכנית קומה ב	1:100
-09	הכנית גגות	1:100
-10	החכים	1:100
-11	חתימות	1:100
-12	חתימות	1:100
הכניות עבודה		
-13	הכנית עבודה קומה א	1:50
-14	חתך א'-א', ב'-ב'	1:50
-15	חזית צפוןית, מערבית	1:50
פרטי בניין		
-16	הדרגות-הכניות, פרטים	1:50
-17	הדרגות-חכים	1:20
-18	קיר ייחודי-חכים	1:20
-19	קיר ייחודי-פרטים	1:5
עיצוב פנים		
-20	הכנית ריהוט, ריצוף	1:50
-21	הכנית קומה ופריזא אנזיר	1:50
-22	הדמיות ופריזת קיר	1:50
-23	הכניו דלפק	1:10 1:20
קונסטרוקציה		
-24	הכניות קונסטרוקציה	1:100

מגישה:

כרמל טעדון

שם ראש המגמה:

שרון גפני

שם המנחה:


לייט'

תאריך:

23\06\2026



חזית פרטים2

1 : 20

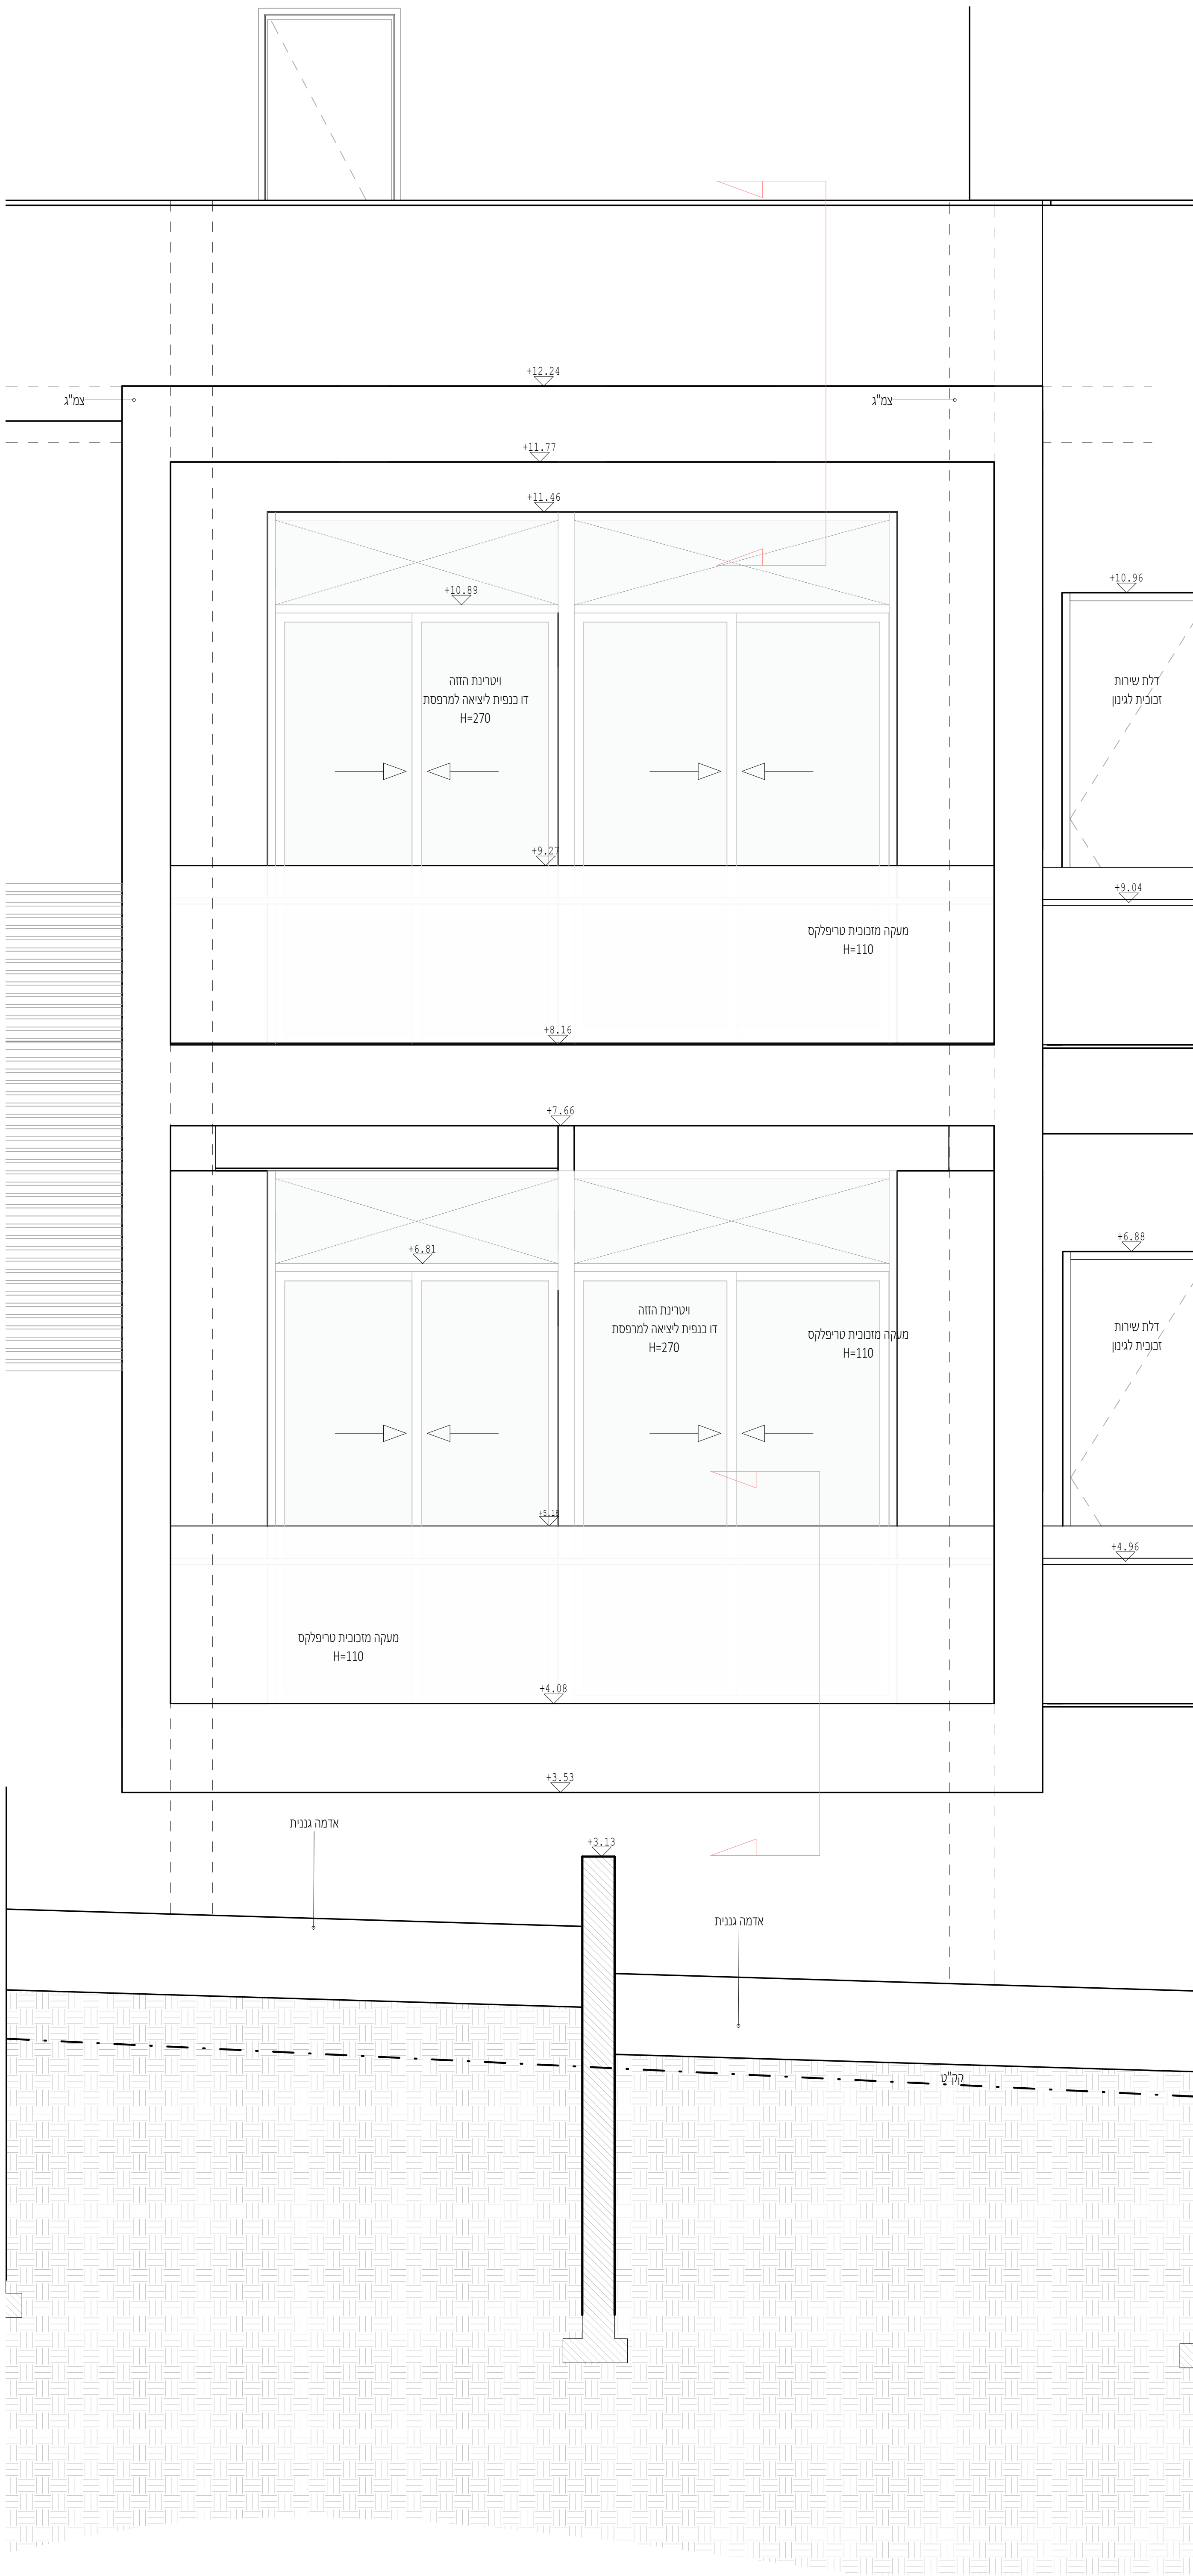


חתך פרטים2

1 : 20

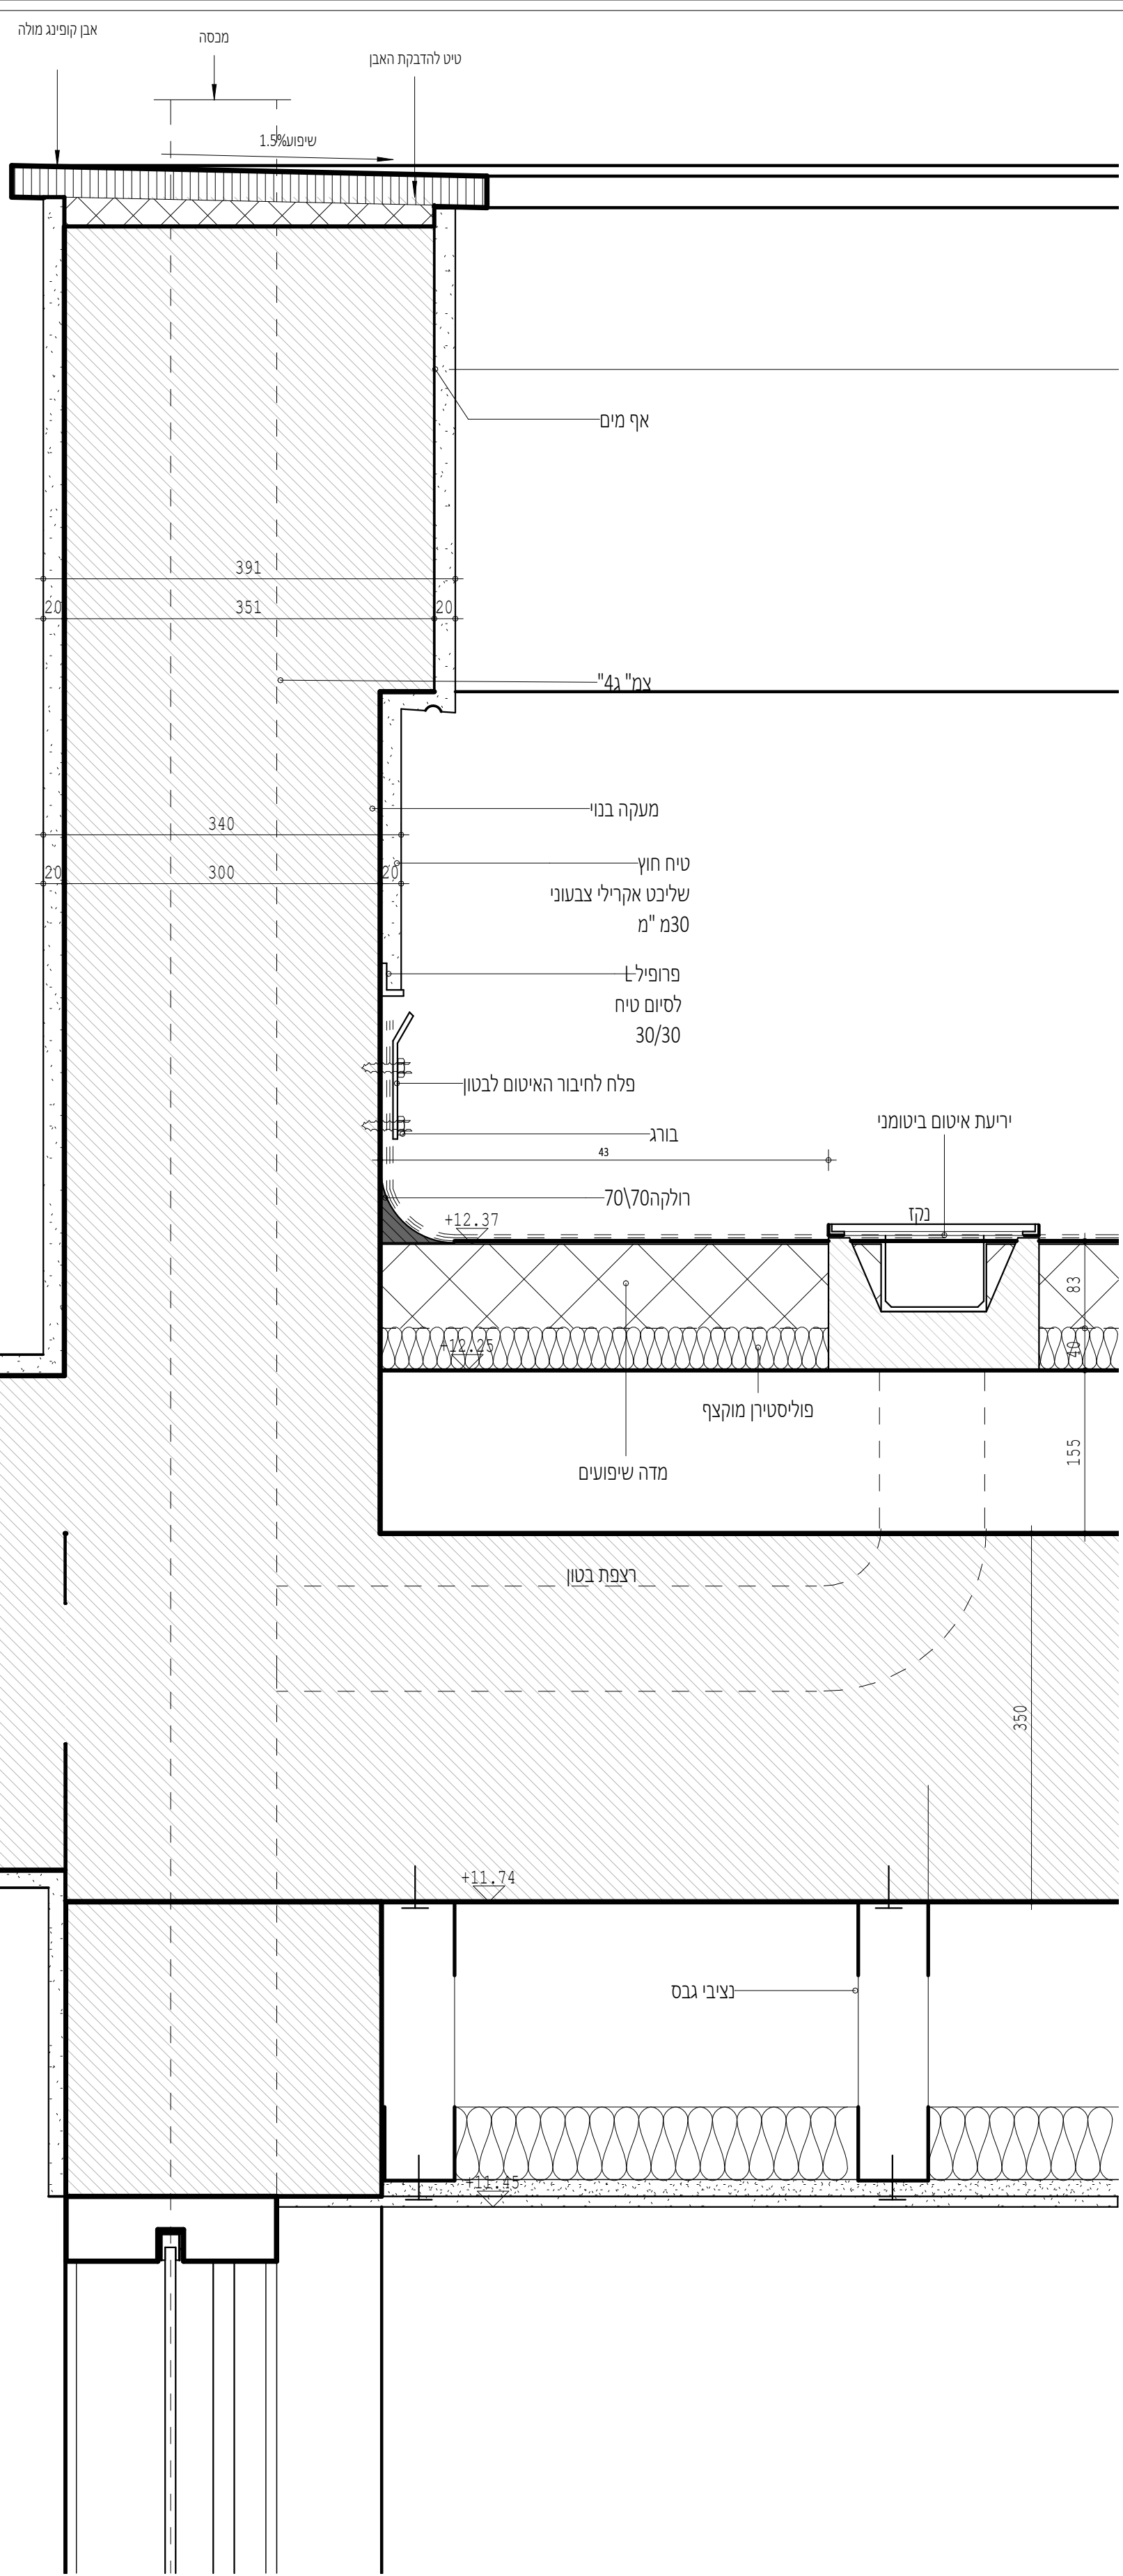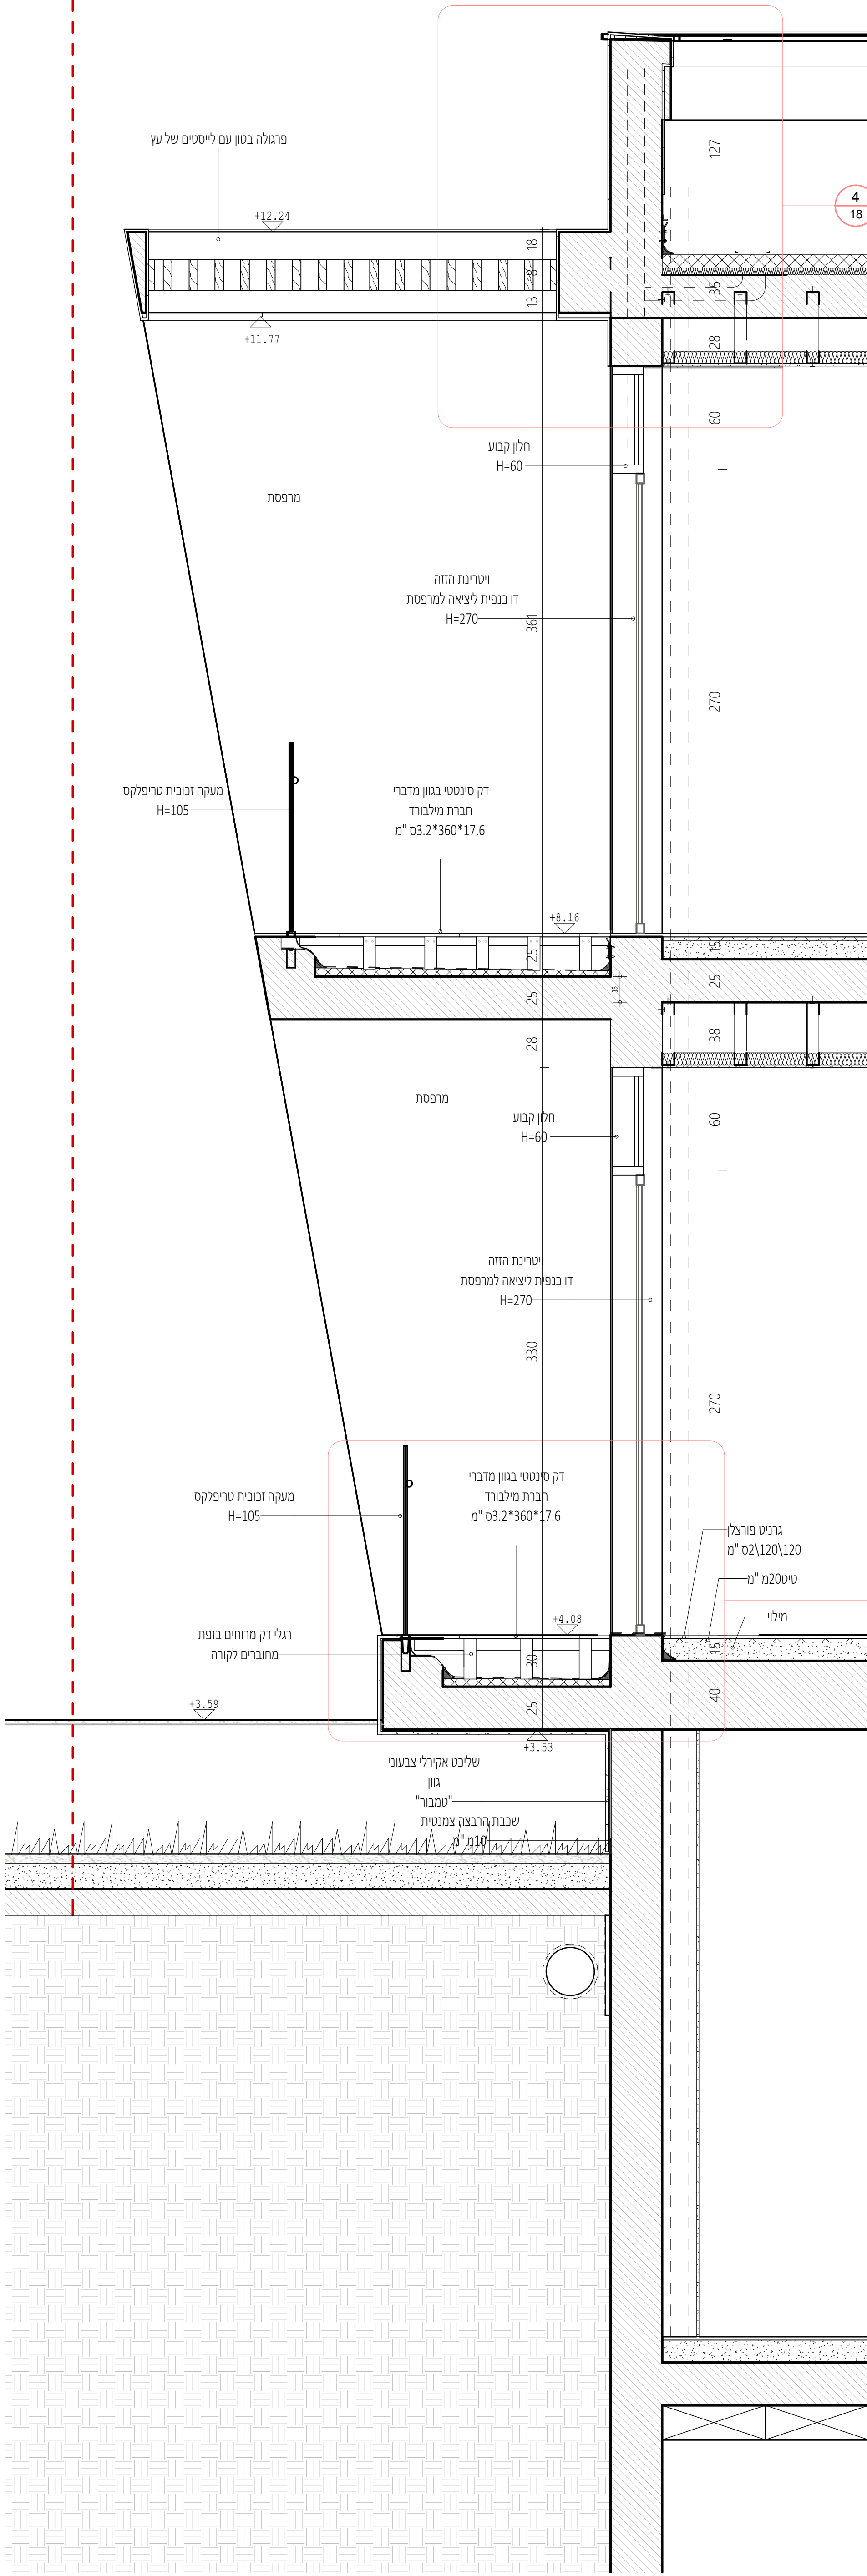

מרפסת דק


1 : 5

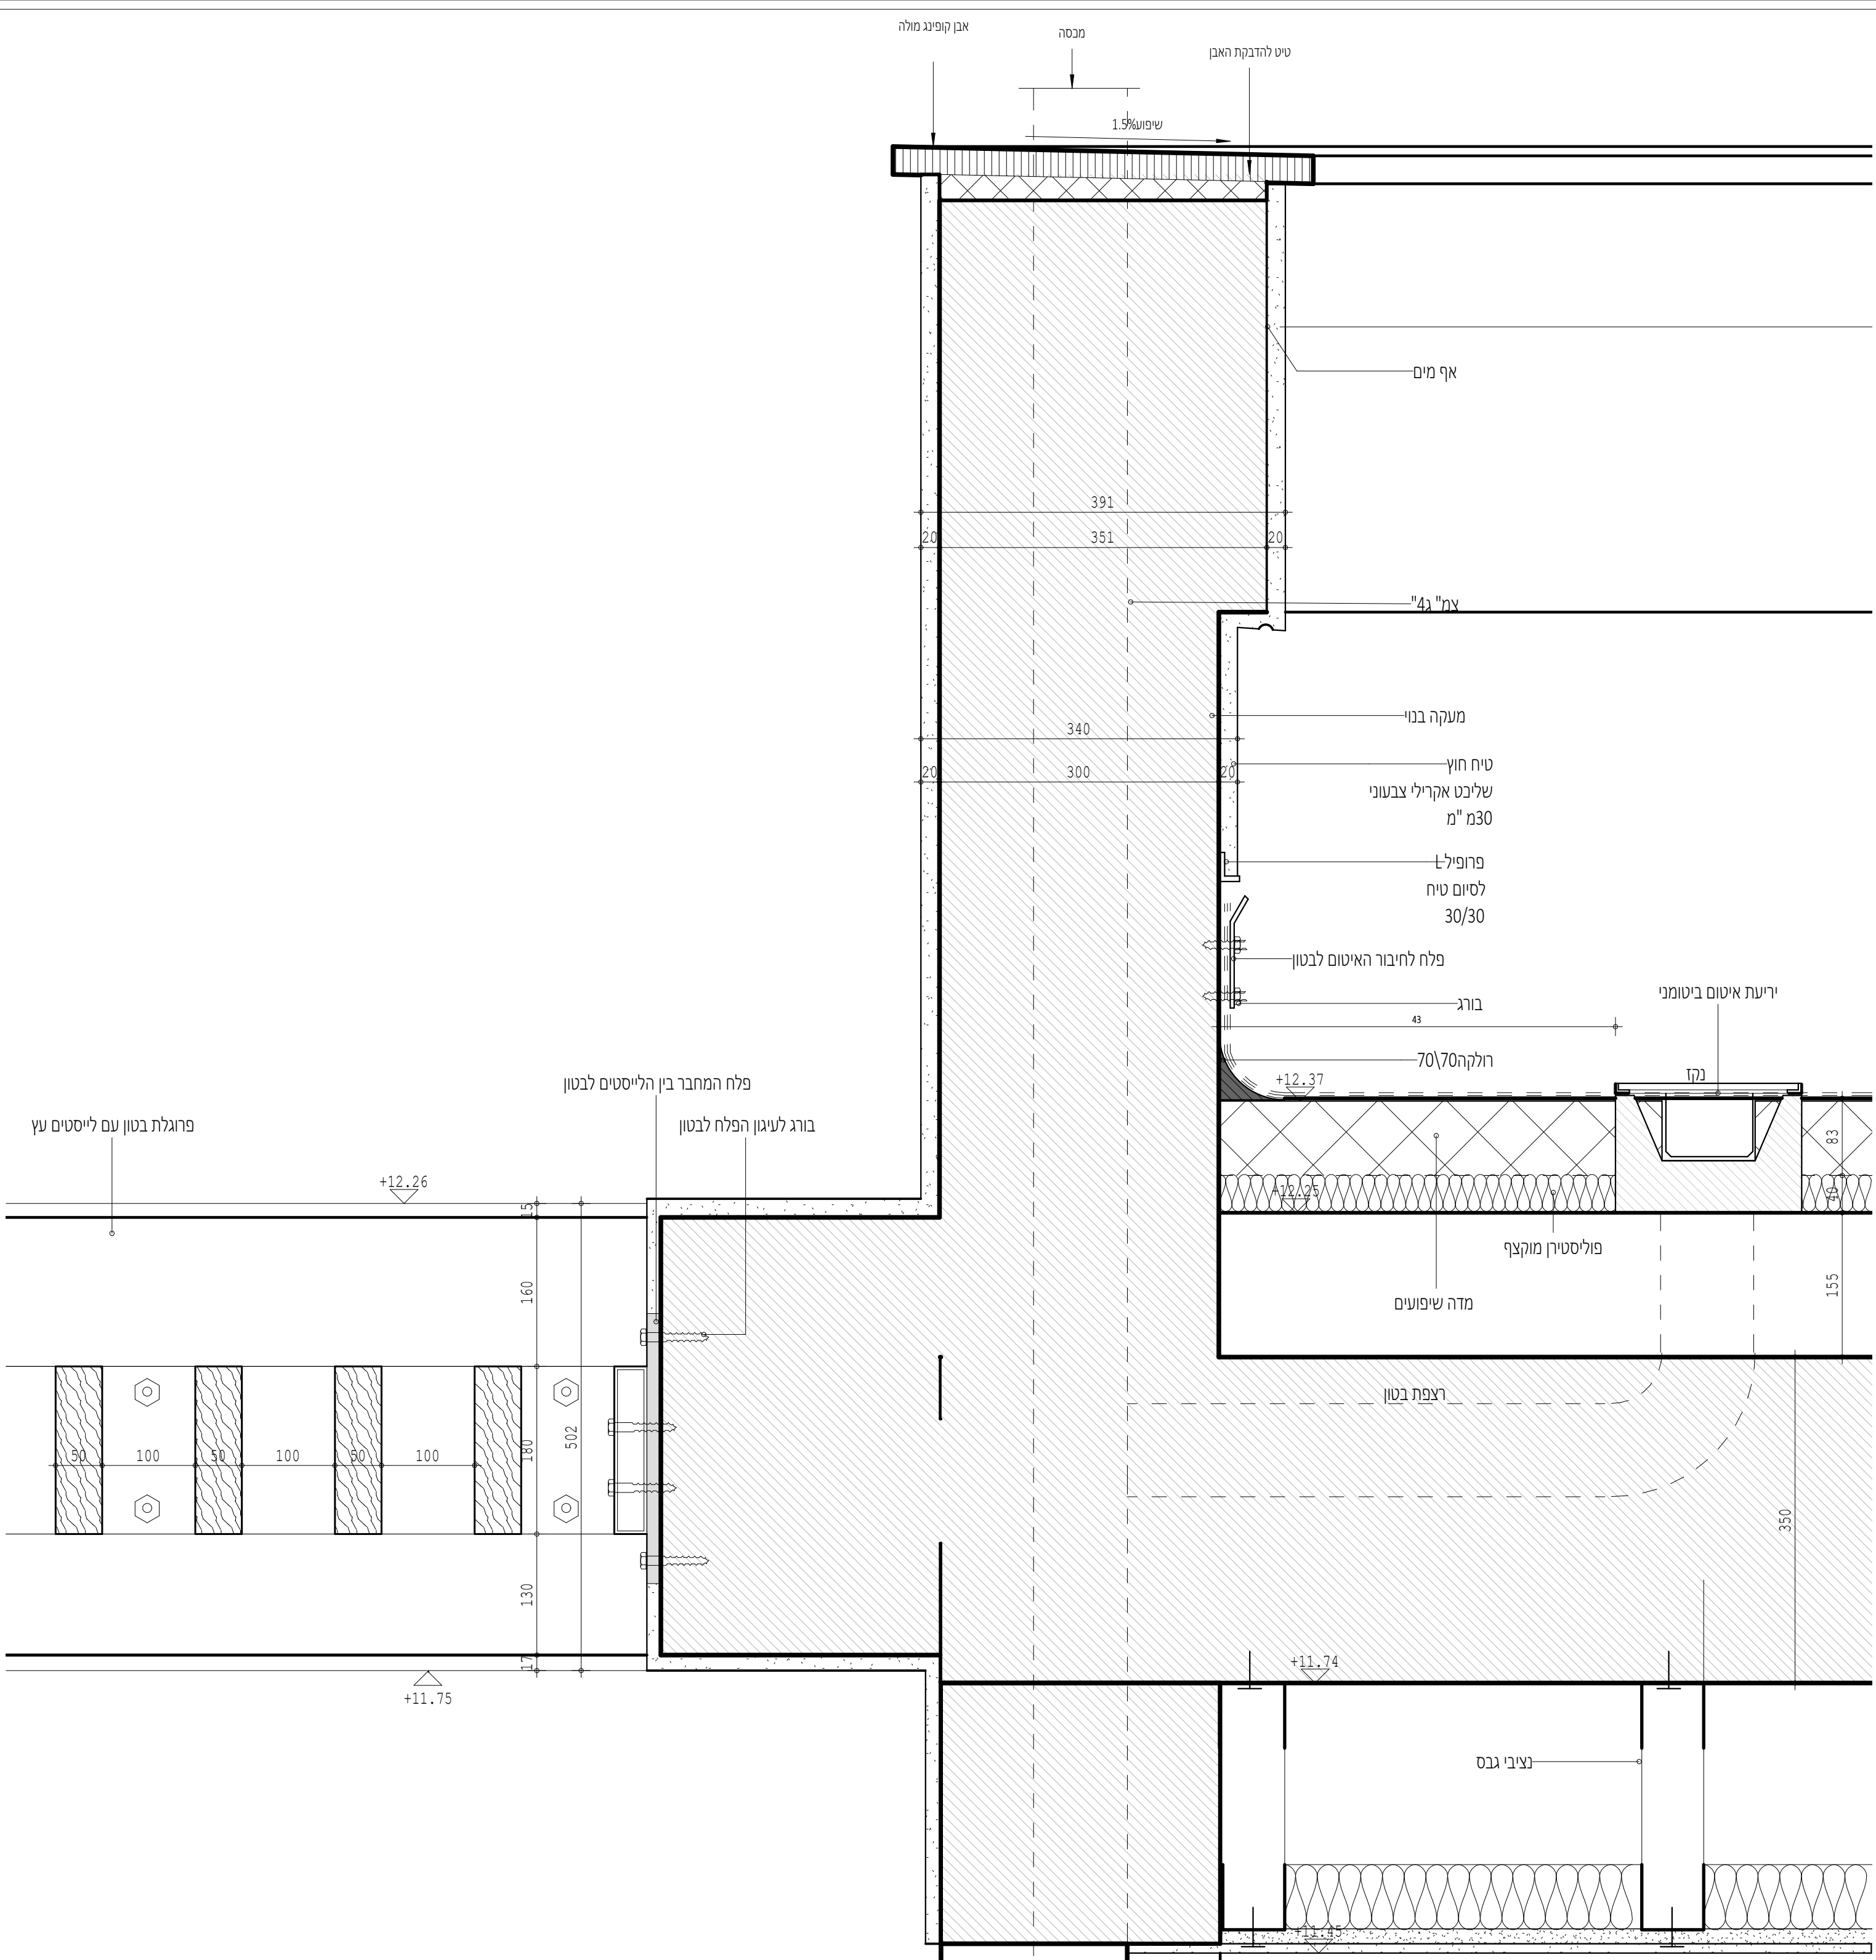

חוץ

פנים

פרט-גג טכני
1 : 5

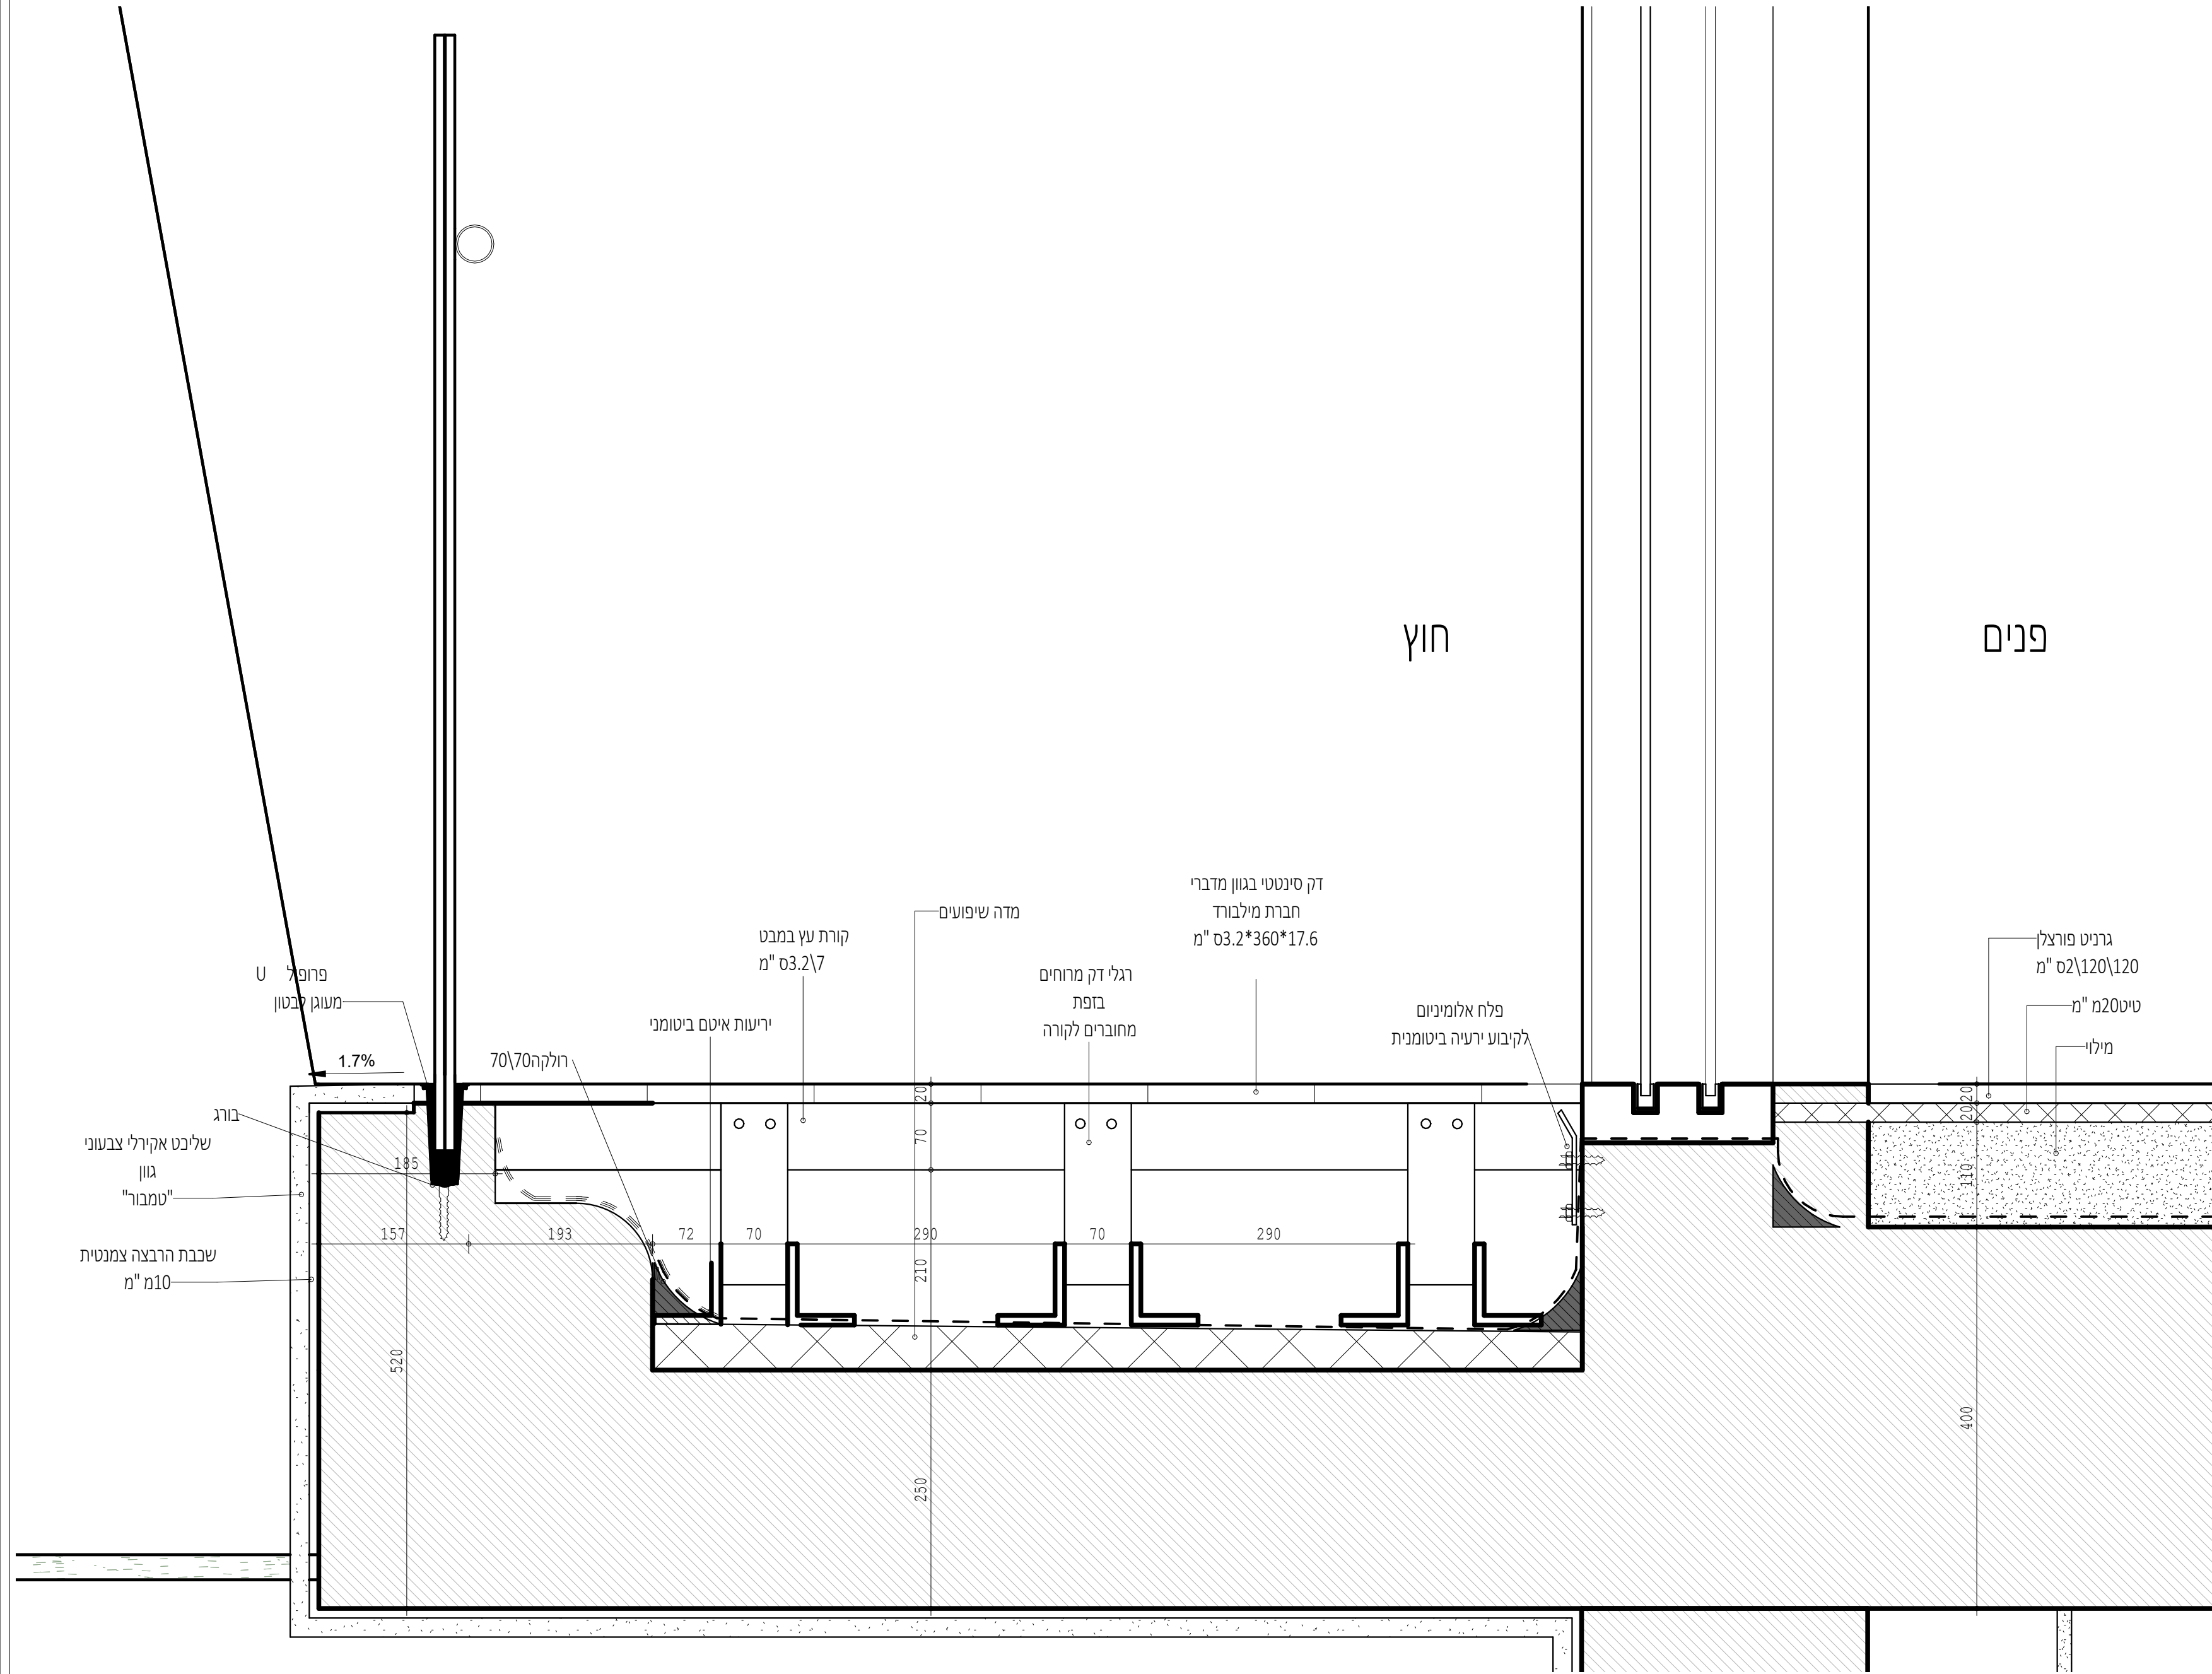

שם הפרויקט:

מעונות סטודנטים



מס'	תיאור גיליון:	קני'ם:
00	שער	
01	ניתוח סביבה	
02	קצוות -פרוגרמה	
03	הדמיות	

פיתוח שטח		
1:100	תכנית קומת קרקע	-04
1:100	תכנית קומה א'	05

תכנית שדור לבן	
תכנית קומת קרקע	1:100
תכנית קומה א	1:100
תכנית קומה ב	1:100
תכנית גגות	1:100
חזקים	1:100
חזיתות	1:100
חזיתות	1:100

תכניות עבודה	
תכנית עבודה קומה א	1:50
תוכן א'-א',י'-כ'	1:50
חזית צפוןית,מערבית	1:50

פרטי בניין	
מדרגות-תכניות, פרטים	1:50
מדרגות-חזקים	1:20
קיר ייחודי-חזקים	1:20
קיר ייחודי-פרטים	1:5

עיצוב פנים	
תכנית ריהוט, ריצוף	1:50
תכנית תקרה ומיזוג אוויר	1:50
הדמיות ופריסת קיר	1:50
תכנון דלפק	1:10

קונסטרוקציה
תכניות קונסטרוקציה

מגיש/ה:

כרמל סעדון

שם ראש המגמה:

שרון גפני

שם המנחה:


ליית'

תאריך:

23\06\2026



תכנית לוברים

1 : 5

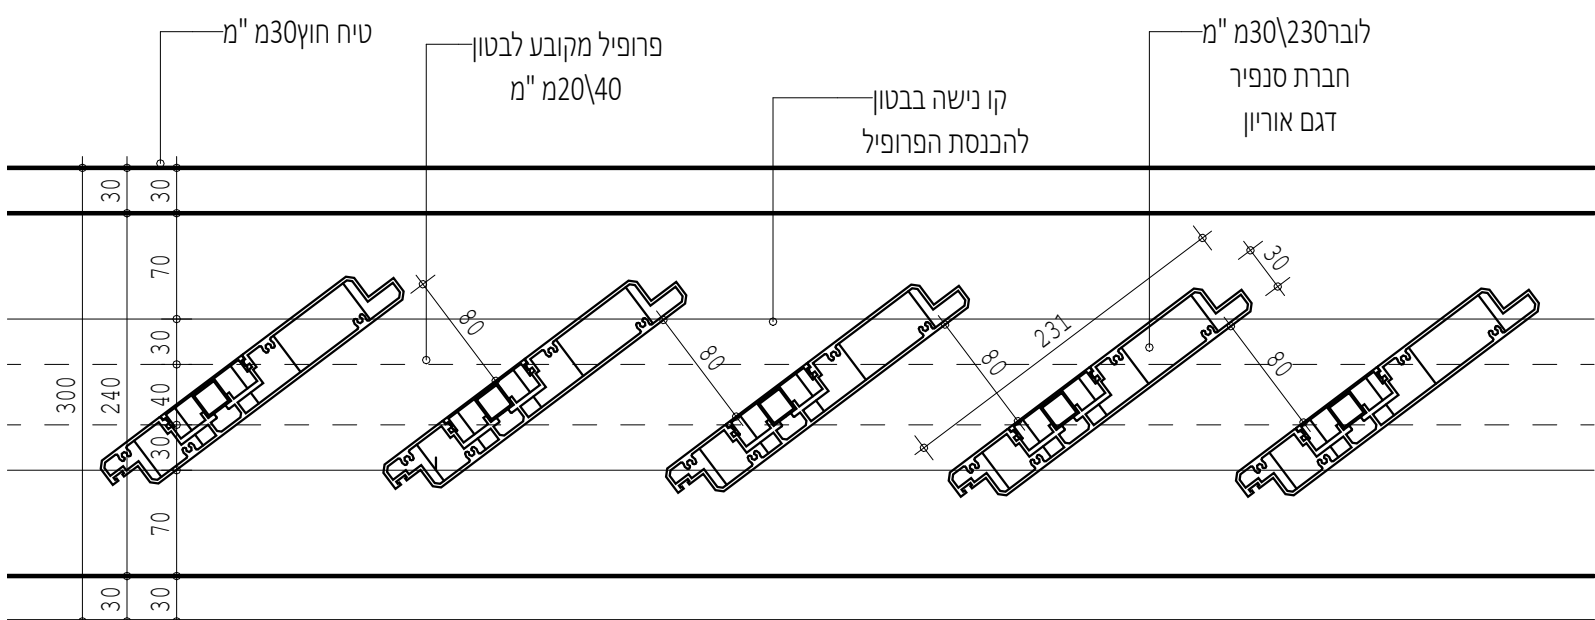


פרט גג ירוק

1 : 5

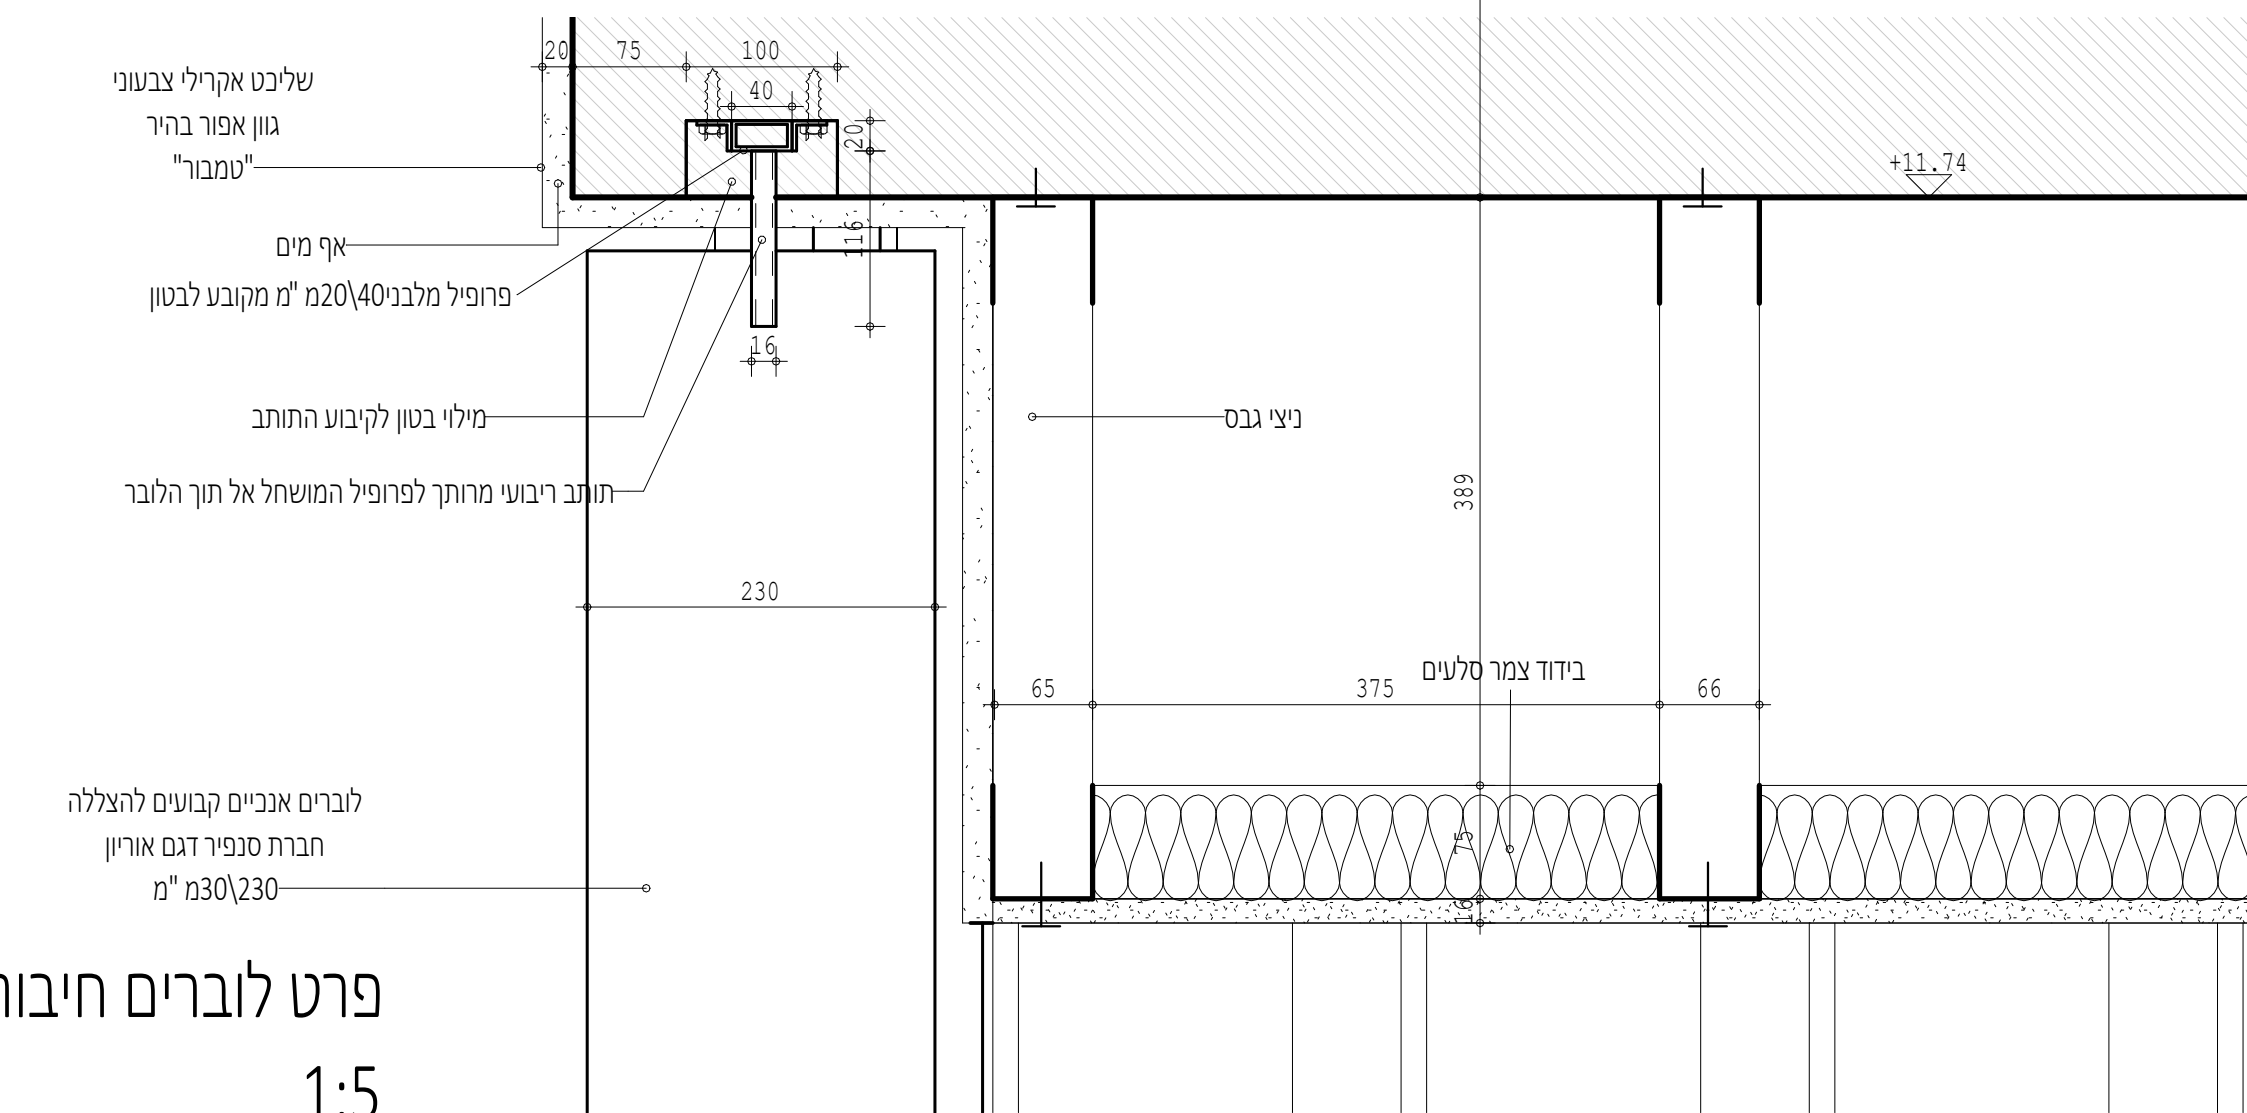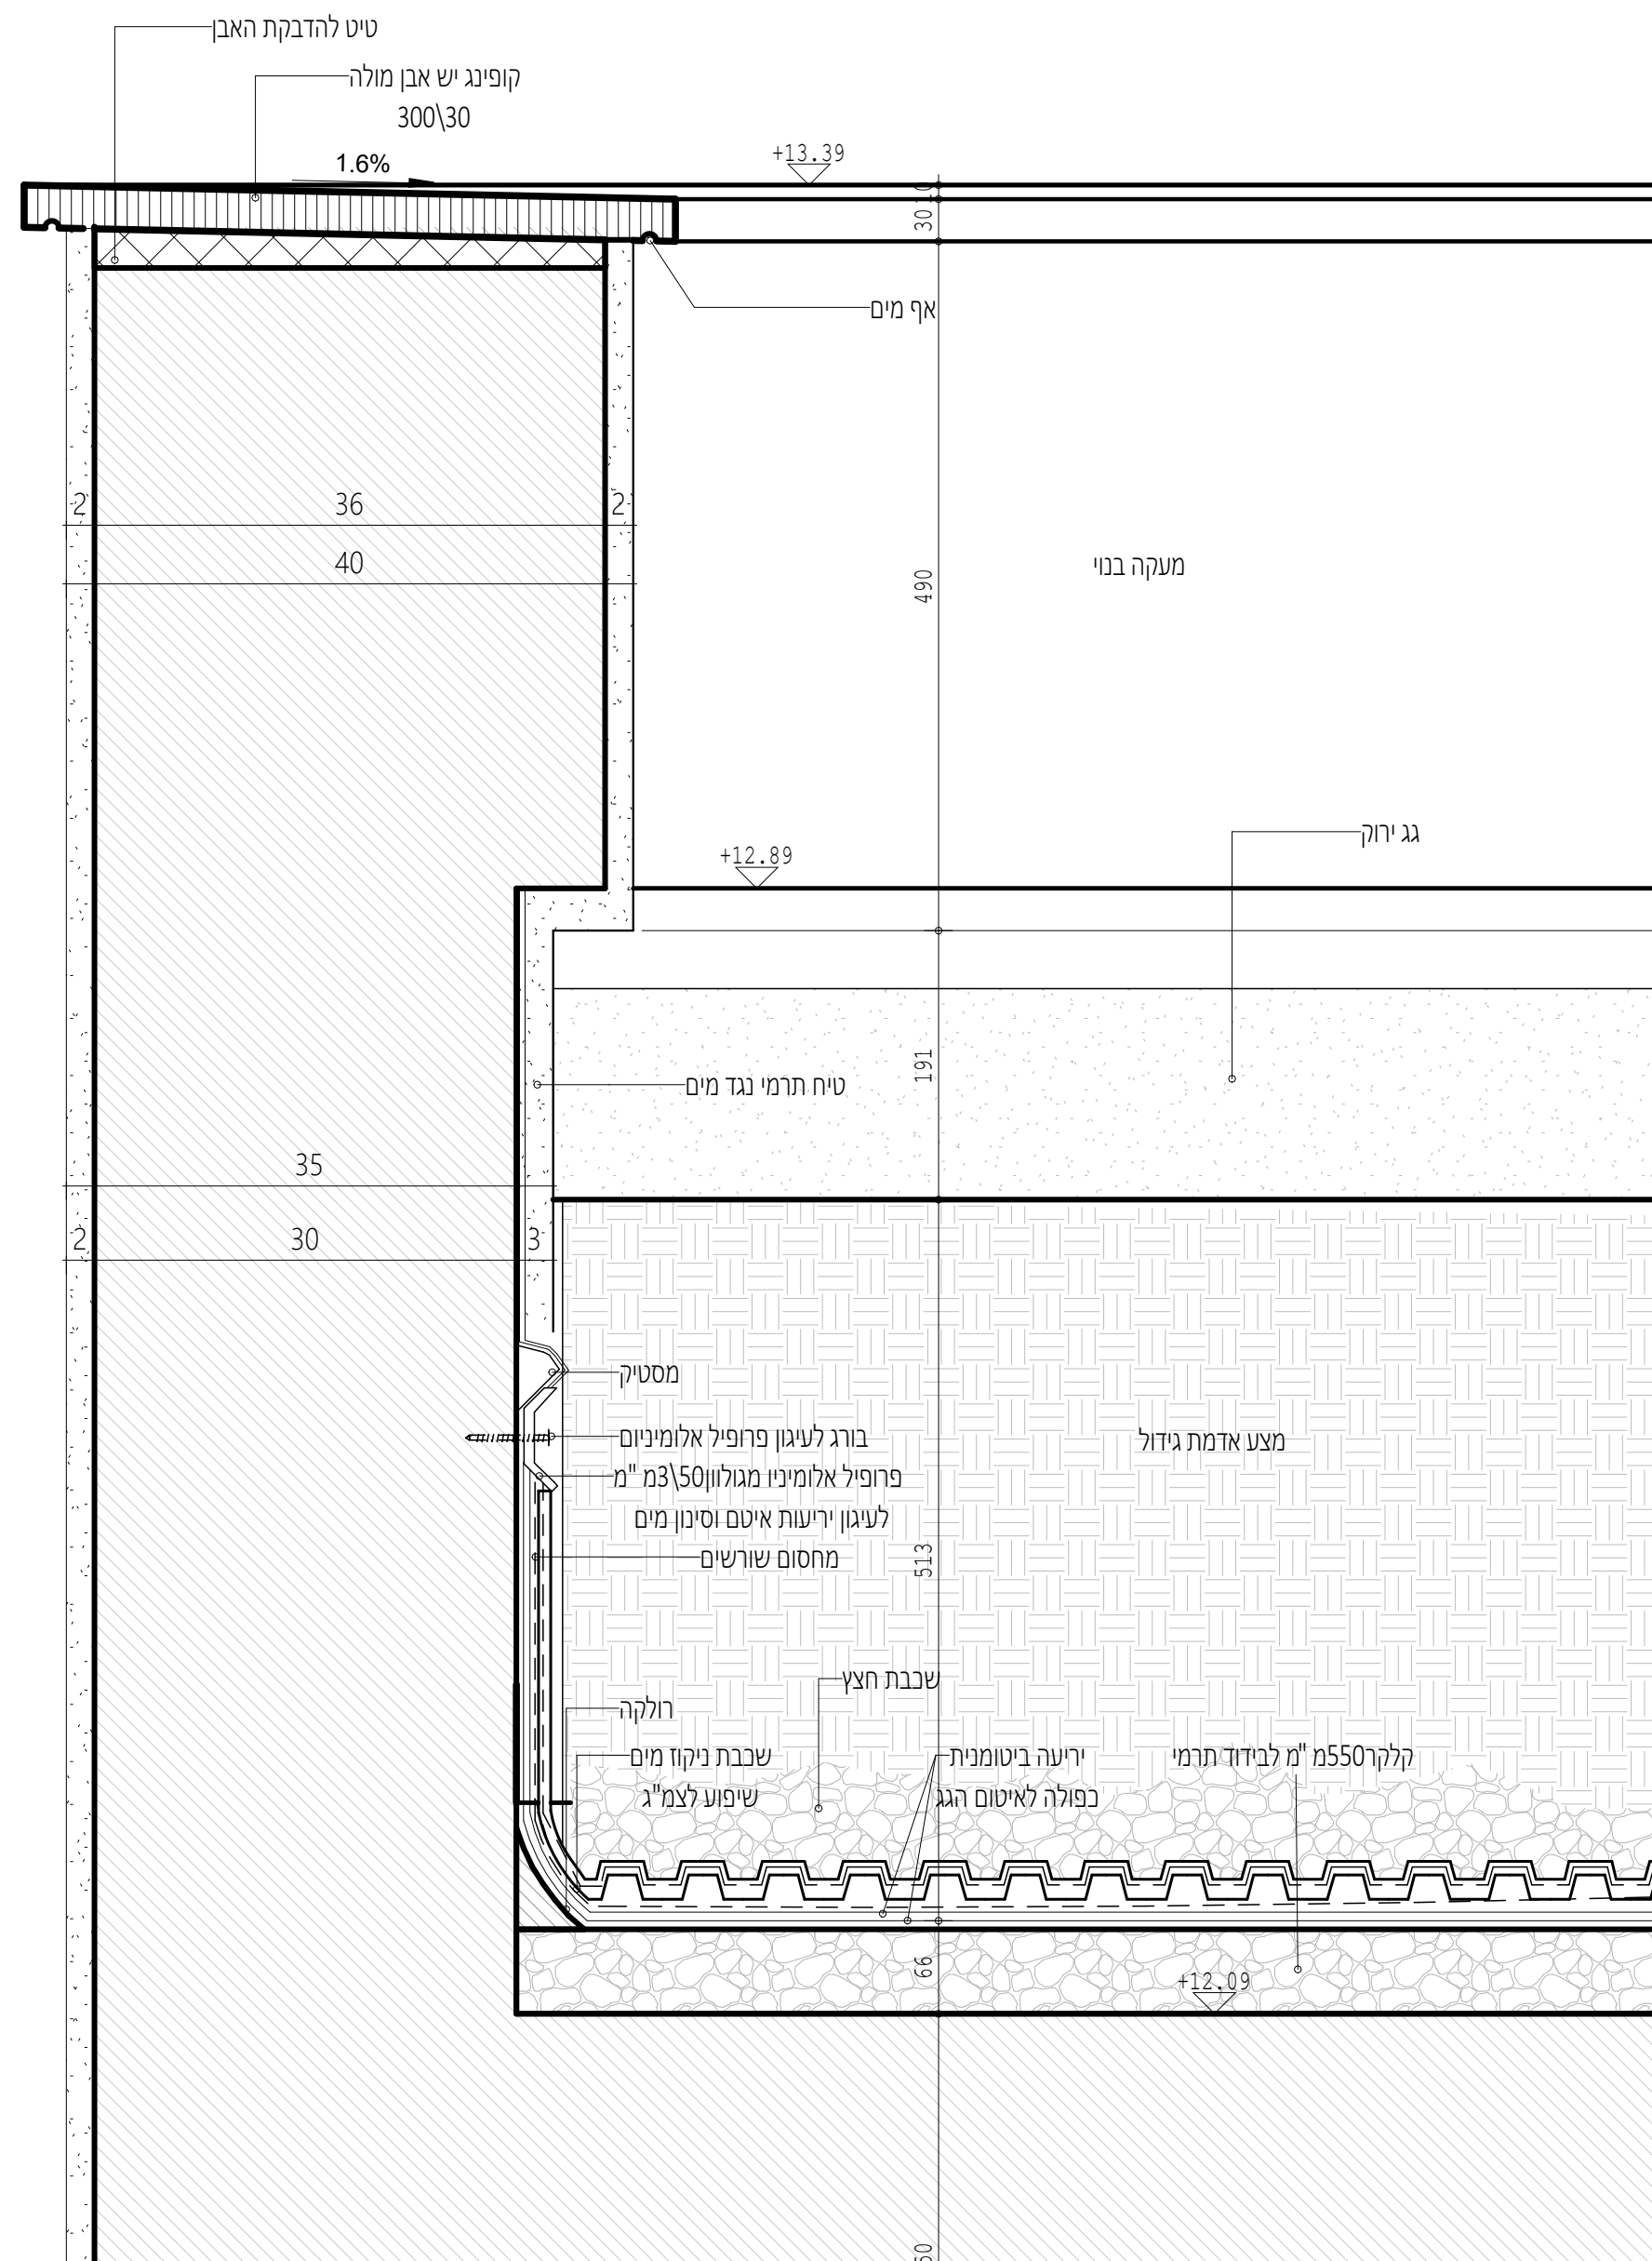


פרט לברים חיבור עליון

1:5

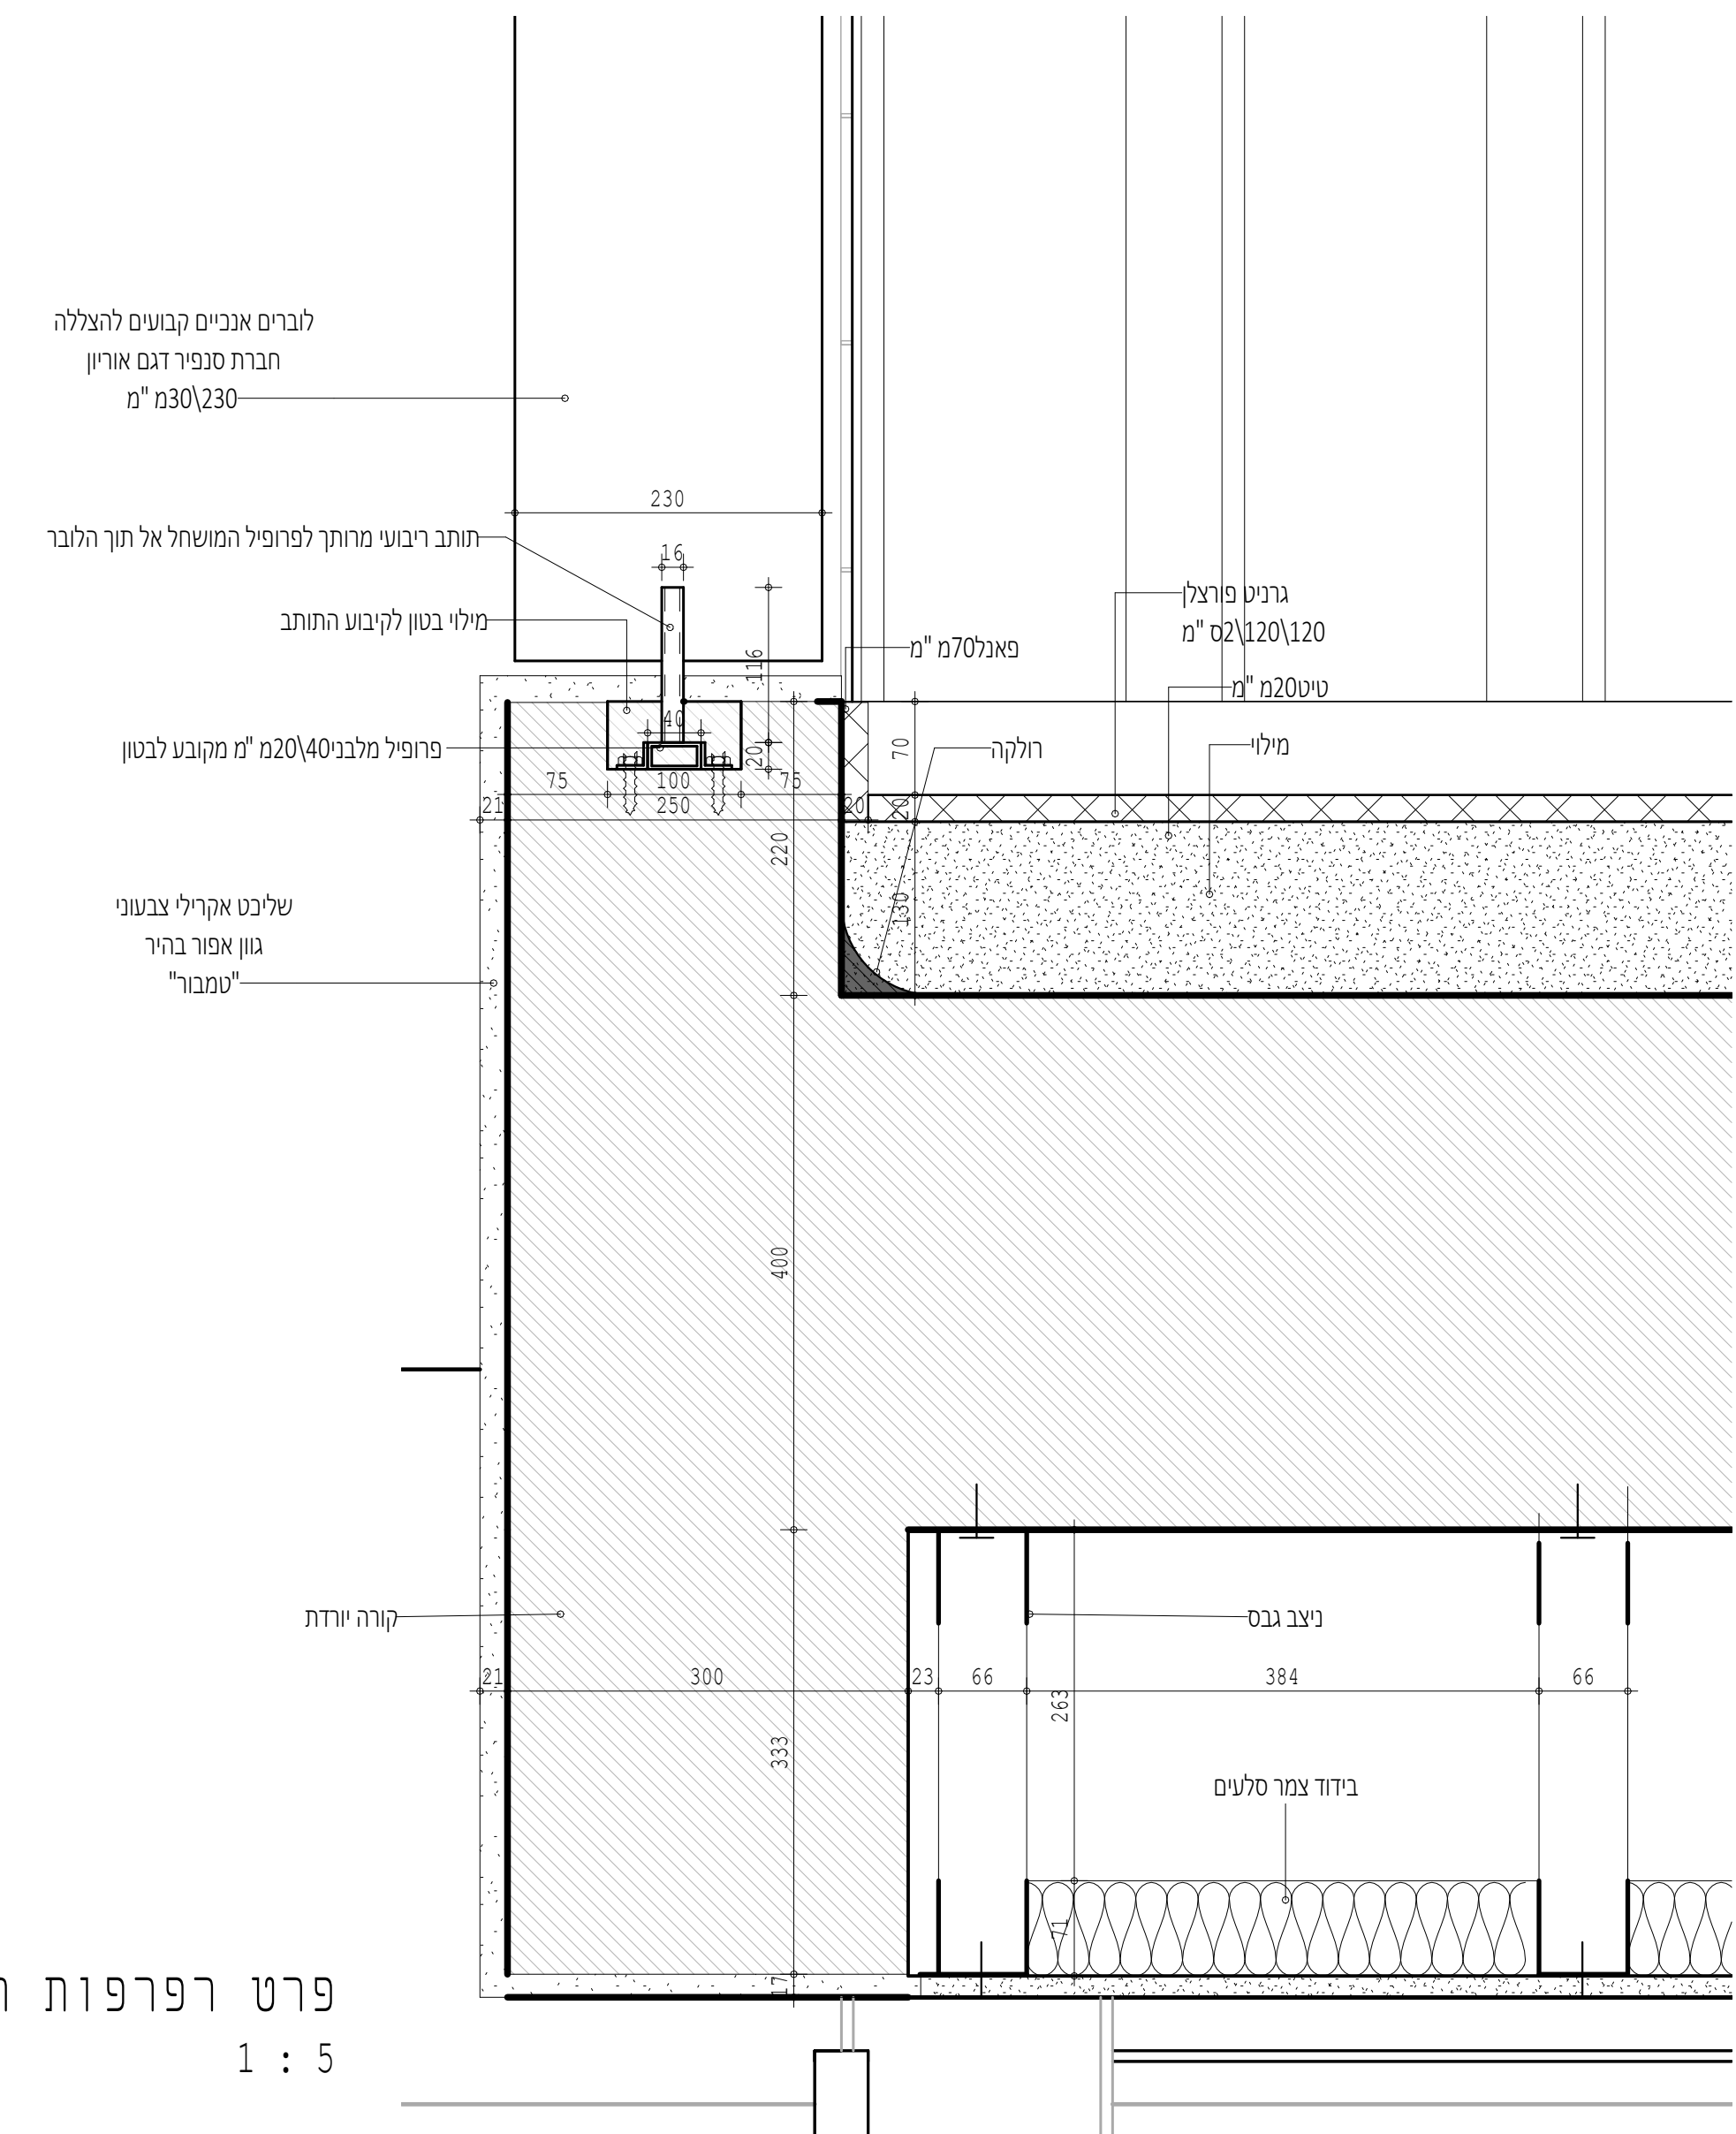


פרט רפרפות הצללה-תחתון

1 : 5

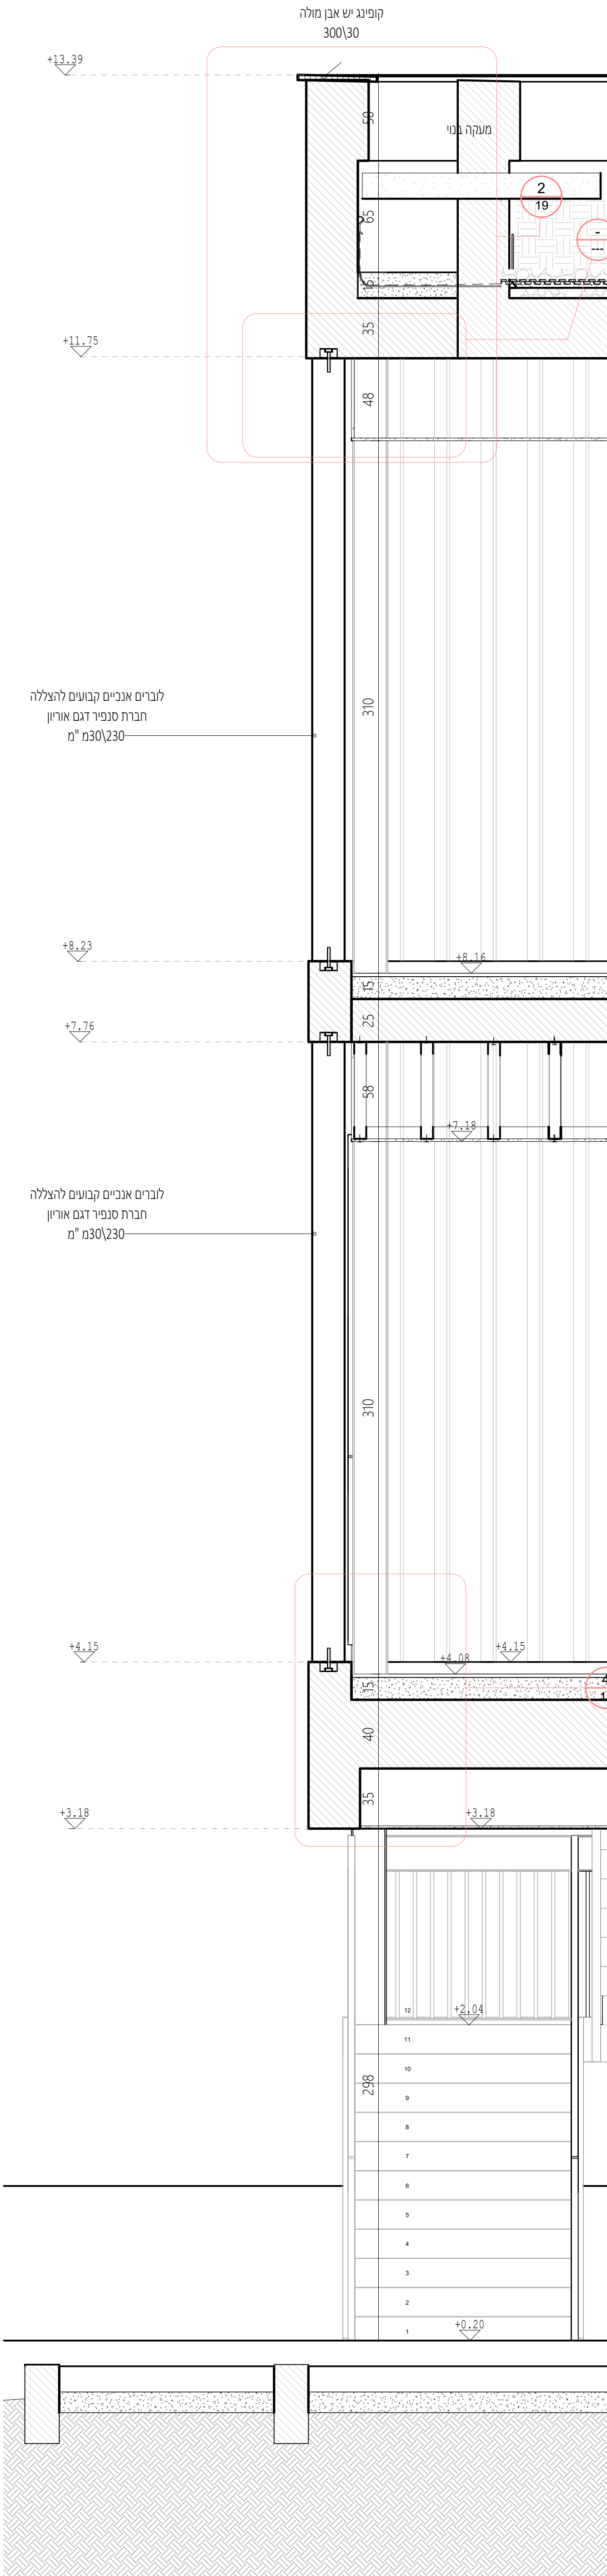

חתך פרטים

1 : 20

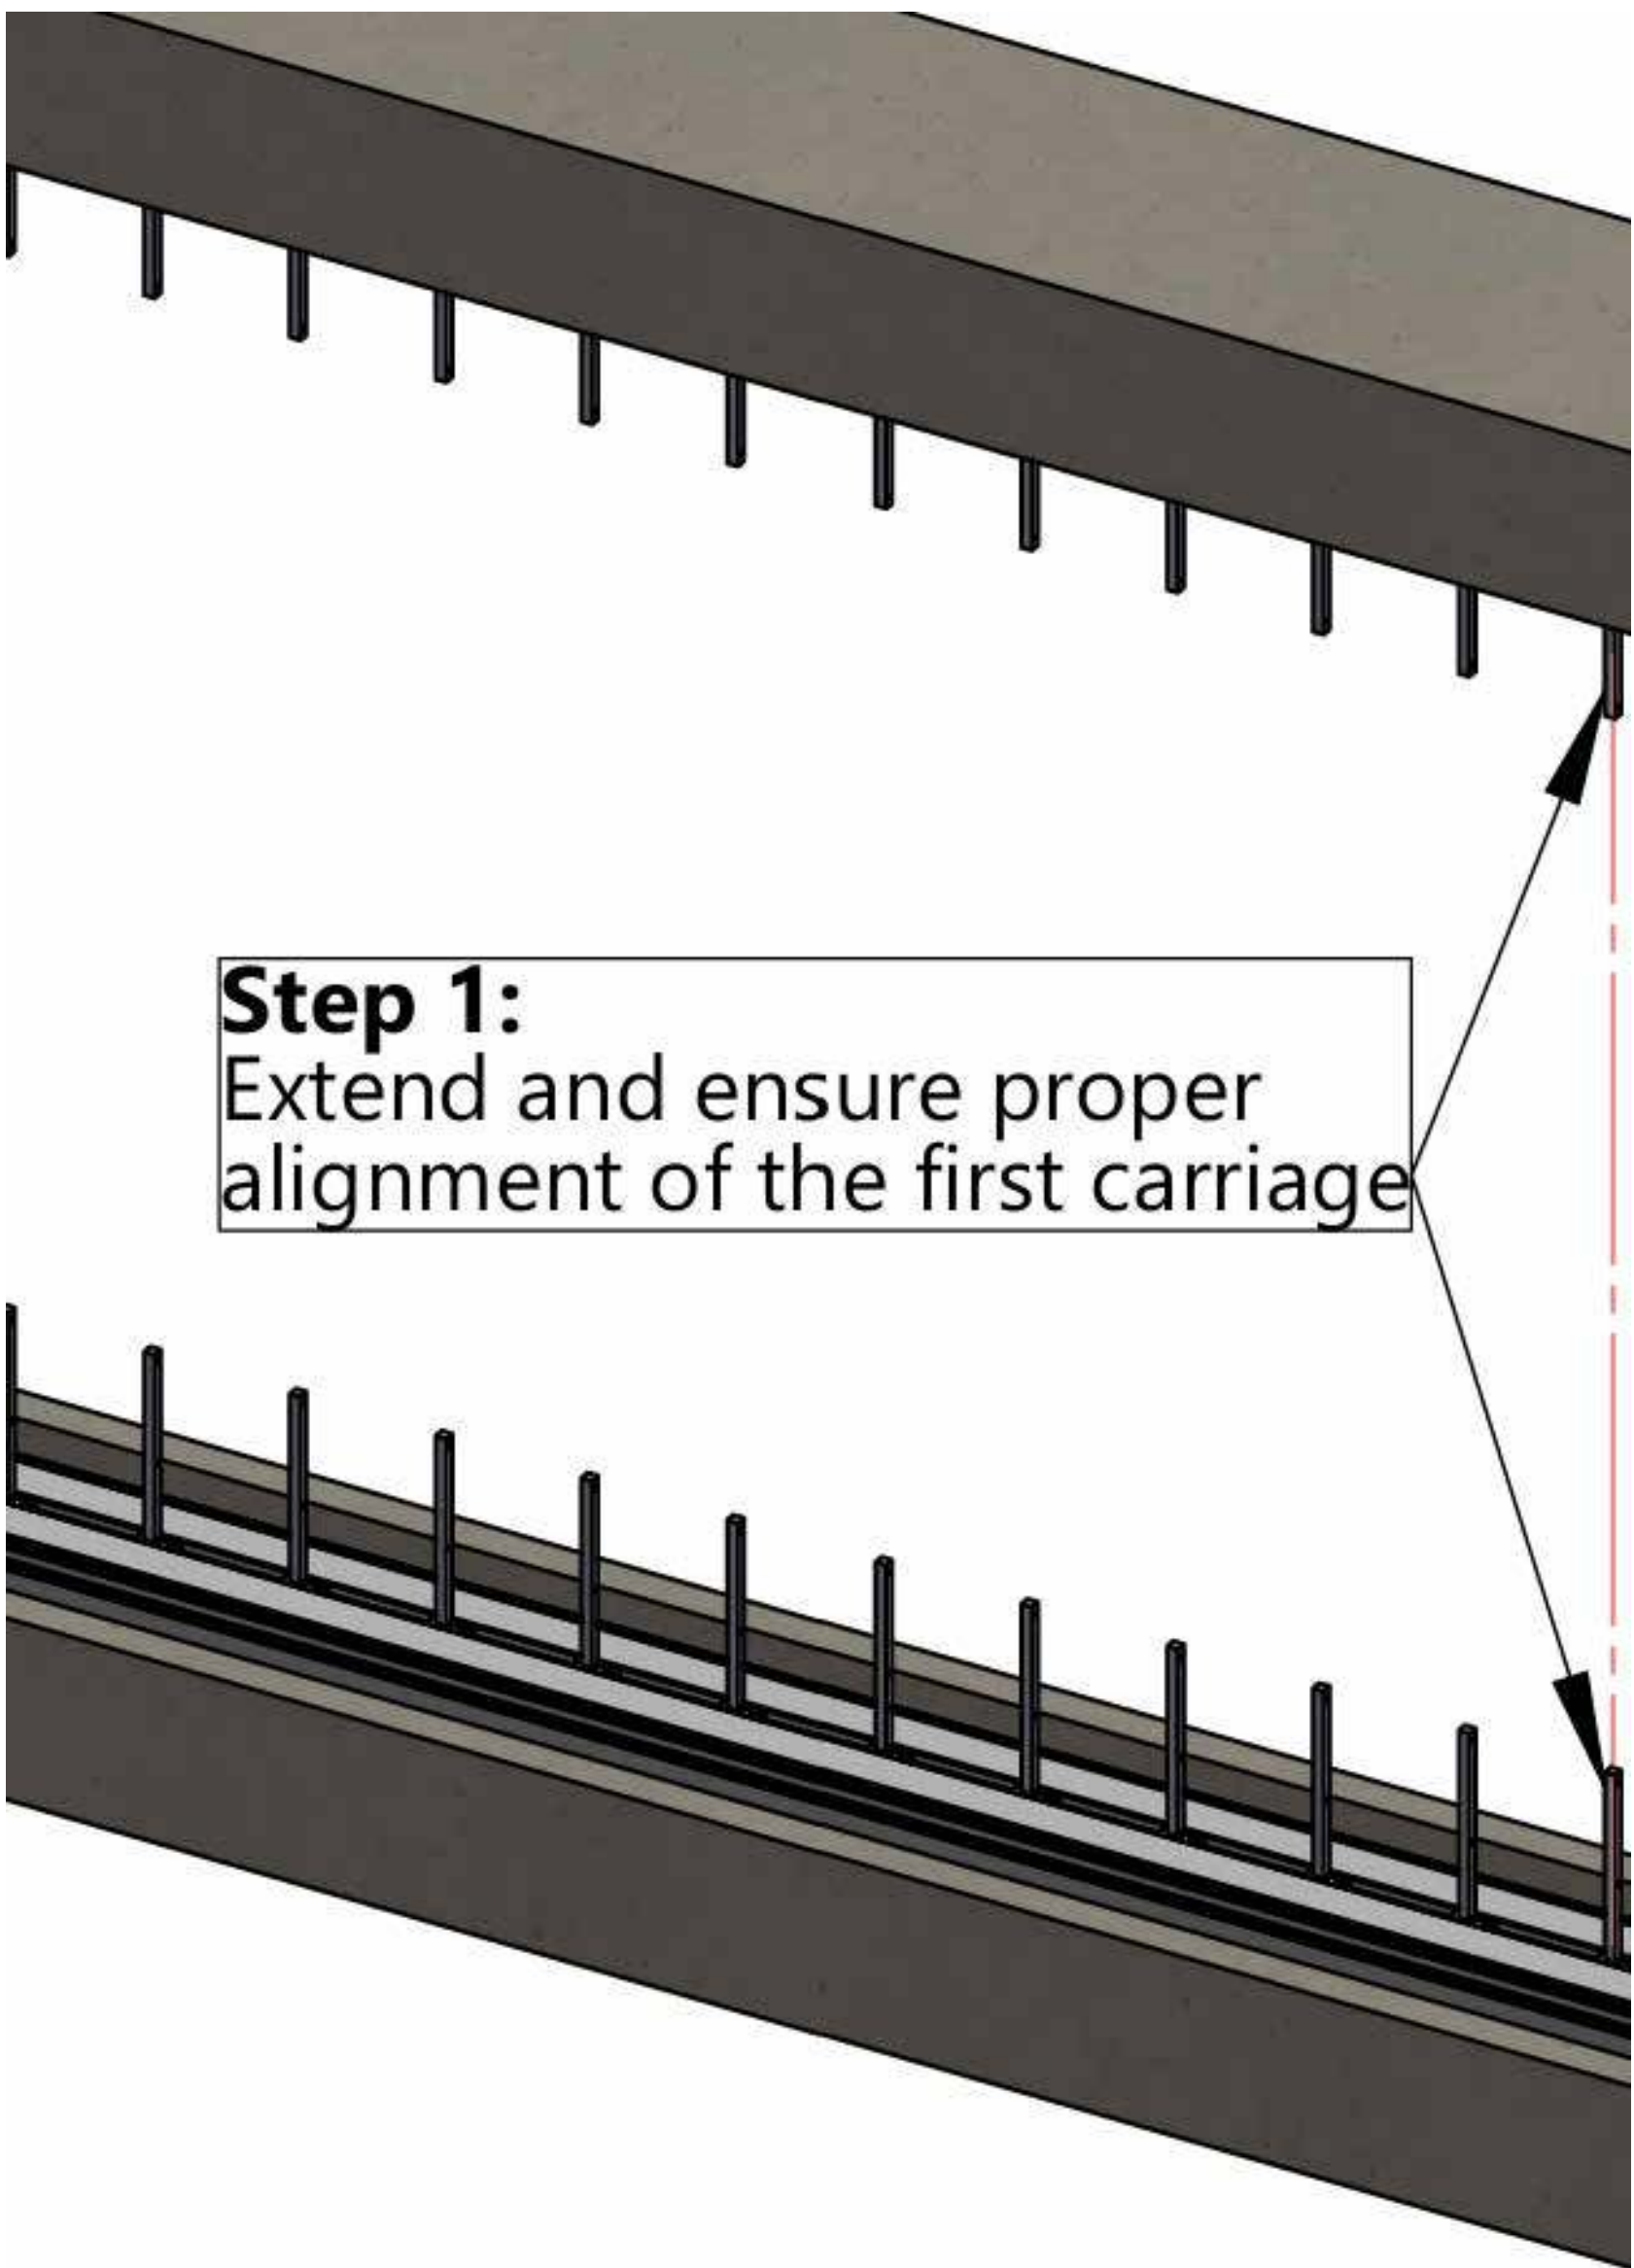

Step 1:
Extend and ensure proper
alignment of the first carriage

שם הפרויקט:
מעונות סטודנטיים



מס'	תיאור גיליון:	קב"מ:
-00	שער	
-01	ניתוח סביבה	
-02	סקיצות-פרוגרמה	
-03	הדמיות	

פיתוח שטח		
-04	תכנית קומת קרקע	1:100
-05	תכנית קומה א	1:100

תכנית שחור לבן		
-06	תכנית קומת קרקע	1:100
-07	תכנית קומה א	1:100
-08	תכנית קומה ב	1:100
-09	תכנית גגות	1:100
-10	חתכים	1:100
-11	חזיתות	1:100
-12	חזיתות	1:100

תכנית עבודה		
-13	תכנית עבודה קומה א	1:50
-14	חתך א'-א' ב'-ב'	1:50
-15	חזית צפונית, מערבית	1:50

פרטי בנין		
-16	מדרגות-תכנית, פרטים	1:20 1:5
-17	מדרגות-חתכים	1:20
-18	קיר ייחודי-חתכים	1:20
-19	קיר ייחודי-פרטים	1:5

עיצוב פנים		
-20	תכנית ריהוט, ריצוף	1:50
-21	תכנית תקרה ופנורמא	1:50
-22	הדמיות ופריסת קיר	1:50
-23	תכנון דלפק	1:10 1:20
-24	עיצוב חדר לדוגמא	1:50

קונסטרוקציה		
-25	תכנית קונסטרוקציה	1:100

מגיש/ה:

כרמל שעדון

שם ראש המגמה:

שרון גפני

שם המנחה:

ליית'

תאריך:

23\06\2026


תוכנית עיצוב פנים קרקע

1 : 50



תכנית ריצוף

1 : 50

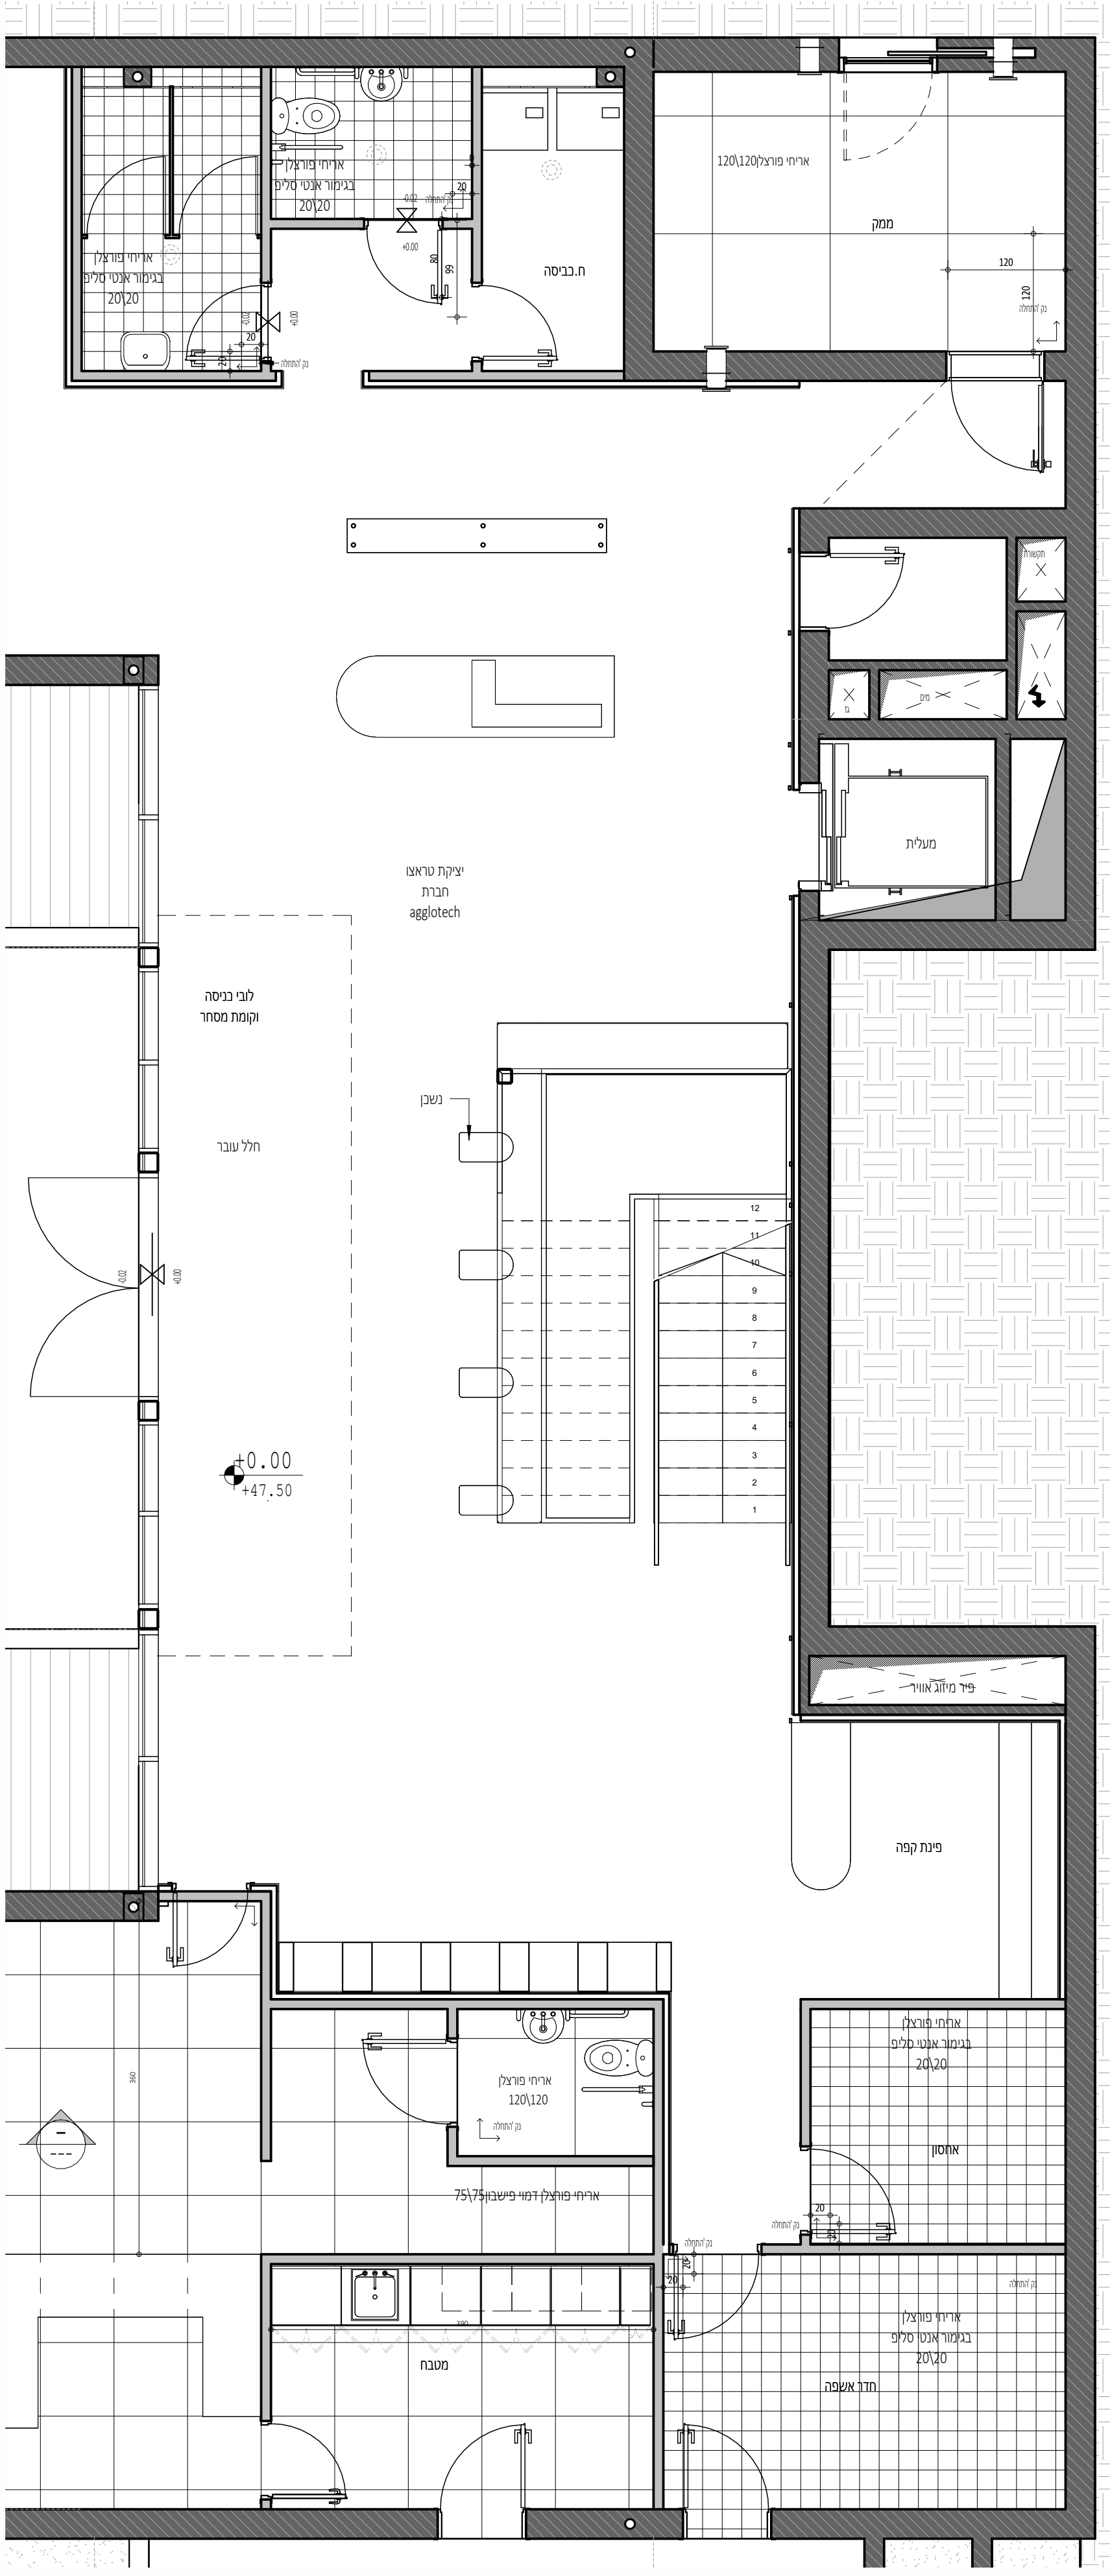

לובי-ציקת טראצו
חברת agglotech



בית קפה- אריחי פורצלן דמוי פרקט75\75
חברת ALONY



שירותים-
אריחי פורצלן120\120
חברת ALONY



שם הפרויקט:

מעונות סטודנטים



מס'	תיאור גיליון:	קמ"מ:
-00	שער	
-01	ניתוח סביבה	
-02	סקיצות פרוגרמה	
-03	הדמיות	

פיתוח שטח	1:100
תכנית קומת קרקע	1:100
תכנית קומה א	1:100

תכנית שחור לבן	1:100
תכנית קומת קרקע	1:100
תכנית קומה א	1:100
תכנית קומה ב	1:100
תכנית גגות	1:100
חתכים	1:100
חזיתות	1:100
חזיתות	1:100

תכנית עבודה	1:50
תכנית עבודה קומה א	1:50
חתך א-א', ב-ב'	1:50
חזית צפונית, מערבית	1:50

פרטי ביניים	1:5
מדרגות-תכניות, פרטים	1:20
מדרגות-חתכים	1:20
קר ייחודי-חתכים	1:20
קר ייחודי-פרטים	1:5

עיצוב פנים	1:50
תכנית ריהוט, ריצוף	1:50
תכנית חקיה ממוגז	1:50
הדמיות ופריסת קיר	1:50
תכנון דלפק	1:20
עיצוב חדר לדוגמא	1:50

קונסטרוקציה	1:100
תכנית קונסטרוקציה	1:100

מגישה/:

ברמל סעדון

שם ראש הממנה:

שרון גפני

שם הממנה:

ליית'

תאריך:

23\06\2026




מבט מהכניסה לפינת קפה



מבט מהכניסה לדלפק קבלה


חתך עיצוב פנים
1 : 25

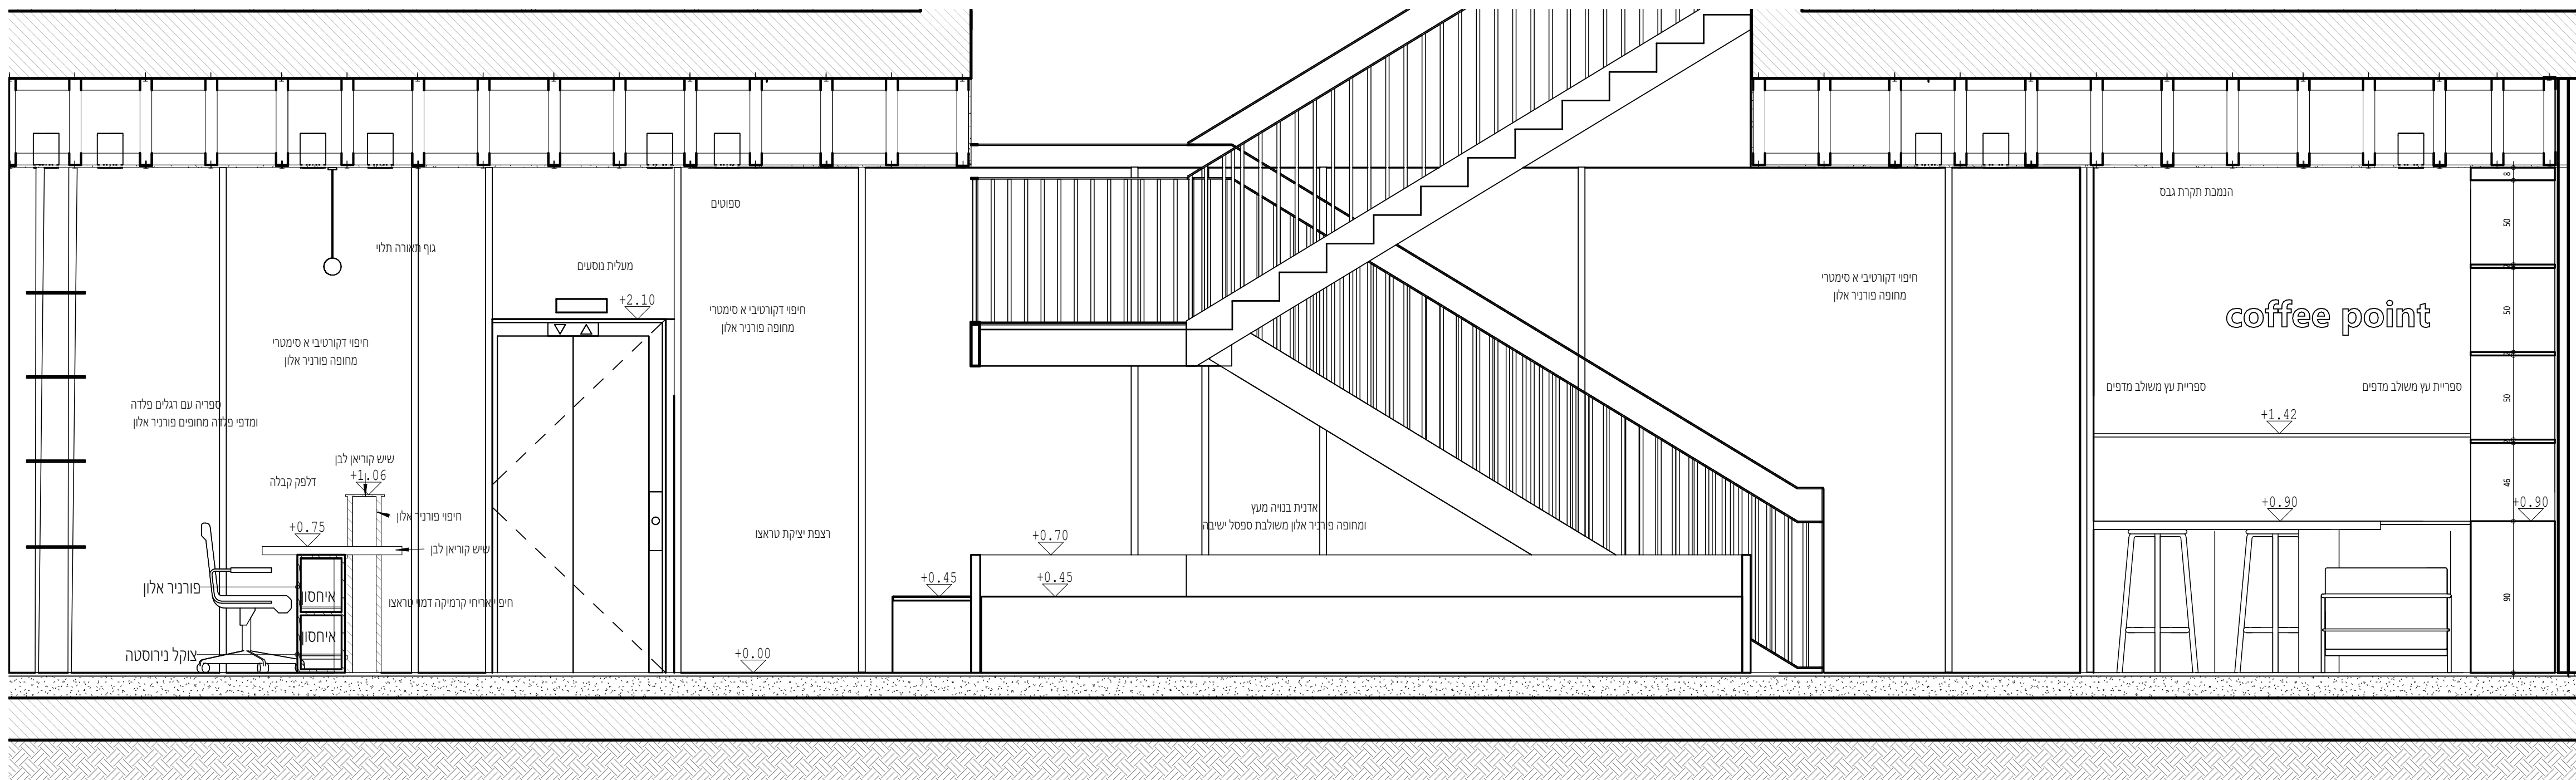





תכנית עבודה		
1:50	תכנית עבודה קומה א	-13
1:50	חוק א'-ב' ב'	-14
1:50	חזית צפופית, מעברית	-15
	פרט ביני	
1:20	מדרגות תכנית, פרטים	-16
1:20	מדרגות-חיתוכים	-17
1:20	קיר ייחוד-חיתוכים	-18
1:5	קיר ייחוד-פרטים	-19
	עצוב פנים	
1:50	תכנית ריהוט, ריצוף	-20
1:50	תכנית חתך ושטח ייחוד	-21
1:50	הדמיות ופרסית קיר	-22
1:10	תכנית דלת	-23
1:50	עיצוב חדר לובי	-24
	קונסטרוקציה	
1:100	תכנית קונסטרוקציה	-25

תאריך:

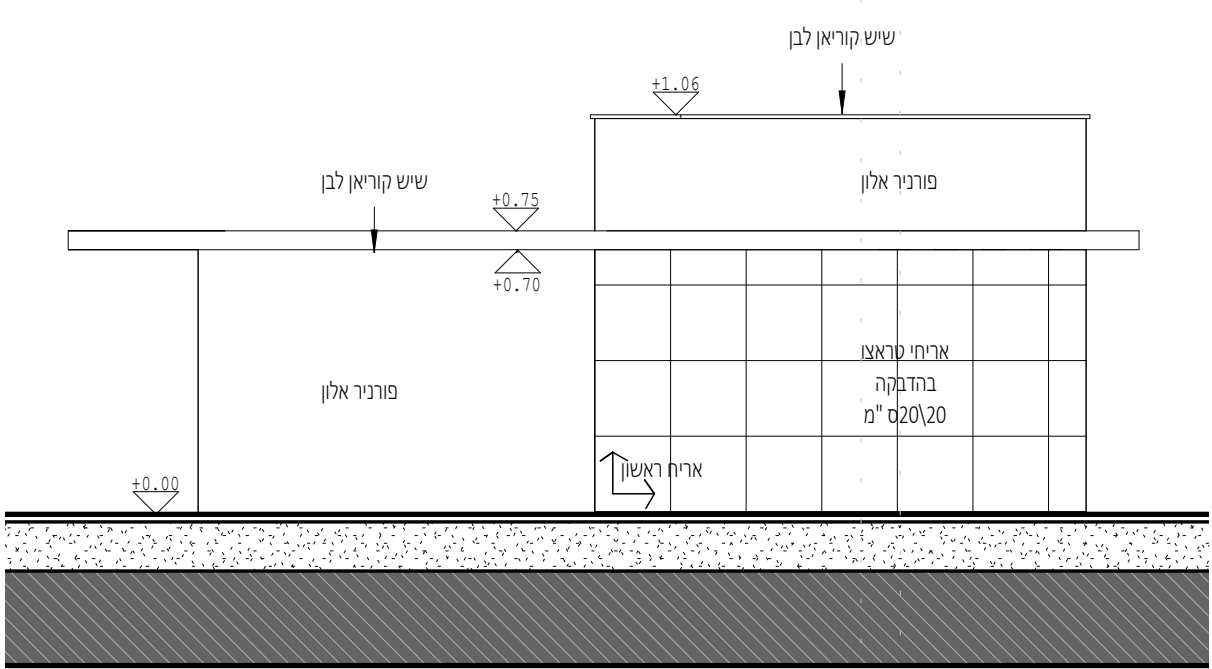

Architectural section AA of a building, showing a cross-section through the main structure. The section includes a ground floor with a large central hall (אזור שירות) and several rooms (אחסון, מציור, מציור איחסון). The roof is shown with a flat surface and a central section labeled 'שיש קוריאן' (Corian stone). The section is marked with dimensions and elevations. The drawing is oriented with a north arrow pointing upwards.

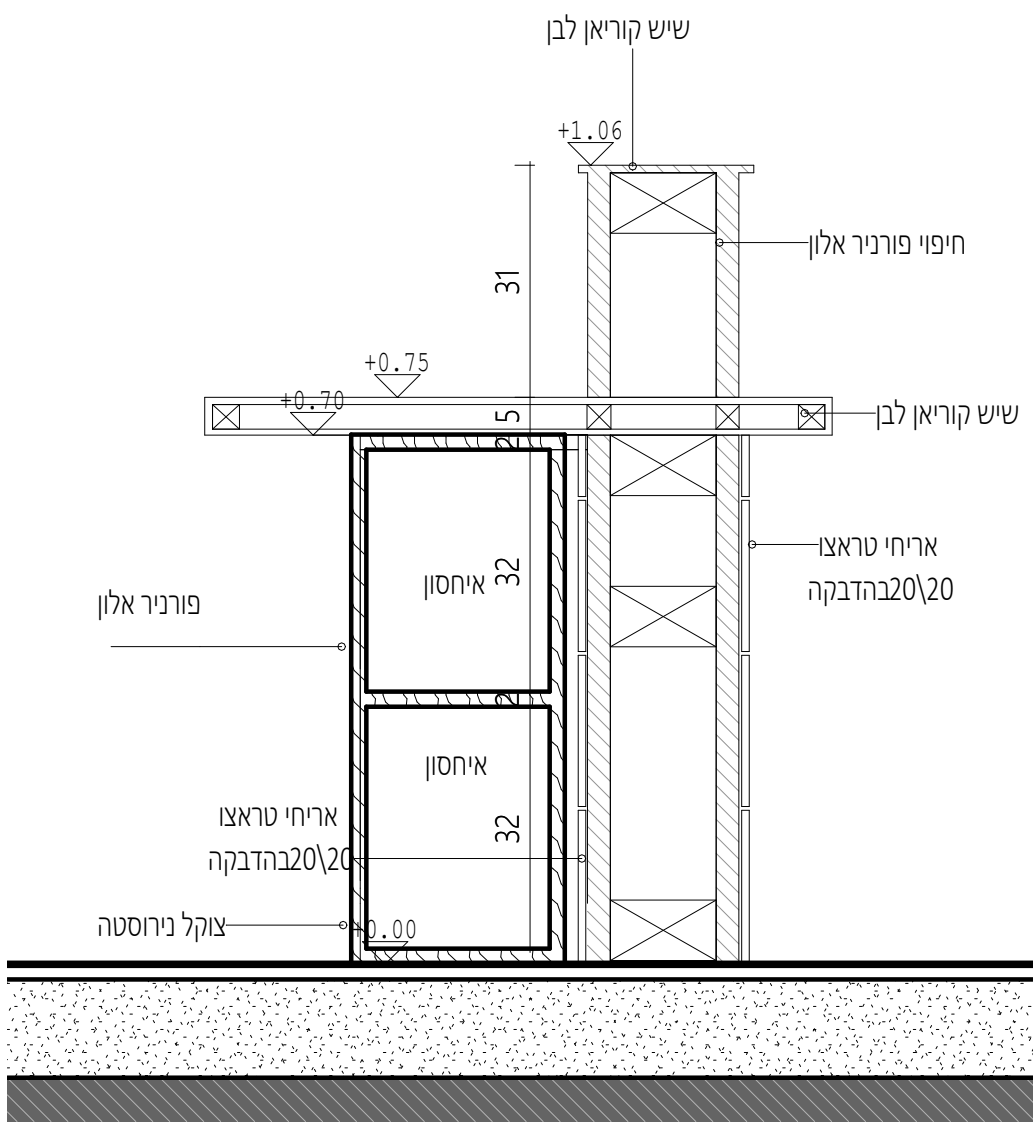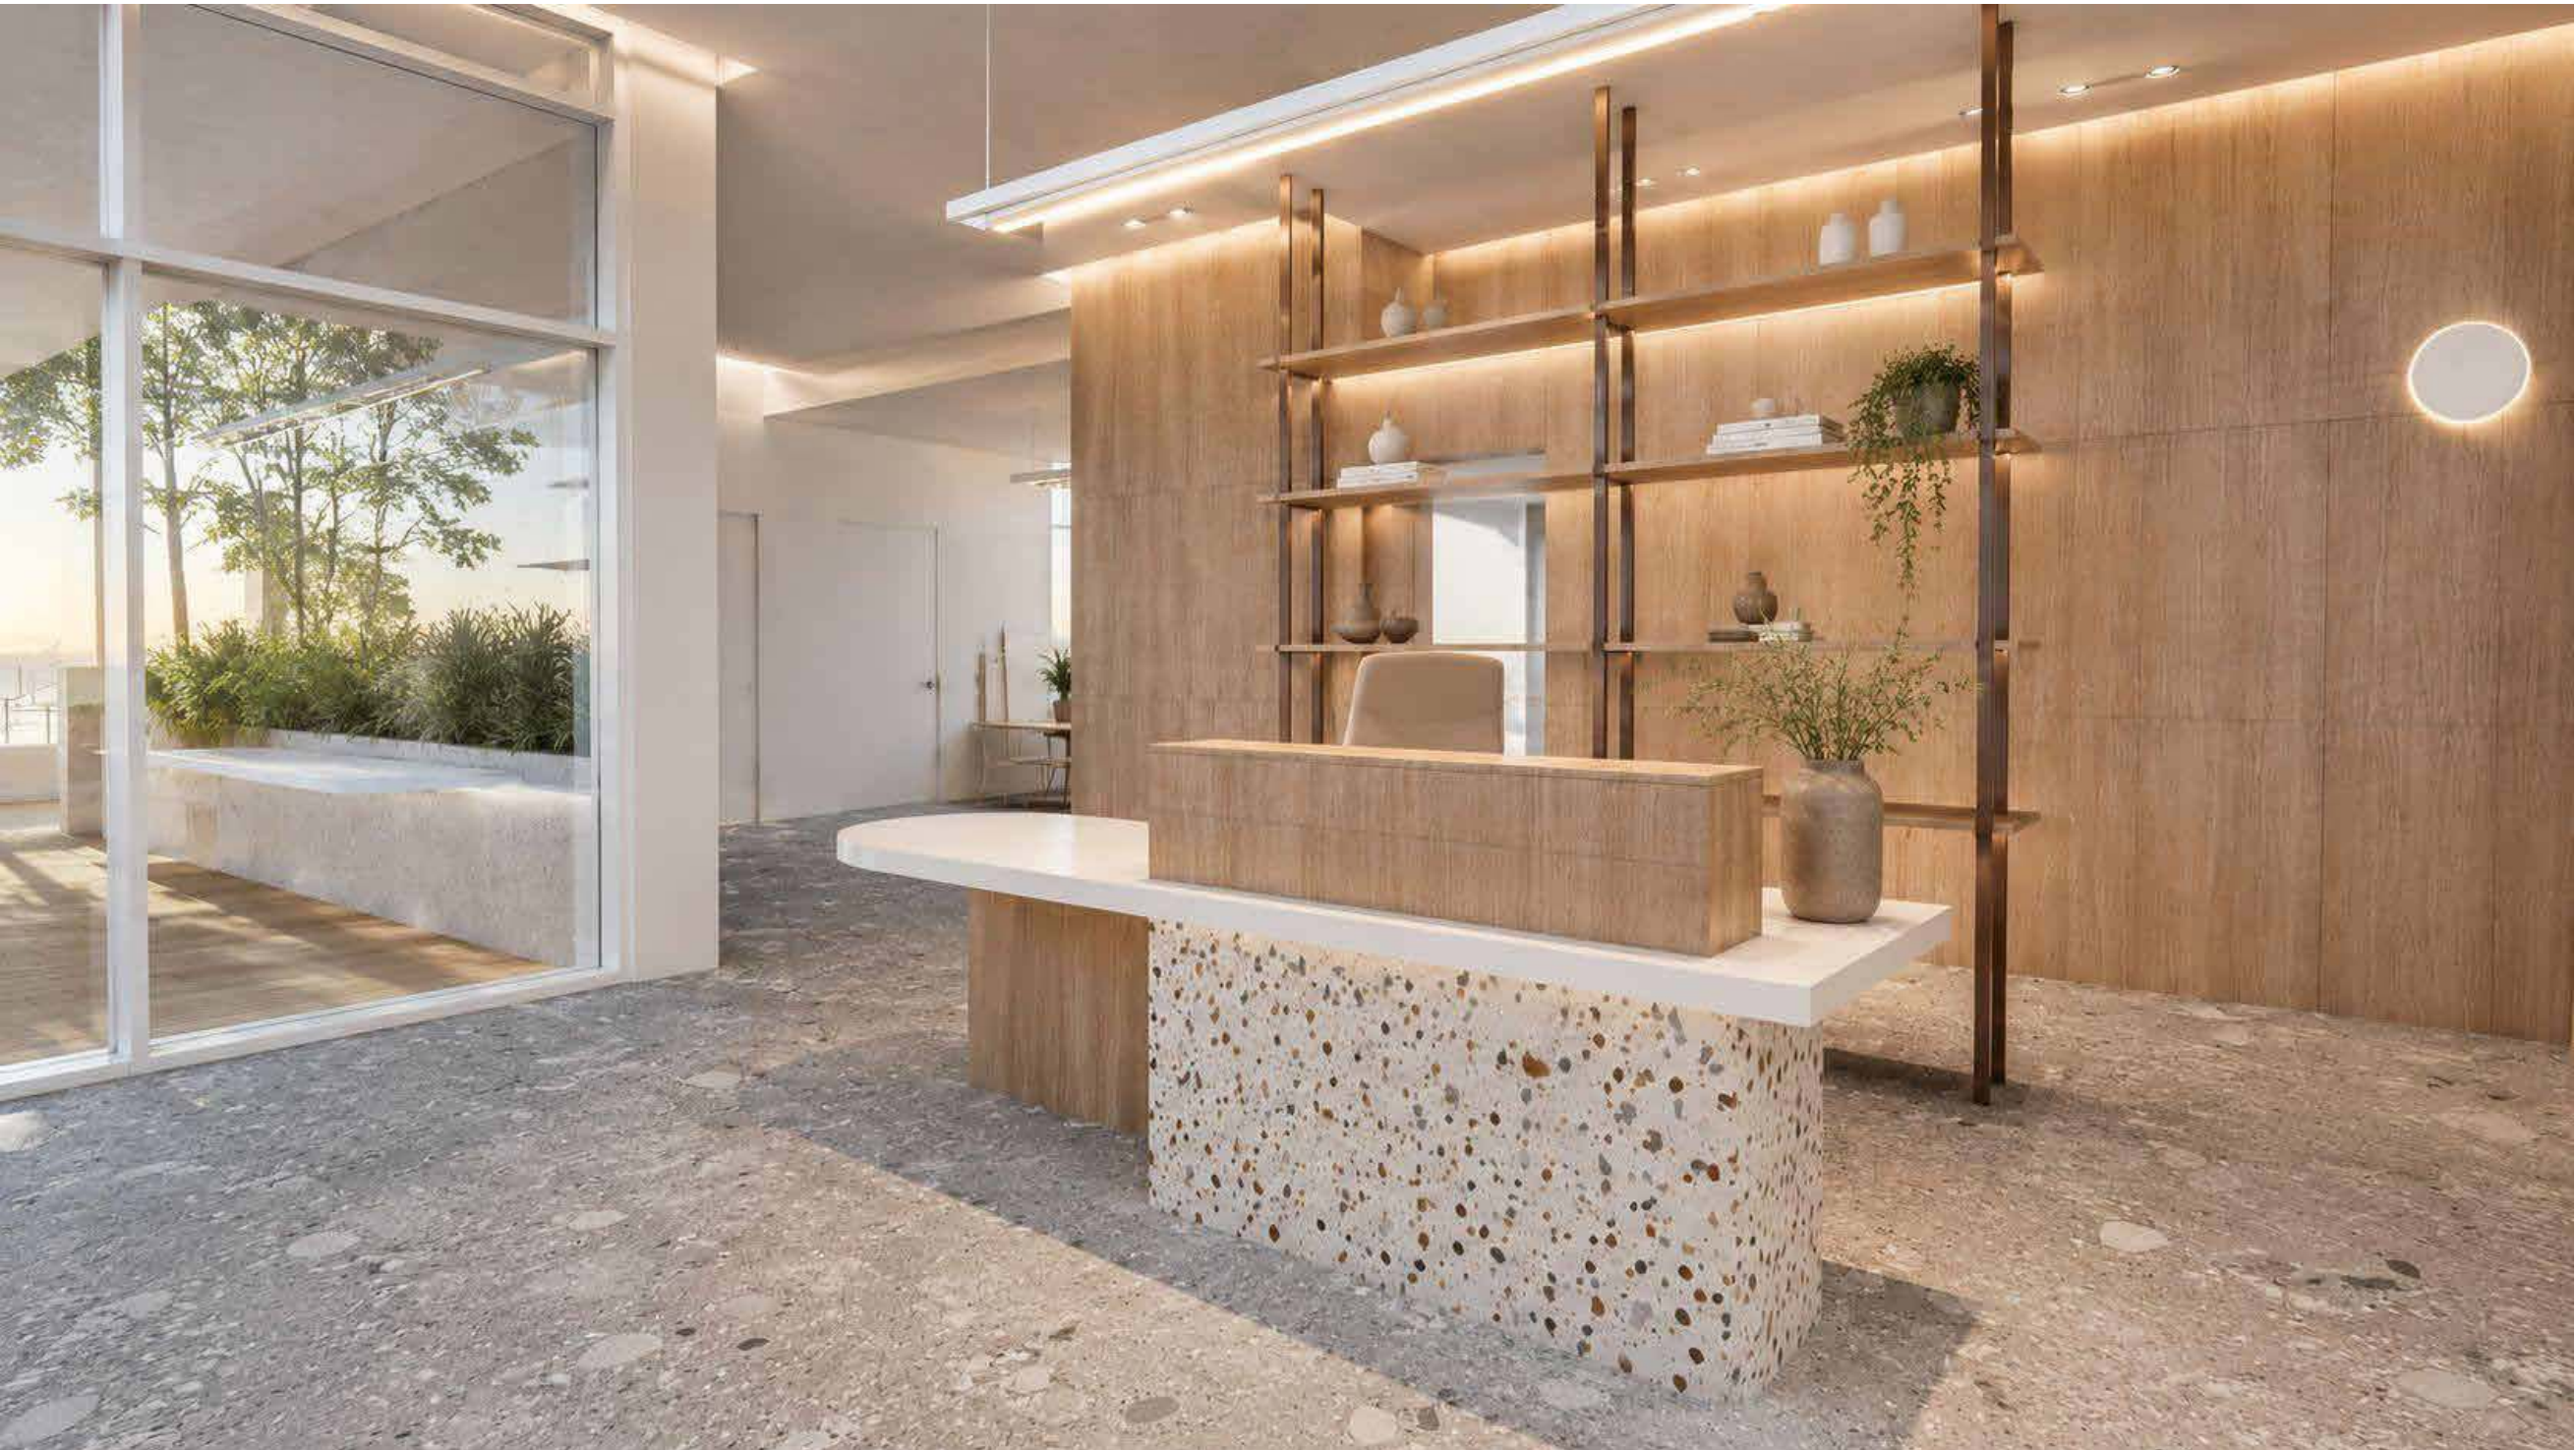
$$\begin{array}{c} \text{BB} \quad \neg \neg \Pi \\ 1 : 10 \end{array}$$

שם הפרויקט:

מעונות סטודנטים



מס'	תיאור גיליון:	קמ"מ:
-00	שער	
-01	ניתוח סביבה	
-02	סקיצות פרוגרמה	
-03	הדמיות	

פיתוח שטח		
-04	תכנית קומות קרקע	1:100
-05	תכנית קומות א	1:100

תכניות שחור לבן		
-06	תכנית קומות קרקע	1:100
-07	תכנית קומות א	1:100
-08	תכנית קומות ב	1:100
-09	תכנית גגות	1:100
-10	חתיכים	1:100
-11	חזיתות	1:100
-12	חזיתות	1:100

תכנית עבודה		
-13	תכנית עבודה קומה א	1:50
-14	חתך א-א', ב-ב'	1:50
-15	חזית צפונית, מערבית	1:50

פרטי ביין		
-16	מדגמות תכניות, פרטים	1:20 1:5
-17	מדגמות חתיכים	1:20
-18	קיר ייחודי-חתיכים	1:20
-19	קיר ייחודי-פרטים	1:5

עיצוב פנים		
-20	תכנית ריהוט, ריצוף	1:50 1:50
-21	תכנית חזקה מלאו אוור	1:50
-22	הדמיות ופריסת קיר	1:50
-23	תכנון דלפק	1:20 1:10

-24	עיצוב חדר לדוגמא	1:50
קונסטרוקציה		
-25	תכנית קונסטרוקציה	1:100

מגיש/ה:

כרמל סעדון


שם ראש המגמה:

שרון גפני

שם המנחה:


לית'

תאריך:

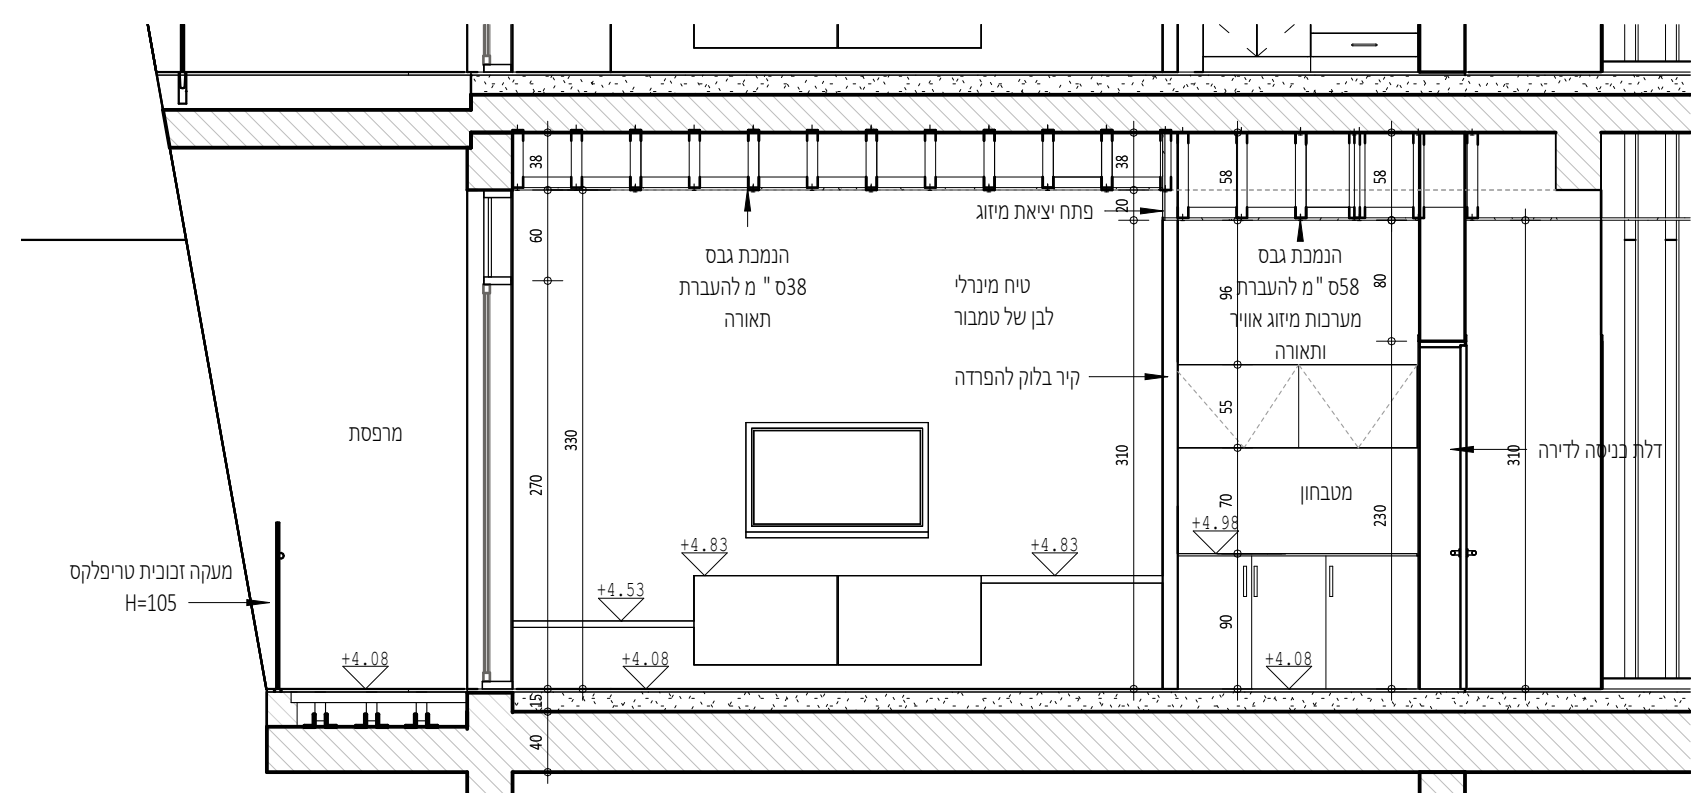


פריסה קיר טלוויזיה

1 : 50

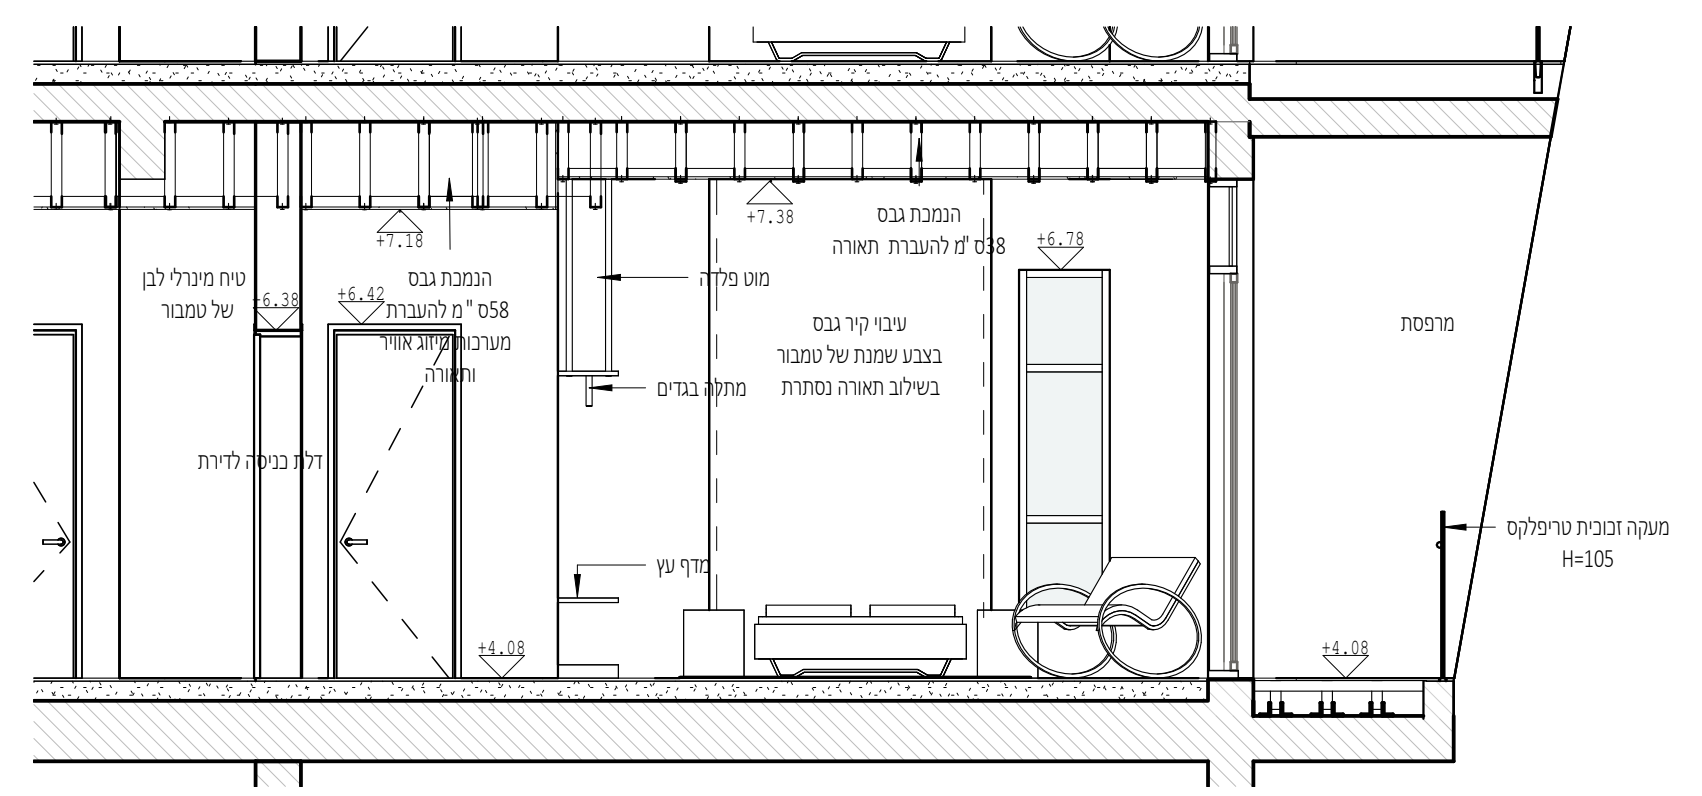


פריסת חדר מבט למיטה

1 : 50

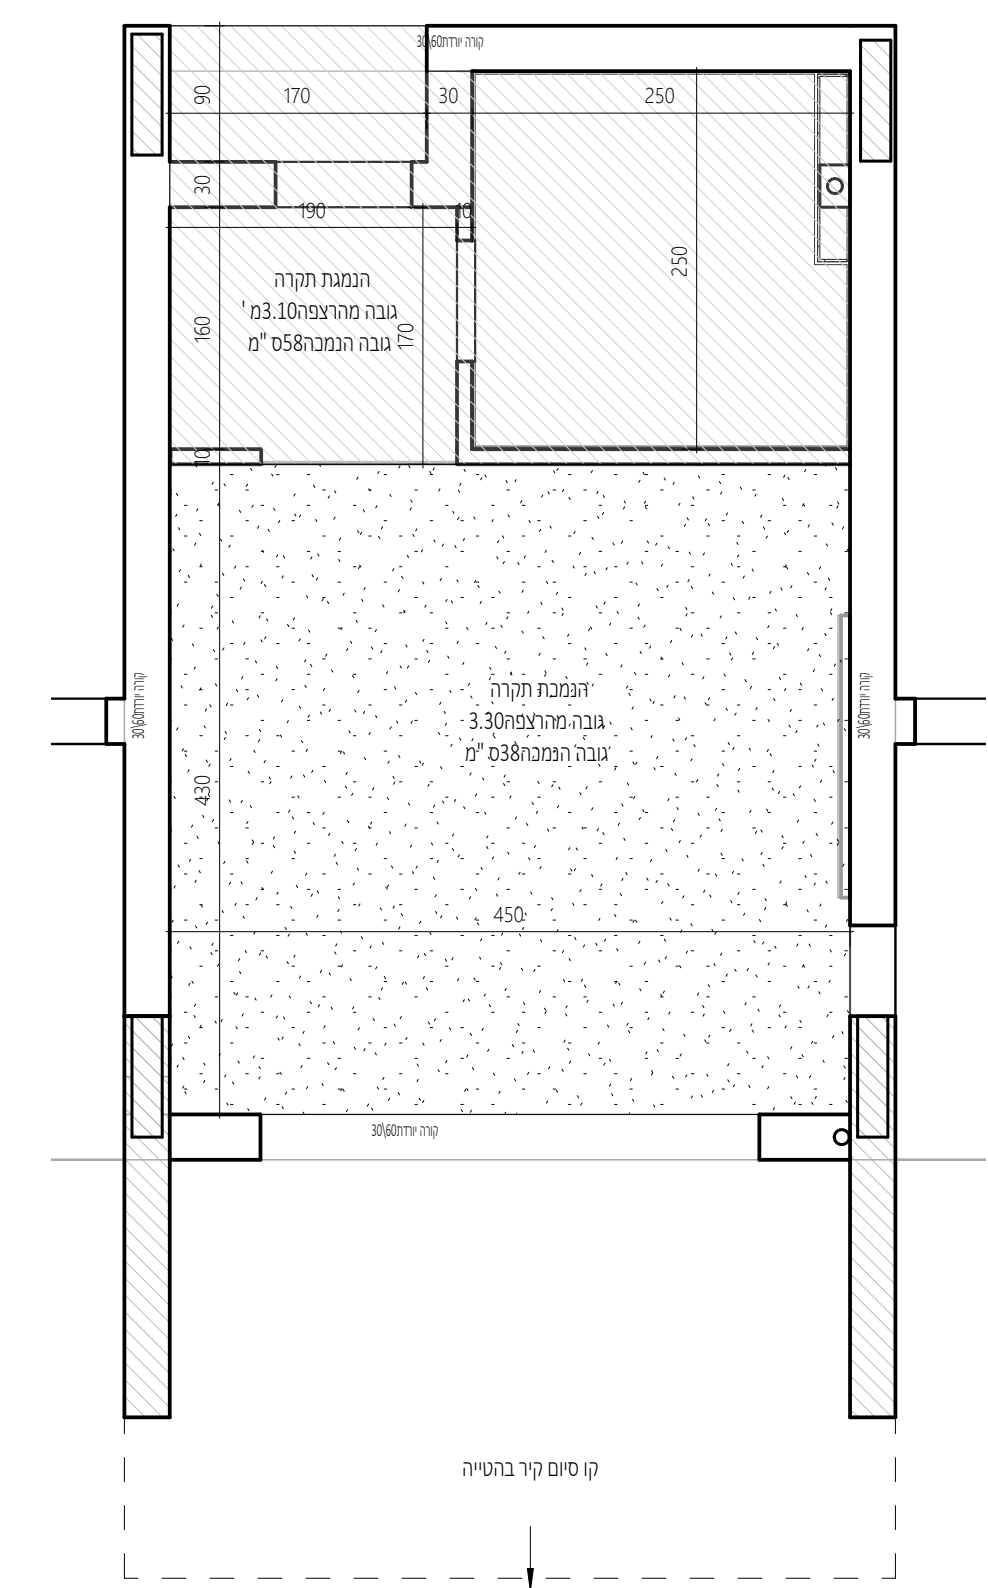


תכנית תקרה ותאורה

1 : 50

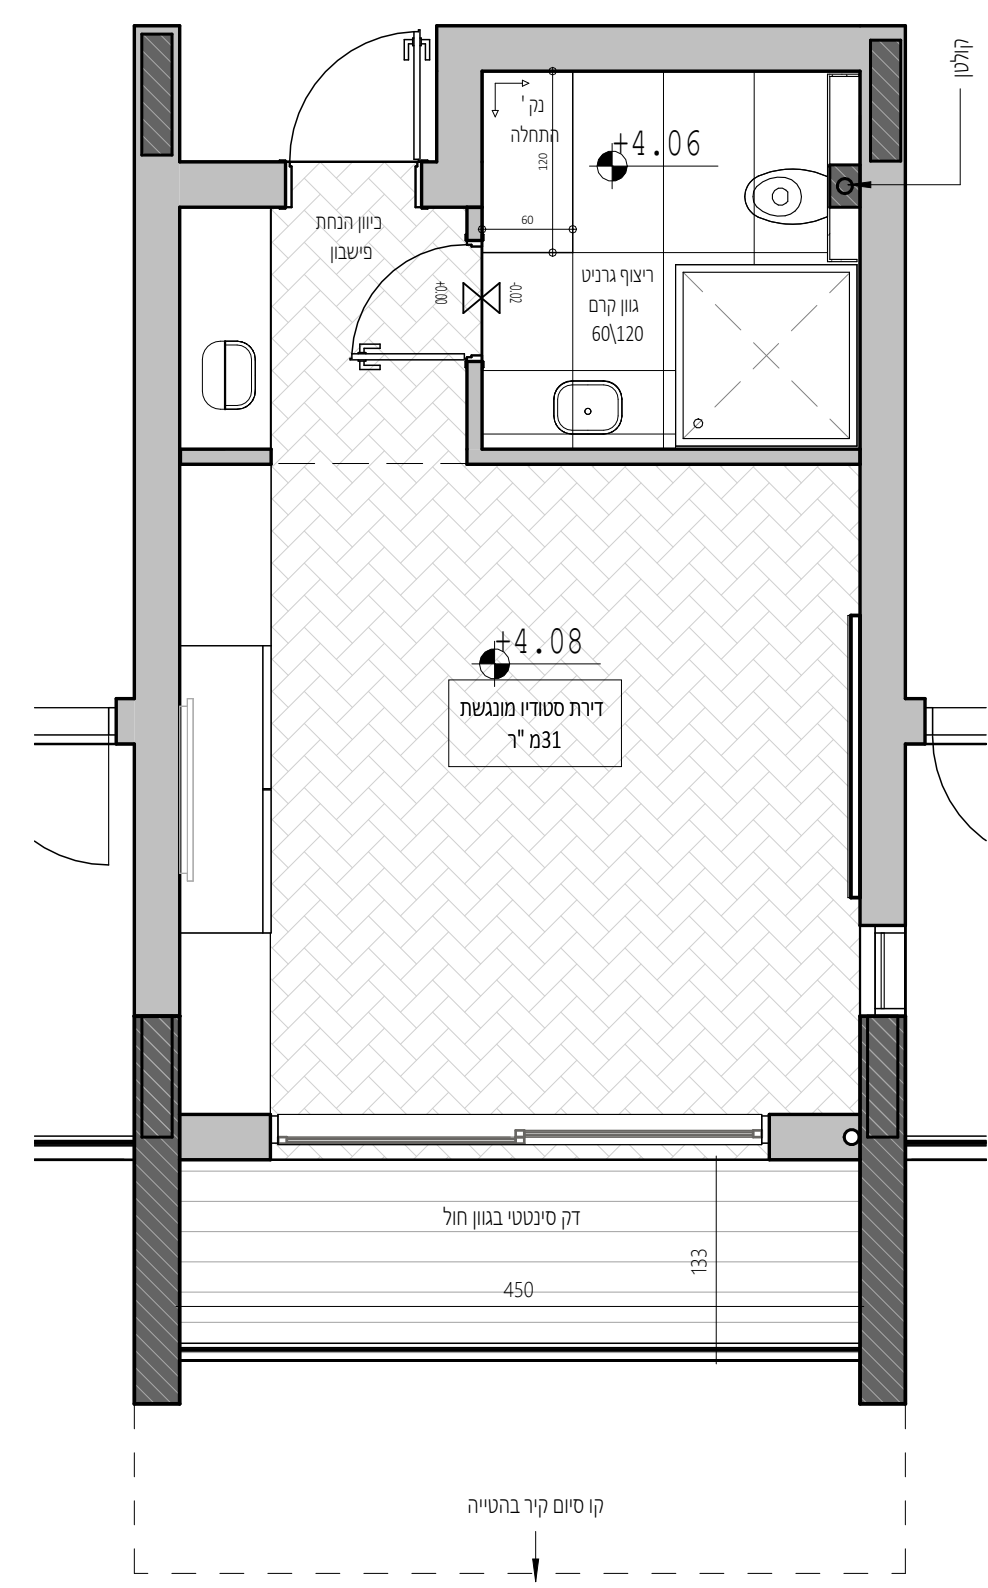

תכנית ריצוף חדר לדוגמא

1 : 50

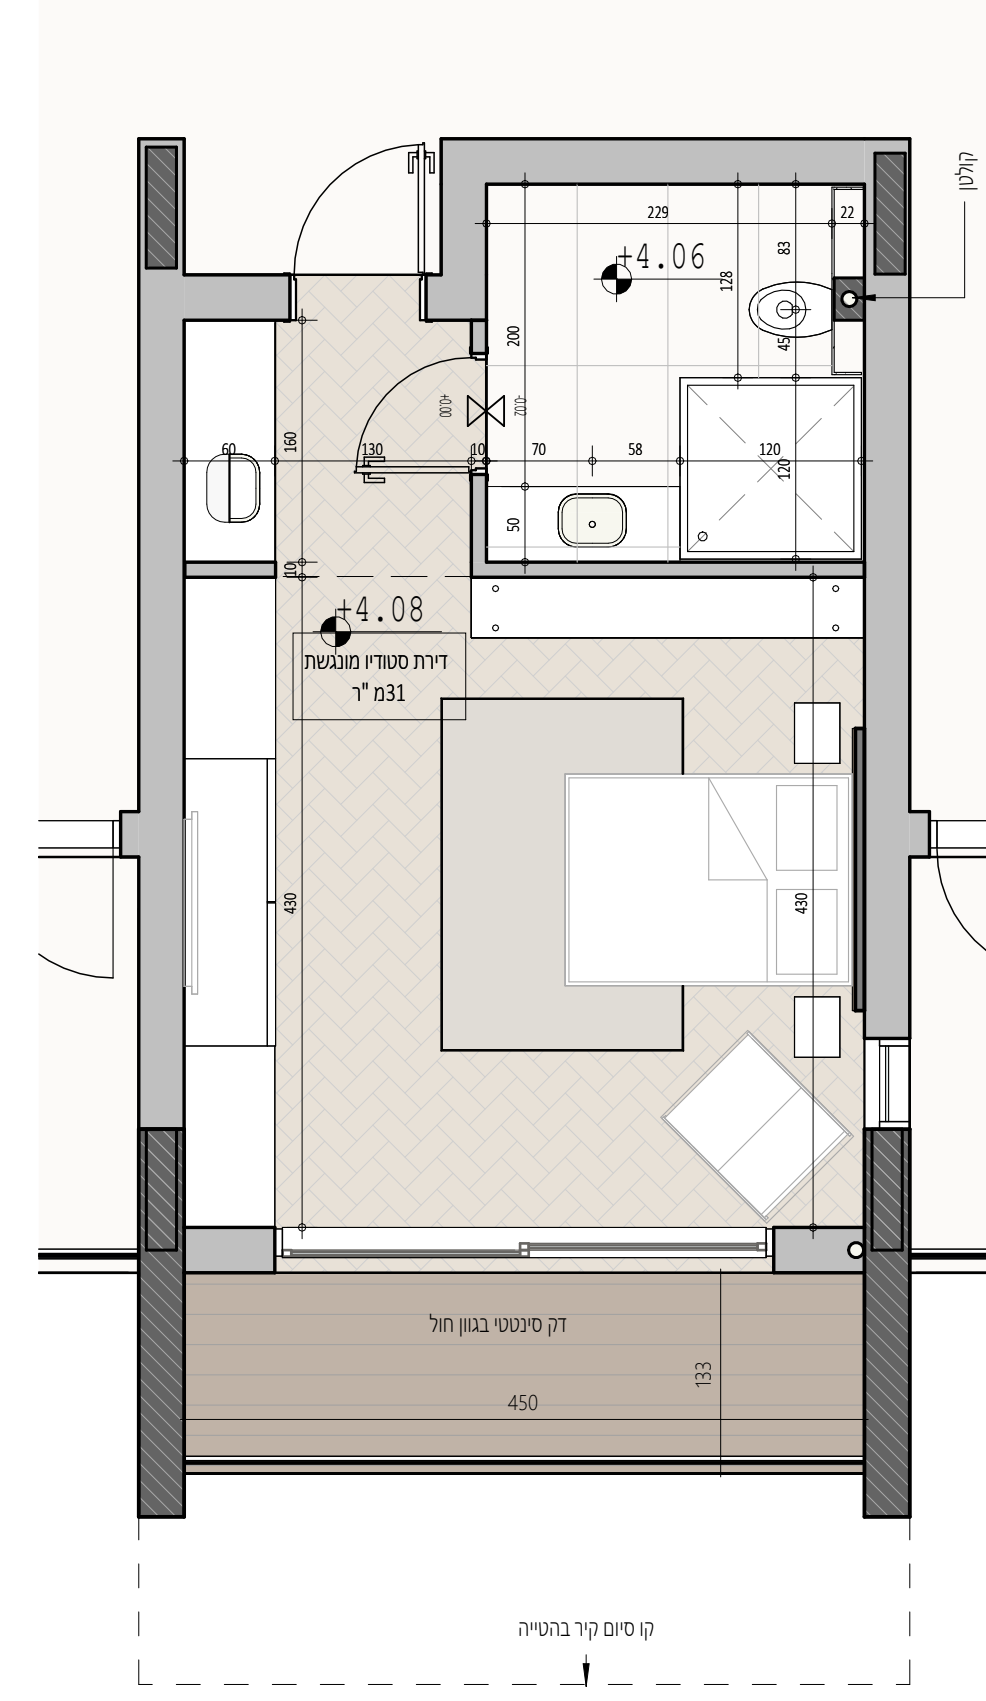

תכנית ריהוט חדר לדוגמא

1 : 50



עיצוב החדר:

העיצוב משלב בצורה מושלמת בין פונקציונליות לחמימות ביתית, ומתאים בדיוק לאווירה של חדר מעונות . ניצול החלל החכם בא לידי ביטוי ביחידת נגרות רציפה ובמערכת אחסון פתוחה , ששומרות יחד על תחושה מרווחת, קלילה ומאווררת . הבחירה בעץ בהיר וברצפת פישבון קלאסית מעניקה לחלל מראה עשיר ומוקפד , בגווני חרדל וכחול – בעוד שנגיעות הצבע בטקסטיל מוסיפות אופי צעיר ורענן על גבי הרקע – מעושן הניטרלי.



שם הפרויקט:

מעונות סטודנטים



מס'	תיאור גיליון:	קנ"מ:
-00	שער	
-01	ניתוח סביבה	
-02	סקיצות פרוגרמה	
-03	הדמיות	
פיתוח שטח		
-04	תכנית קומת קרקע	1:100
-05	תכנית קומה א	1:100
תכניות שחור לבן		
-06	תכנית קומת קרקע	1:100
-07	תכנית קומה א	1:100
-08	תכנית קומה ב	1:100
-09	תכנית גגות	1:100
-10	חתיכים	1:100
-11	חיתות	1:100
-12	חיתות	1:100
תכנית עבודה		
-13	תכנית עבודה קומה א	1:50
-14	חתך א-א', ב-ב'	1:50
-15	חזית צפונית, מערבית	1:50
פרטי בנין		
-16	מדרגות-תכניות, פרטים	1:20 1:5
-17	מדרגות-חתיכים	1:20
-18	קיר ייחודי-חתיכים	1:20
-19	קיר ייחודי-פרטים	1:5
עיצוב פנים		
-20	תכנית ריהוט, רישוף	1:50
-21	תכנית חוקי מילוי אזור	1:50
-22	הדמיות פריסת קיר	1:50
-23	תכנון דלפק	1:20 1:10
-24	עיצוב חדר לדגמא	1:50

קונסטרוקציה
תכנית קונסטרוקציה 1:100


מגישה:
כרמל סעדון
שם ראש המגמה:
שרון גפני
שם המנחה:
ליתית

תאריך:

23/06/2026


רצפת קומת קרקע

1 : 100

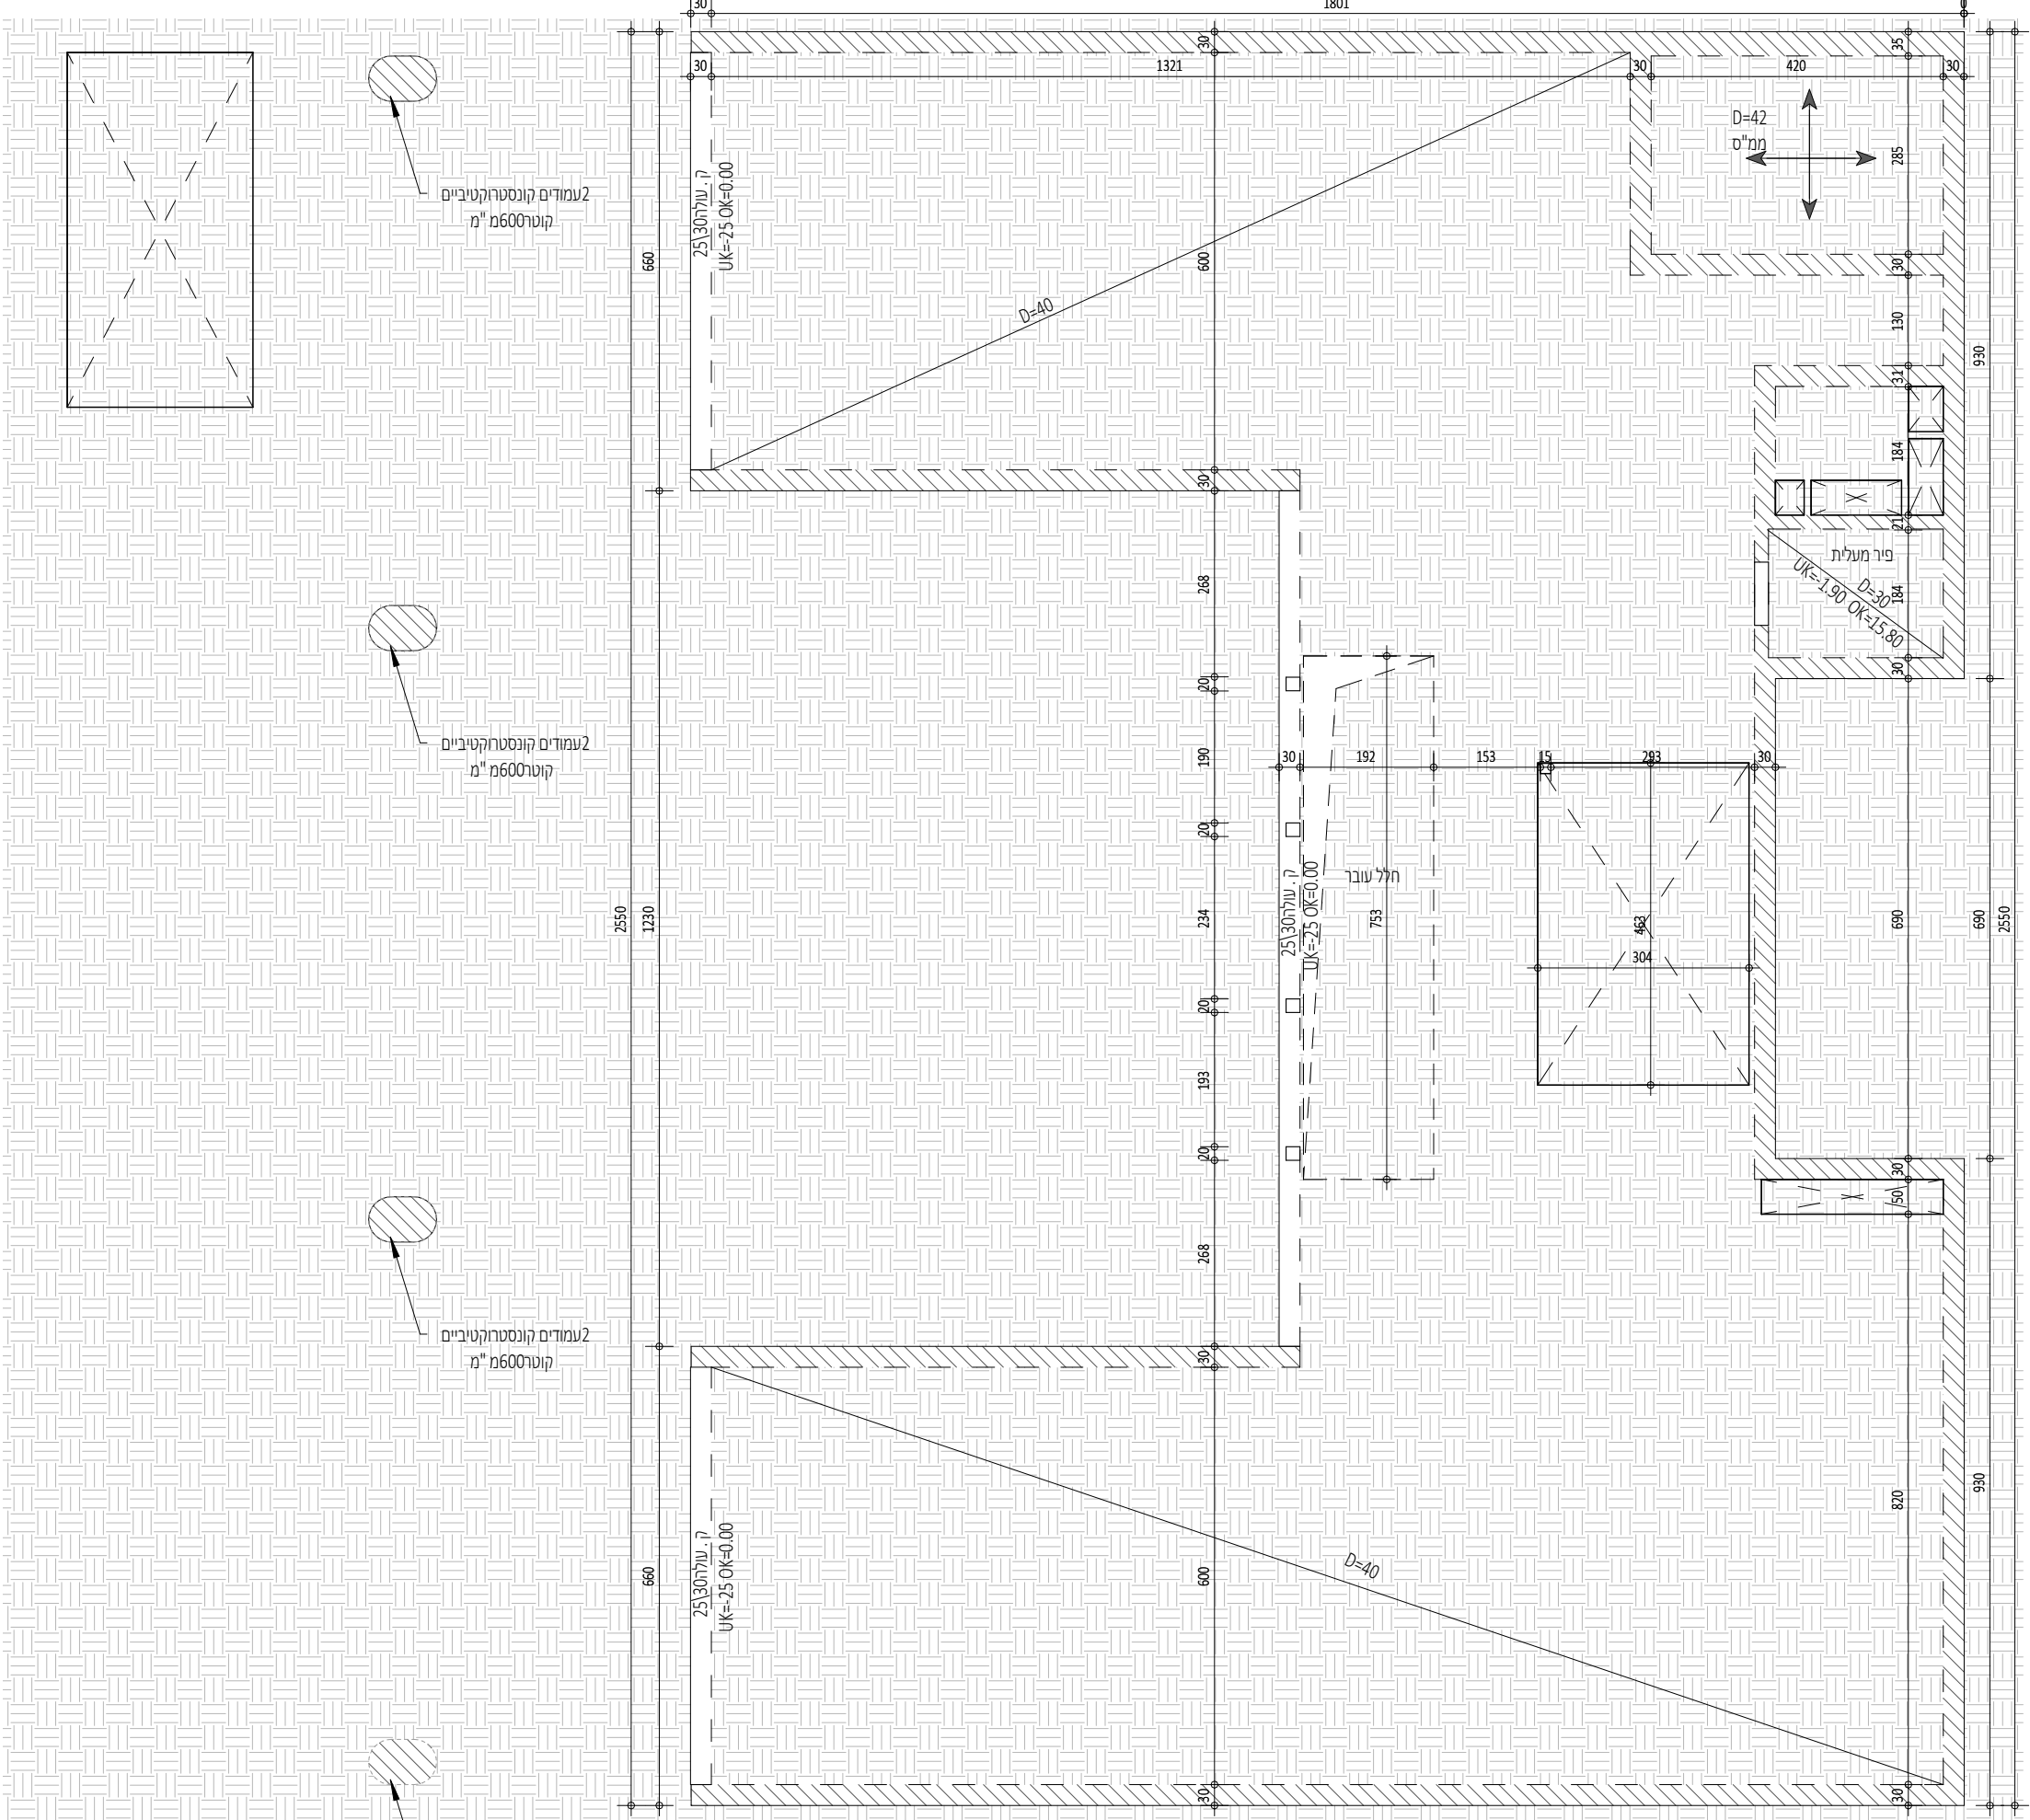


רצפת קומה ב'

1 : 100

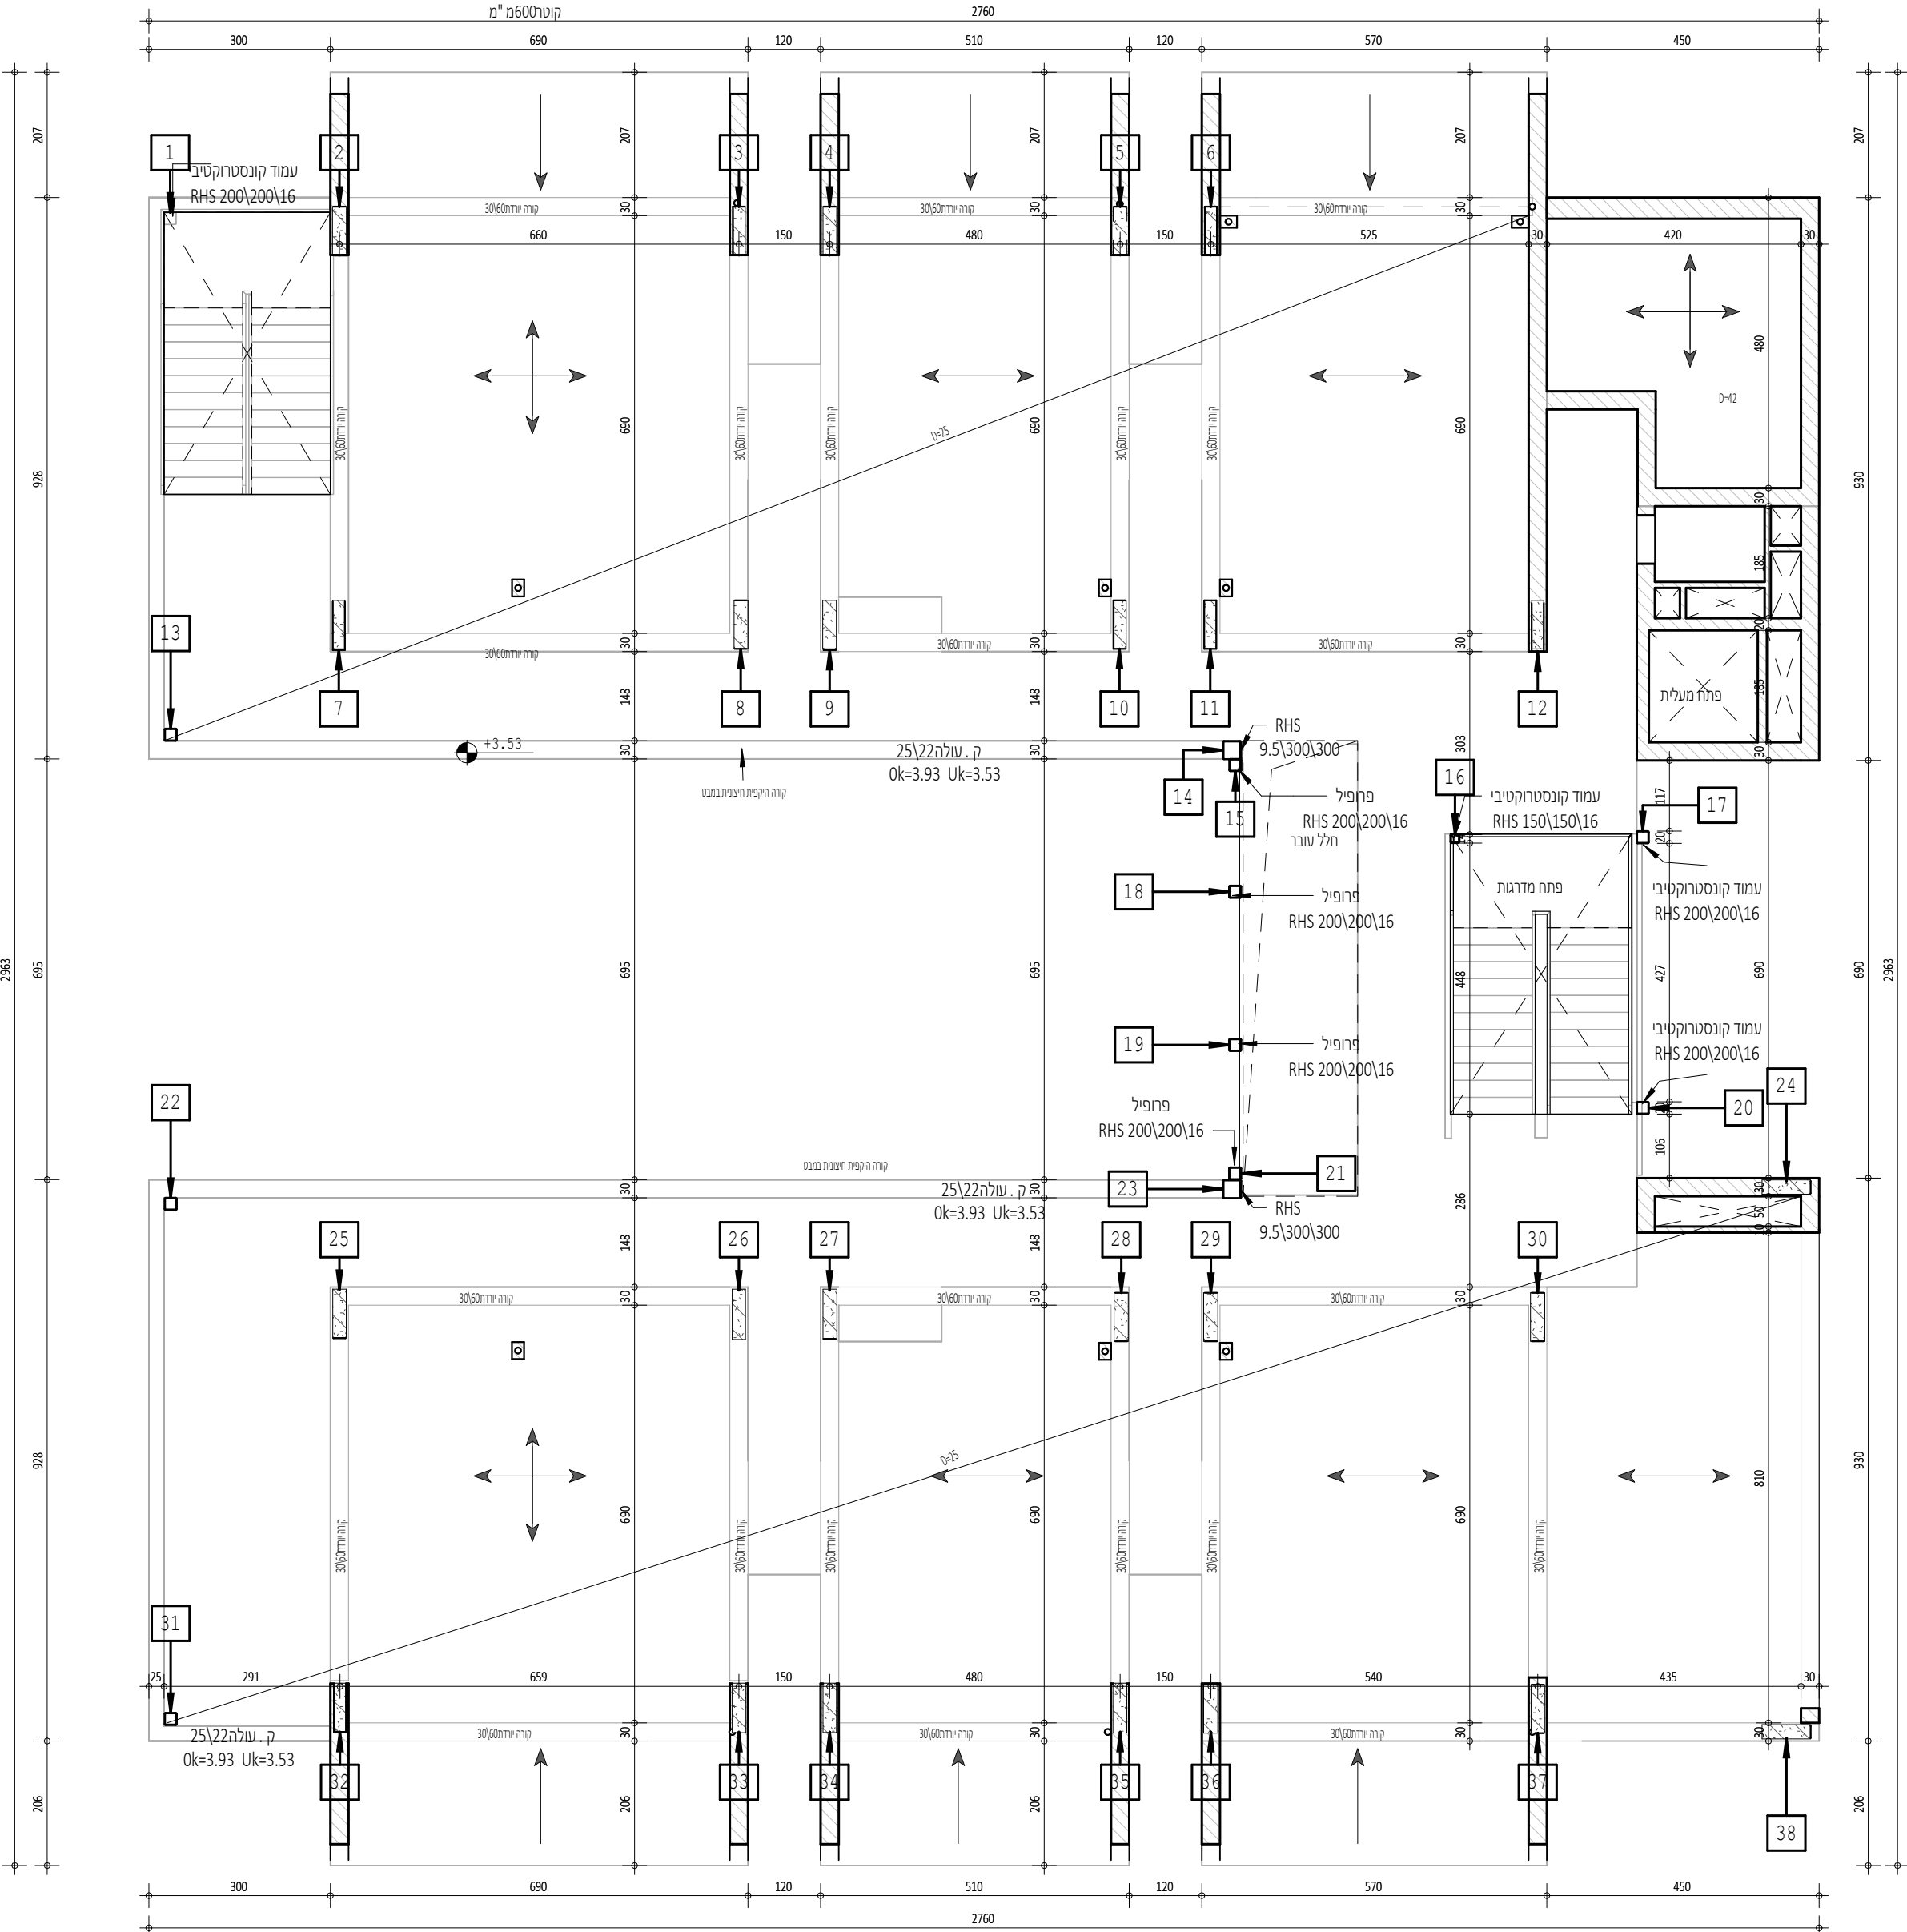

רצפת קומה א'

1 : 100

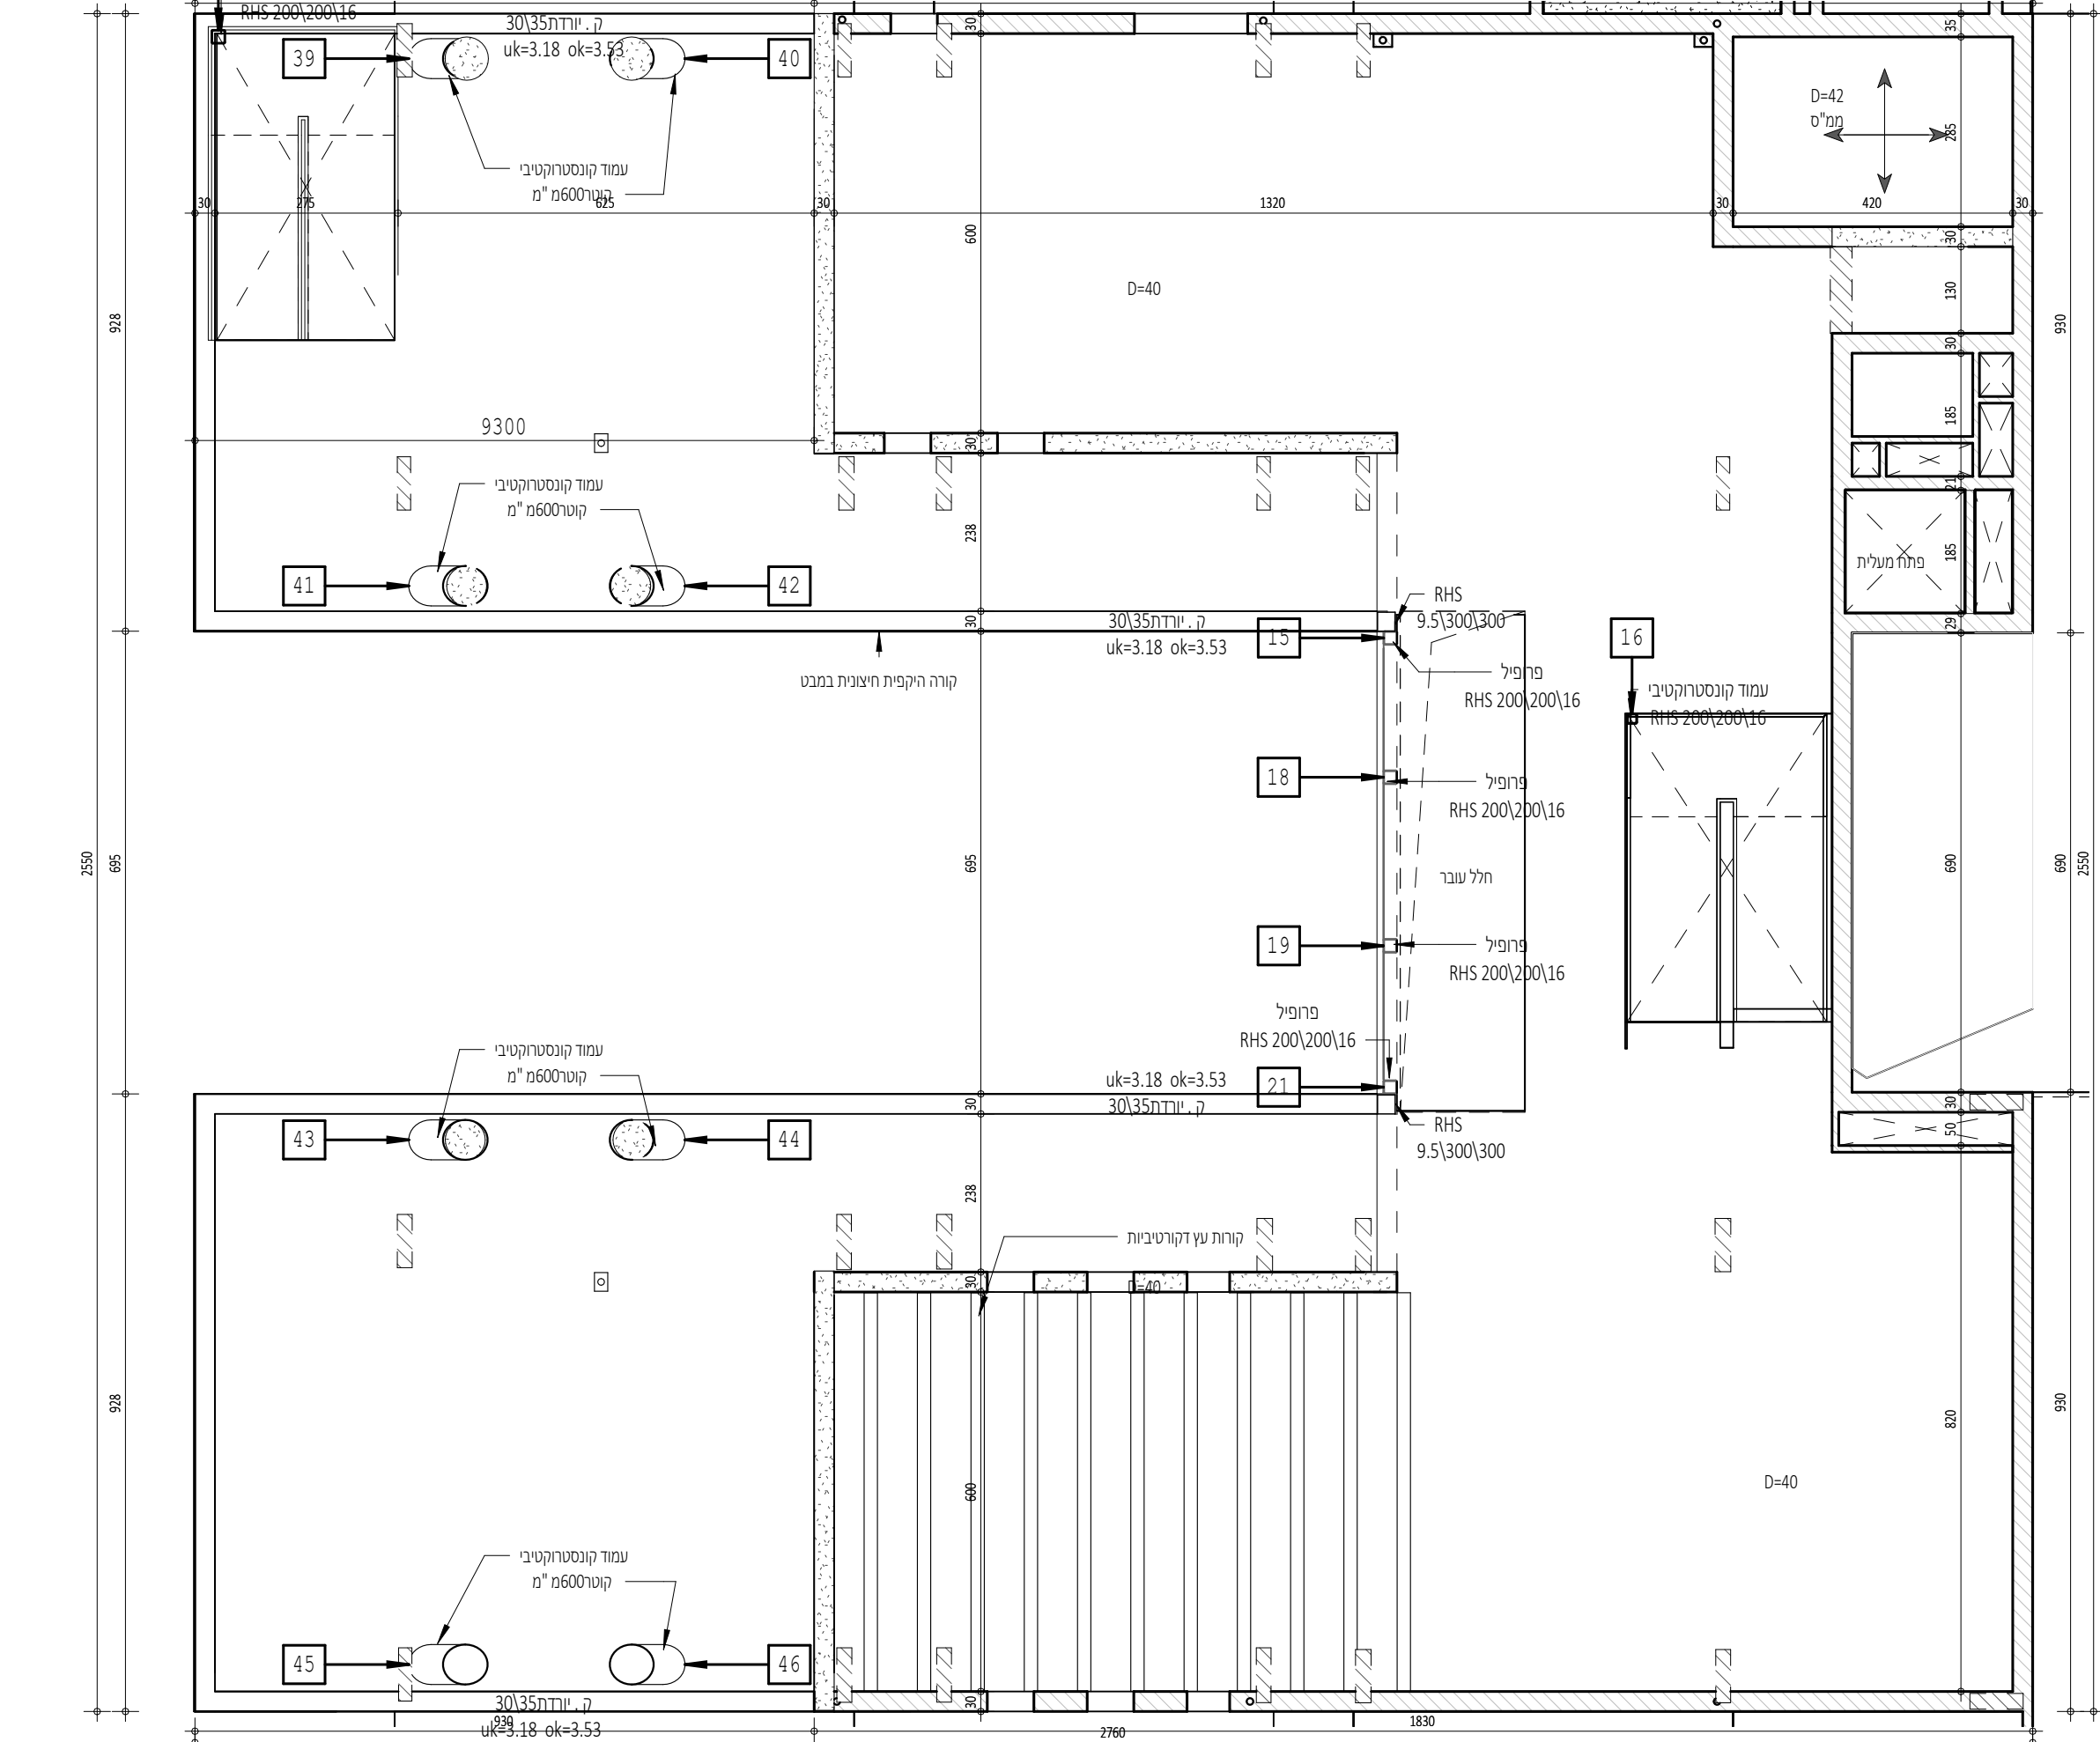

רצפת קומת גג

1 : 100

